



# Change register

## Council Documentation

			PM	Drawn	Checked
Issue 01	6 February 2025	First issue	RL	CO	CR/RL/TD
Issue 02	19 February 2025	Updates based on client feedback: Location 11 added, RMG scope updated	RL	CO	CR/RL
Issue 03	17 March 2025	Updates throughout pack	RL	CO	CR/RL/NCW
Issue 04	20 March 2025	Updates to location 6 & 10	RL	CO	NCW
Issue 05	27 March 2025	General updates	RL	CO	CR/RL

Endorsed by	Name	Signed	Date	Issue No.

**diadem**

Australia  
1300 613 934

New Zealand  
+64 9 377 3736

Hong Kong  
+613 9670 6767  
info@diadem.co  
diadem.co

General note: These drawings are prepared to communicate design intent only.  
All message content is indicative. All structural frames, footings and connections to be as per  
Engineer's specifications and requirements. Contractor to ensure all materials, measurements,  
fixing details and methods are suitable for the site application before manufacture.

©Copyright Diadem Pty Ltd  
Proprietary information. All rights reserved. All rights reserved. All rights reserved.  
The information, ideas and concepts contained in this document are confidential. The recipient(s)  
of this document is prohibited from disclosing such information to any person without the prior  
written consent of Diadem. Figured dimensions shall take precedence to scaled.

## Logo proportions



INLINE LOGO



STACKED LOGO



PANORAMIC LOGO


LOGO ALIGNMENT CRITICAL  
ALL VERSIONS OF THE LOGO

# Site plan – City east campus: Schulz Building

CAMPUS BOUNDARY HIGH LEVEL SIGN LOCATION



OVERALL SITE PLAN  
NOT TO SCALE

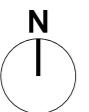


# Site plan – City east campus: Nexus 10 Building

CAMPUS BOUNDARY HIGH LEVEL SIGN LOCATION



OVERALL SITE PLAN  
NOT TO SCALE

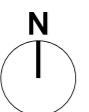

New signs  
(day time)



Location 6



Location 9




Location 10



Location 11

## ILLUMINATIONS

ALL SIGNS WILL ILLUMINATE WHITE AT NIGHT TIME,  
REGARDLESS OF APPEARANCE DURING THE DAY.  
IN ADDITION, ALL SIGNS WILL BE FITTED WITH RGBW LEDs,  
TO ALLOW THE ABILITY TO ILLUMINATE IN MULTIPLE COLOURS.

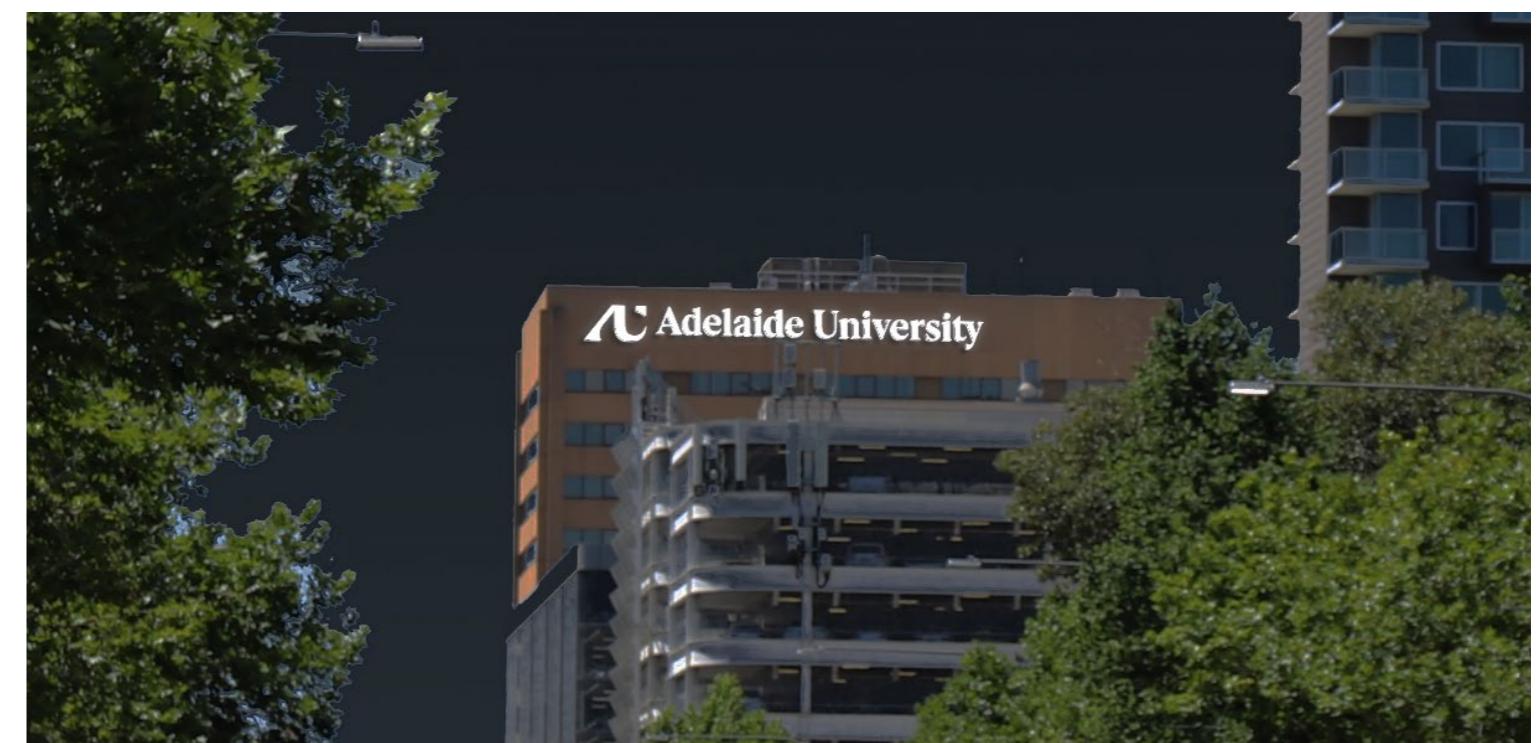

# Site plan – City east campus

CAMPUS BOUNDARY HIGH LEVEL SIGN LOCATION



OVERALL SITE PLAN  
NOT TO SCALE



**INSTRUCTIONS**

REMOVE EXISTING SIGN AND MAKE GOOD TO REMOVE LOCATION.

MAKE GOOD INCLUDES THE FOLLOWING WHERE APPLICABLE:

- EXISTING CLADDING REMOVED
- NEW CLADDING INSTALLED TO MATCH EXISTING
- REPAINT SURROUNDING WALL AREAS
- ANY IMPACTED SUBSTRATES FROM REMOVAL PROCESS

TO BE REINSTATED TO EXISTING CONDITIONS

**RMG2****Removal scope**

Existing signage

**RMG2-F****RMG2-F**



**EXISTING CONDITIONS**



**PROPOSED LOCATION**



**SIGN LOCATION**

SCALE 1:2000



**LOCATION SPECIFIC INFORMATION**

**LOGO**


FABRICATED ALUMINIUM, RETURNS PAINTED WHITE FLEXFACE SIGN FACES WITH BLUE DAY/NIGHT VINYL ALUMINIUM TRIM ANGLES TO SECURE SIGN FACE

**LETTERS**

FABRICATED ALUMINIUM, RETURNS PAINTED WHITE CORIAN SIGN FACES WITH BLUE DAY/NIGHT VINYL ALL INTERNAL SIGN FACES PAINTED WHITE LOGO AND LETTERS FIXED DIRECTLY TO BUILDING FAÇADE, INTERNALLY ILLUMINATED THROUGH FACES, SIGN TO ILLUMINATE WHITE AT NIGHT.


LED DRIVERS MUST BE INSTALLED IN AN AGREED-UPON ACCESSIBLE AREA AND, IF APPROPRIATE, THE REUSE OF THE EXISTING 240V SUPPLY FROM THE EXISTING SIGNS IS PREFERRED.

EXISTING SIGN TO BE REMOVED.

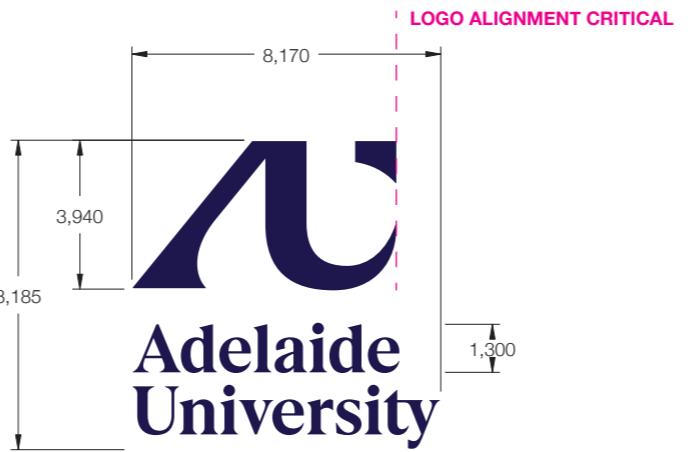

**SIGN DETAIL**

SCALE 1:200

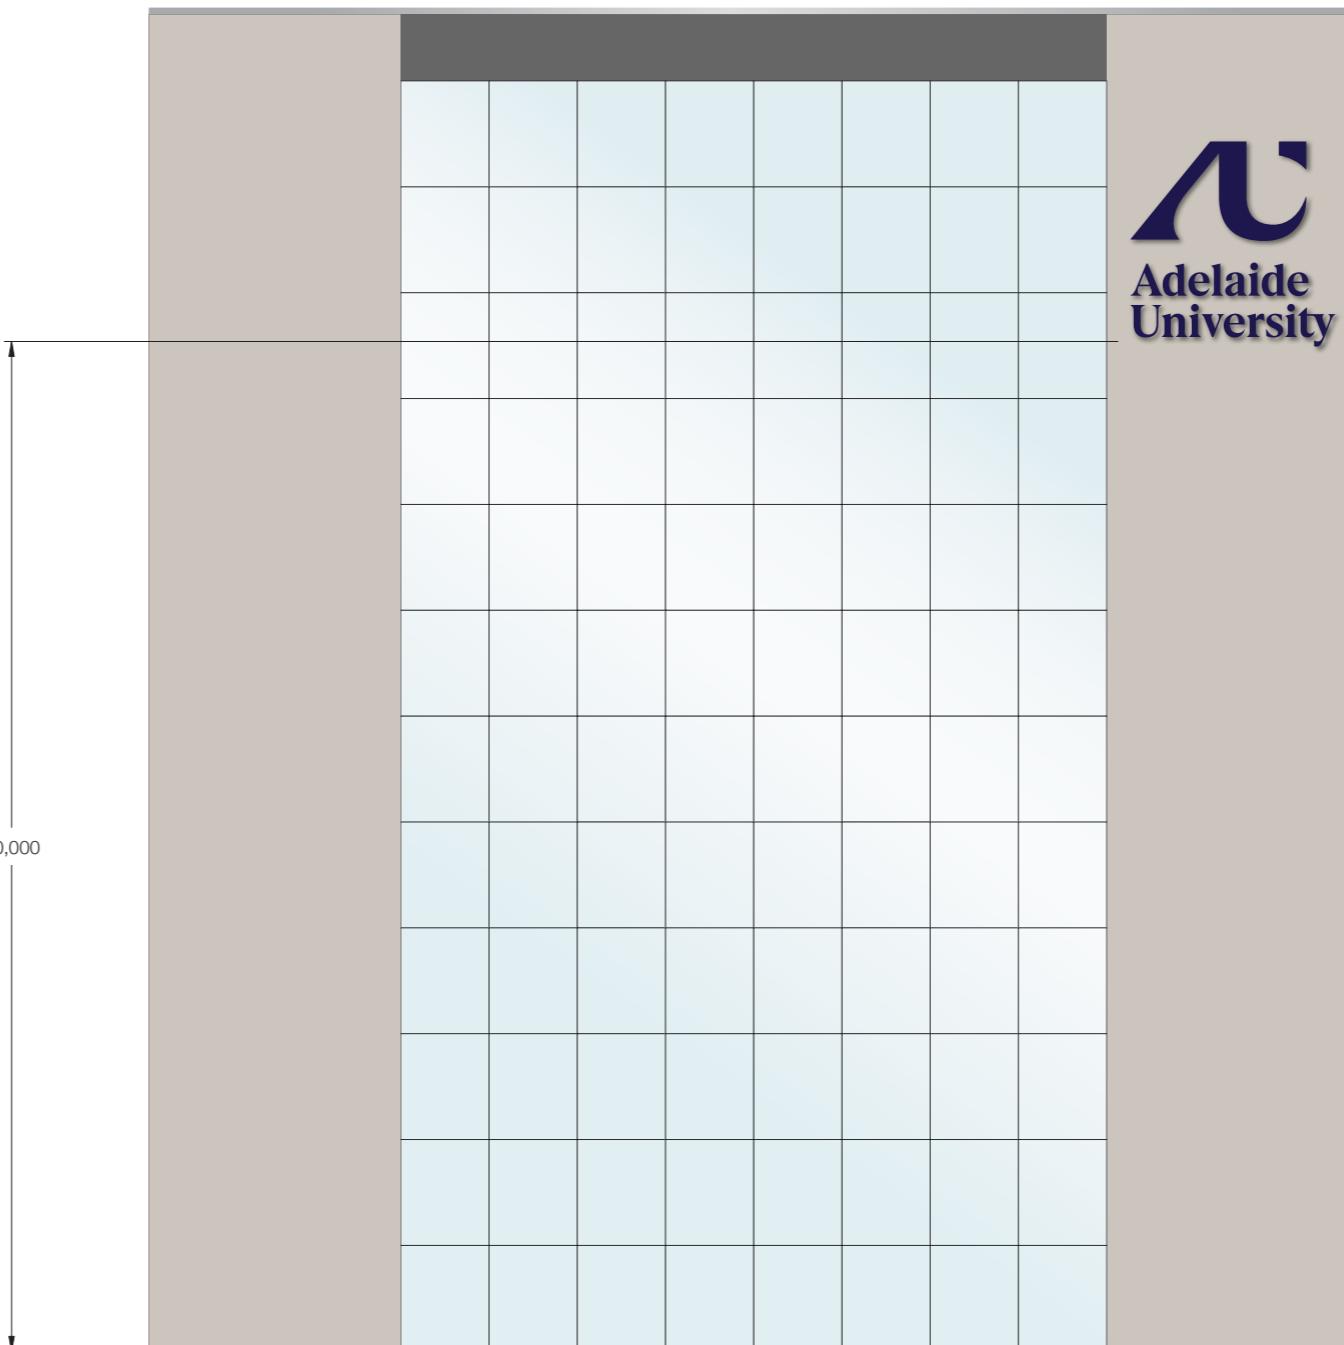

**NORTH ELEVATION**

SCALE 1:300

# Schulz Building

# Location 6

Adelaide SA 5000

**High level sign – stacked format**  
Wall mounted  
Single sided  
Illuminated

Drawing title  
**General arrangement**

Issue Issue date  
**ISSUE 05** 27 MARCH 2025

Drawing no Scale  
- @A3

PM Drawn Checked  
RL CO CR/RL/NOW

Revision  
- - -

**Not for construction**

General note: These drawings are prepared to communicate design intent only. All message content is indicative. All structural frames, footings and connections to be as per engineer's specifications and requirements. Contractor to ensure all materials, measurements, fixing details and methods are suitable for the site application before manufacture.

Client  
ADELAIDE UNIVERSITY

Project  
CITY WEST CAMPUS

Document file name  
**26304-DOC\_CITY\_EAST\_SKY\_SIGNS-05**

**diadem**

Australia

1300 613 934

New Zealand

+64 9 377 3736

Hong Kong

+61 3 9670 6767


info@diadem.co

diadem.co

©Copyright Diadem Pty Ltd  
Reproductions of the whole or part of this document constitutes an infringement of copyright. The information, ideas and concepts contained in this document are the intellectual property of the recipient(s) of this document. It is prohibited from disclosing such information to any person without the prior written consent of Diadem. Figured dimensions shall take precedence to scaled.

Adelaide SA 5000

**High level sign – stacked format**  
Wall mounted  
Single sided  
Illuminated

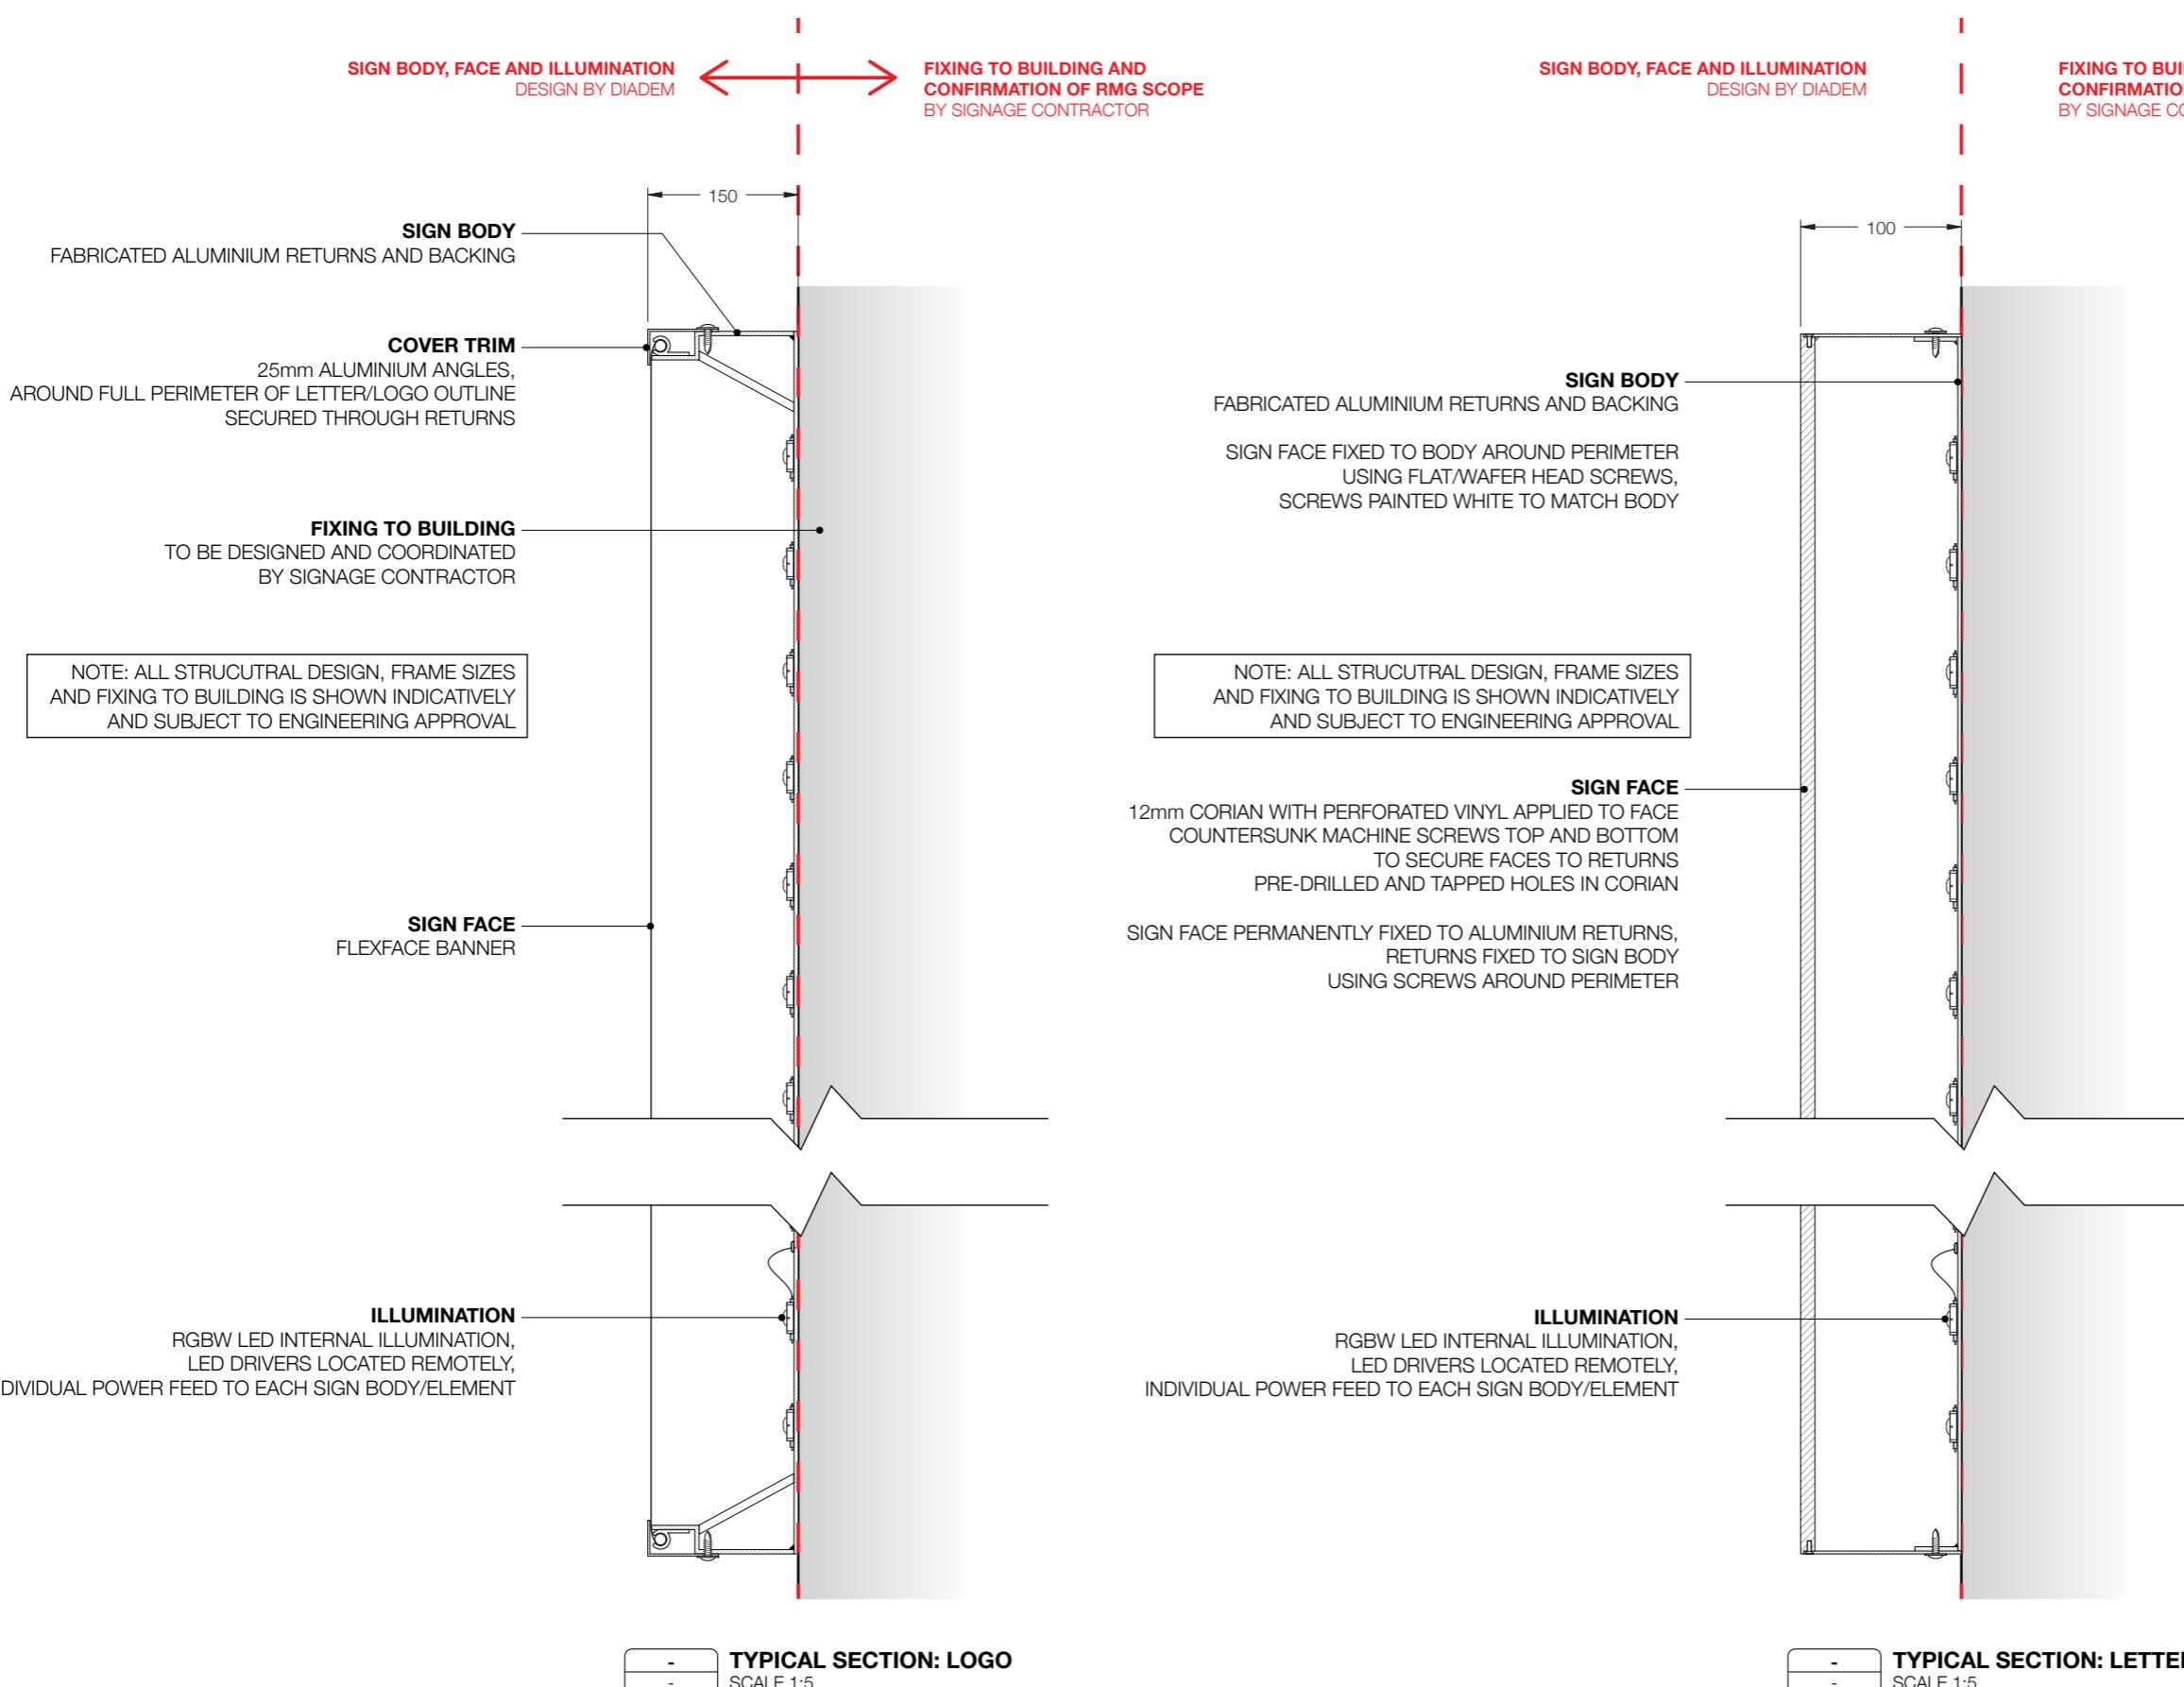

Drawing title

Section detail

Issue Issue date  
ISSUE 05 27 MARCH 2025

Drawing no Scale  
- @A3

PM Drawn Checked  
RL CO CR/RL/NOW

Revision  
- - -

**Not for construction**

General note: These drawings are prepared to communicate design intent only. All message content is indicative. All structural frames, footings and connections to be as per engineer's specifications and requirements. Contractor to ensure all materials, measurements, fixing details and methods are suitable for the site application before manufacture.

Client  
ADELAIDE UNIVERSITY

Project  
CITY WEST CAMPUS

Document file name  
26304-DOC\_CITY\_EAST\_SKY\_SIGNS-05

**diadem**

Australia  
1300 613 934

New Zealand  
+64 9 377 3736

Hong Kong  
+61 3 9670 6767

info@diadem.co  
diadem.co

©Copyright Diadem Pty Ltd  
Reproductions of the whole or part of this document constitutes an infringement of copyright. The information, ideas and concepts contained in this document are the intellectual property of the recipient(s) of this document. It is prohibited from disclosing such information to any person without the prior written consent of Diadem. Figured dimensions shall take precedence to scaled.

Adelaide SA 5000

**High level sign – stacked format**  
 Wall mounted  
 Single sided  
 Illuminated

Drawing title \_\_\_\_\_

**Removal scope**

EXISTING CONDITIONS

**RMG:** REMOVE EXISTING SIGN AND MAKE GOOD TO FAÇADE INCLUDING BUT NOT LIMITED TO, WATERPROOFING, PATCHING AND COLOUR MATCHING EXISTING REMOVAL POINTS TO REFLECT CURRENT BUILDING COLOUR AND CONDITIONS. CLEAN AND MAKE GOOD EXTENT OF EXISTING SIGN FOOTPRINT.

**ACCESS:** CRANE OR ROPE ACCESS FROM ROOF TO BE DETERMINED ON SITE BY CONTRACTOR WITH FACILITIES TEAM.

CONTRACTOR TO ALLOW FOR ALL RELEVANT AUTHORITY AND TRAFFIC MANAGEMENT REQUIREMENTS FOR INSTALLATION

**NOTE:** TELECOMMUNICATION ON ROOF, MAY REQUIRE SHUT DOWN, CONTRACTOR TO COORDINATE

Issue	Issue date
ISSUE 05	27 MARCH 2025

Drawing no	Scale
-	@A3

PM	Drawn	Checked
RL	CO	CR/RL/NOW

Revision
-- -

**Not for construction**

General note: These drawings are prepared to communicate design intent only. All message content is indicative. All structural frames, footings and connections to be as per engineer's specifications and requirements. Contractor to ensure all materials, measurements, fixing details and methods are suitable for the site application before manufacture.

Client  
ADELAIDE UNIVERSITY

Project  
CITY WEST CAMPUS

Document file name  
26304-DOC\_CITY\_EAST\_SKY\_SIGNS-05

**diadem**

Australia

1300 613 934

New Zealand

+64 9 377 3736

Hong Kong

+61 3 9670 6767

info@diadem.co

diadem.co

©Copyright Diadem Pty Ltd  
 Reproductions of the whole or part of this document constitutes an infringement of copyright. The information, ideas and concepts contained in this document are the copyright of Diadem. The recipient(s) of this document is prohibited from disclosing such information to any person without the prior written consent of Diadem. Figured dimensions shall take precedence to scaled.

# Schulz Building

# Location 10

Adelaide SA 5000

**High level sign – panoramic format**  
Wall mounted  
Single sided  
Illuminated



EXISTING CONDITIONS



PROPOSED LOCATION



SIGN LOCATION

SCALE 1:2000



## LOCATION SPECIFIC INFORMATION

### LOGO

FABRICATED ALUMINIUM, RETURNS PAINTED WHITE FLEXFACE SIGN FACES WITH BLUE DAY/NIGHT VINYL ALUMINIUM TRIM ANGLES TO SECURE SIGN FACE

### LETTERS


FABRICATED ALUMINIUM, RETURNS PAINTED WHITE CORIAN SIGN FACES WITH BLUE DAY/NIGHT VINYL ALL INTERNAL SIGN FACES PAINTED WHITE LOGO AND LETTERS FIXED DIRECTLY TO BUILDING FAÇADE, INTERNALLY ILLUMINATED THROUGH FACES, SIGN TO ILLUMINATE WHITE AT NIGHT.

LED DRIVERS MUST BE INSTALLED IN AN AGREED-UPON ACCESSIBLE AREA.

EXISTING SIGN TO BE REMOVED.



SIGN DETAIL  
SCALE 1:200

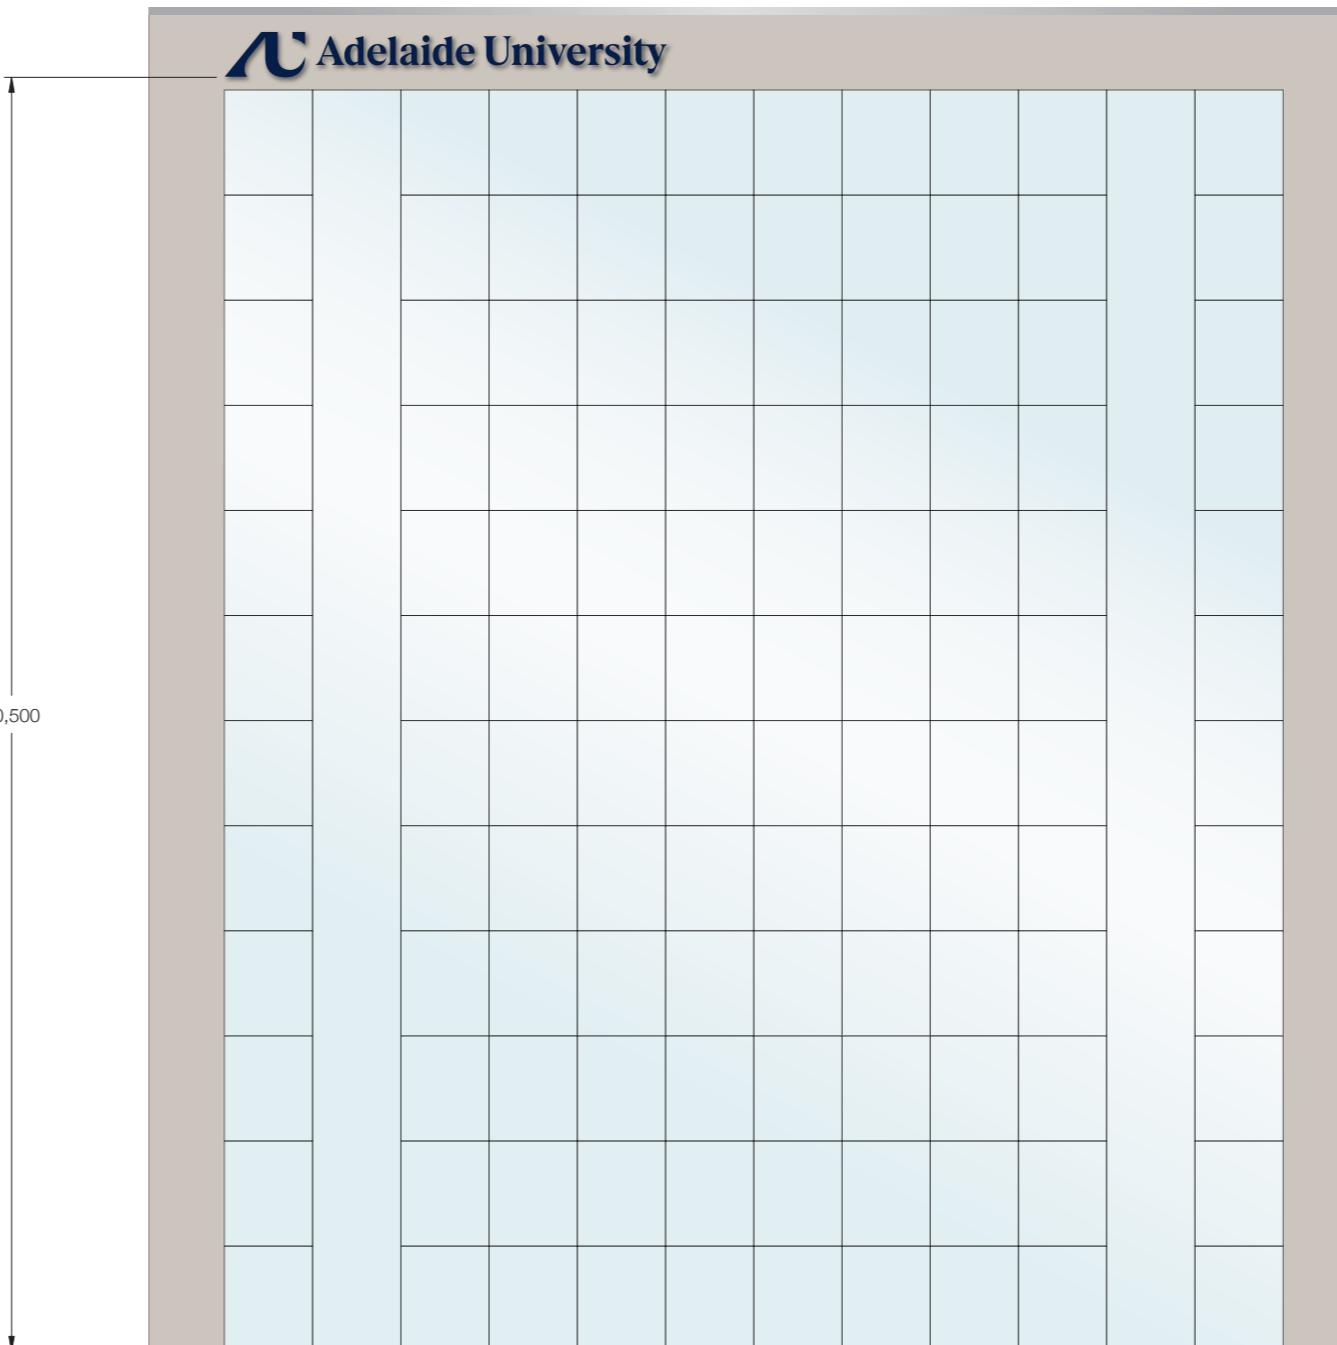

SOUTH ELEVATION  
SCALE 1:250

Issue Issue date  
ISSUE 05 27 MARCH 2025

Drawing no Scale  
- @A3

PM Drawn Checked  
RL CO CR/RL/NOW

Revision  
- - -

## Not for construction

General note: These drawings are prepared to communicate design intent only. All message content is indicative. All structural frames, footings and connections to be as per engineer's specifications and requirements. Contractor to ensure all materials, measurements, fixing details and methods are suitable for the site application before manufacture.

Client  
ADELAIDE UNIVERSITY

Project  
CITY WEST CAMPUS

Document file name  
26304-DOC\_CITY\_EAST\_SKY\_SIGNS-05

**diadem**

Australia

1300 613 934

New Zealand

+64 9 377 3736

Hong Kong

+61 3 9670 6767


info@diadem.co

diadem.co

©Copyright Diadem Pty Ltd  
Reproductions of the whole or part of this document constitutes an infringement of copyright. The information, ideas and concepts contained in this document are the intellectual property of the recipient(s). The recipient(s) of this document is prohibited from disclosing such information to any person without the prior written consent of Diadem. Figured dimensions shall take precedence to scaled.

Adelaide SA 5000

**High level sign – panoramic format**  
Wall mounted  
Single sided  
Illuminated

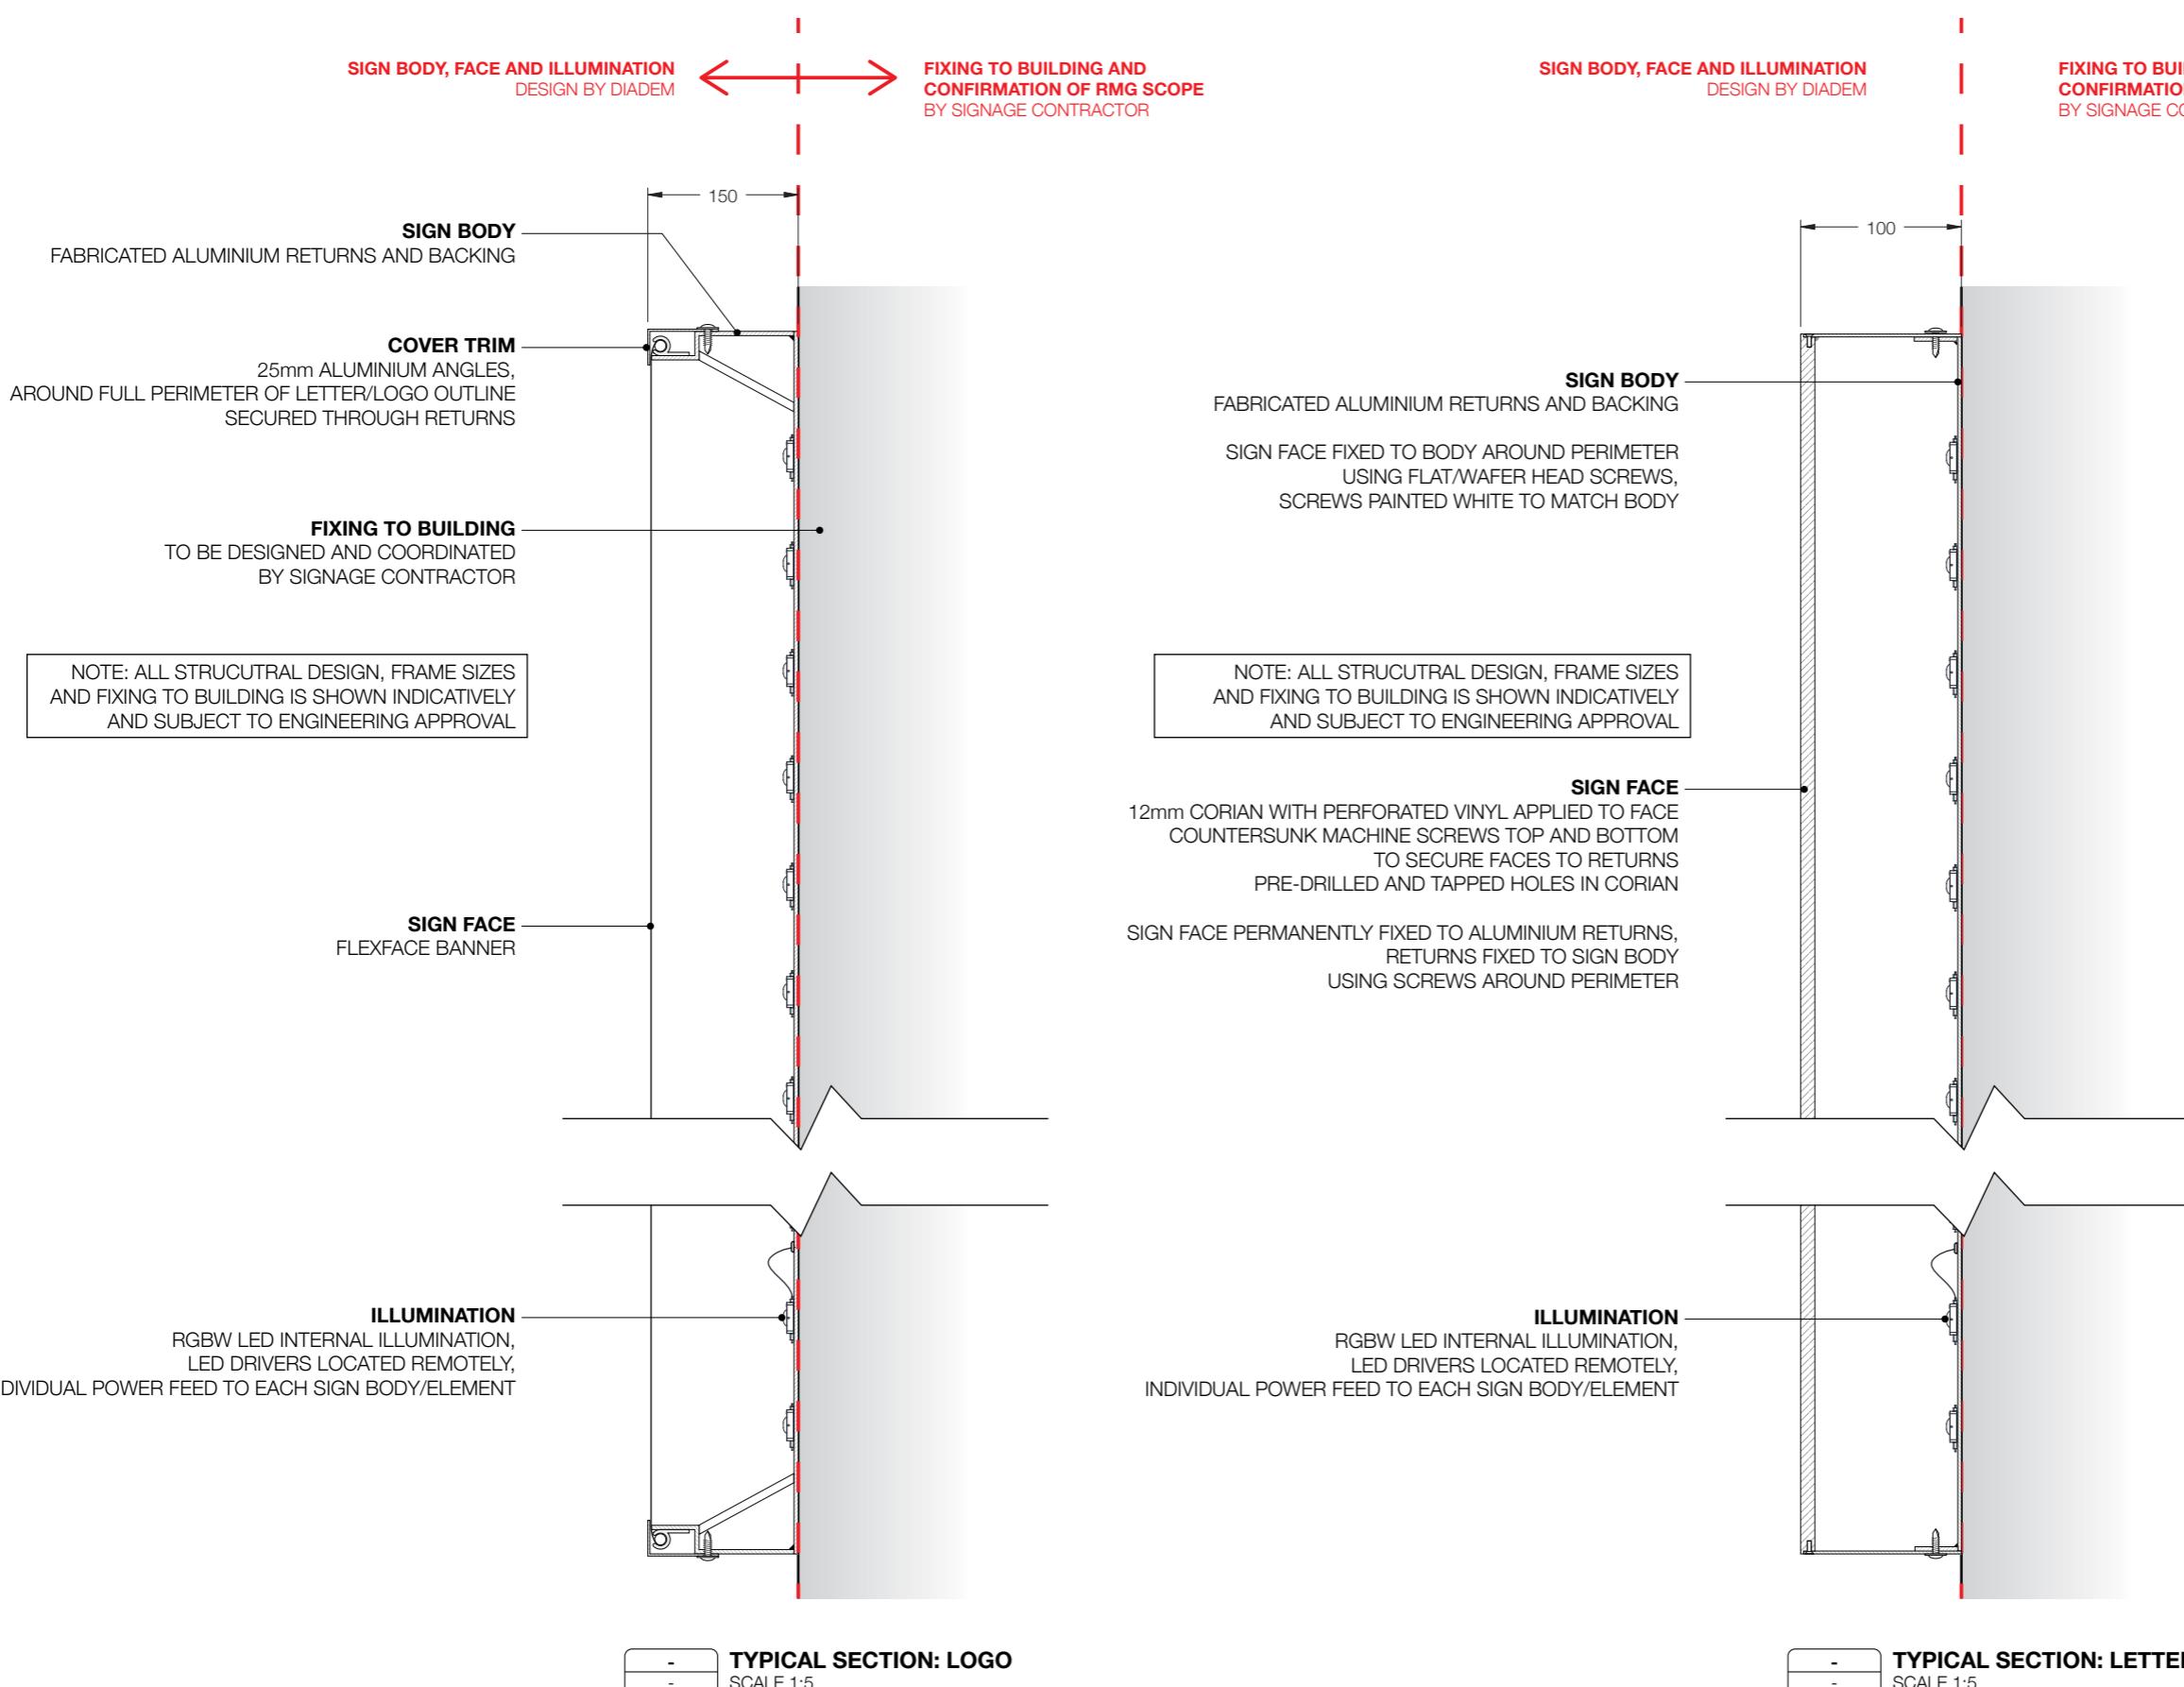

Issue Issue date  
ISSUE 05 27 MARCH 2025

Drawing no Scale  
- @A3

PM Drawn Checked  
RL CO CR/RL/NOW

Revision  
- - -

#### Not for construction

General note: These drawings are prepared to communicate design intent only. All message content is indicative. All structural frames, footings and connections to be as per engineer's specifications and requirements. Contractor to ensure all materials, measurements, fixing details and methods are suitable for the site application before manufacture.

Client  
ADELAIDE UNIVERSITY

Project  
CITY WEST CAMPUS

Document file name  
26304-DOC\_CITY\_EAST\_SKY\_SIGNS-05

**diadem**

Australia  
1300 613 934  
New Zealand  
+64 9 377 3736  
Hong Kong  
+61 3 9670 6767  
info@diadem.co  
diadem.co

©Copyright Diadem Pty Ltd  
Reproductions of the whole or part of this document constitutes an infringement of copyright. The information, ideas and concepts contained in this document are the intellectual property of the recipient(s) of this document. It is prohibited from disclosing such information to any person without the prior written consent of Diadem. Figured dimensions shall take precedence to scaled.

## Location 9

**Nexus10 Tower**

10 Pulteney Street  
Adelaide SA 5000

**High level sign – panoramic format**  
Wall mounted  
Single sided  
Illuminated

EXISTING CONDITIONS



PROPOSED LOCATION



SIGN LOCATION

SCALE 1:2000



### LOCATION SPECIFIC INFORMATION

#### LOGO

FABRICATED ALUMINIUM, RETURNS PAINTED WHITE FLEXFACE SIGN FACES WITH BLUE DAY/NIGHT VINYL ALUMINIUM TRIM ANGLES TO SECURE SIGN FACE

#### LETTERS

FABRICATED ALUMINIUM, RETURNS PAINTED WHITE CORIAN SIGN FACES WITH BLUE DAY/NIGHT VINYL ALL INTERNAL SIGN FACES PAINTED WHITE LOGO AND LETTERS FIXED DIRECTLY TO BUILDING FAÇADE, INTERNALLY ILLUMINATED THROUGH FACES, SIGN TO ILLUMINATE WHITE AT NIGHT.

LED DRIVERS MUST BE INSTALLED IN AN AGREED-UPON ACCESSIBLE AREA AND, IF APPROPRIATE, THE REUSE OF THE EXISTING 240V SUPPLY FROM THE EXISTING SIGNS IS PREFERRED.

EXISTING SIGN TO BE REMOVED.



Issue Issue date  
ISSUE 05 27 MARCH 2025

Drawing no Scale  
- @A3

PM Drawn Checked  
RL CO CR/RL/NOW

Revision  
- - -

### Not for construction

General note: These drawings are prepared to communicate design intent only. All message content is indicative. All structural frames, footings and connections to be as per engineer's specifications and requirements. Contractor to ensure all materials, measurements, fixing details and methods are suitable for the site application before manufacture.

Client  
ADELAIDE UNIVERSITY

Project  
CITY WEST CAMPUS

Document file name  
26304-DOC\_CITY\_EAST\_SKY\_SIGNS-05

**diadem**

Australia  
1300 613 934

New Zealand  
+64 9 377 3736

Hong Kong  
+61 3 9670 6767

info@diadem.co  
diadem.co

©Copyright Diadem Pty Ltd  
Reproductions of the whole or part of this document constitutes an infringement of copyright. The information, ideas and concepts contained in this document are the intellectual property of Diadem. The recipient(s) of this document is prohibited from disclosing such information to any person without the prior written consent of Diadem. Figured dimensions shall take precedence to scaled.

# Nexus10 Tower

10 Pulteney Street  
Adelaide SA 5000

## Location 9

**High level sign – panoramic format**  
Wall mounted  
Single sided  
Illuminated

Drawing title

**Section detail**

Issue Issue date  
ISSUE 05 27 MARCH 2025

Drawing no Scale  
- @A3

PM Drawn Checked  
RL CO CR/RL/NOW

Revision  
- - -

### Not for construction

General note: These drawings are prepared to communicate design intent only. All message content is indicative. All structural frames, footings and connections to be as per engineer's specifications and requirements. Contractor to ensure all materials, measurements, fixing details and methods are suitable for the site application before manufacture.

Client  
ADELAIDE UNIVERSITY


Project  
CITY WEST CAMPUS

Document file name  
26304-DOC\_CITY\_EAST\_SKY\_SIGNS-05

**diadem**

Australia  
1300 613 934  
New Zealand  
+64 9 377 3736  
Hong Kong  
+61 3 9670 6767  
info@diadem.co  
diadem.co

©Copyright Diadem Pty Ltd  
Reproductions of the whole or part of this document constitutes an infringement of copyright. The information, ideas and concepts contained in this document are the intellectual property of the recipient(s) of this document. It is prohibited from disclosing such information to any person without the prior written consent of Diadem. Figured dimensions shall take precedence to scaled.

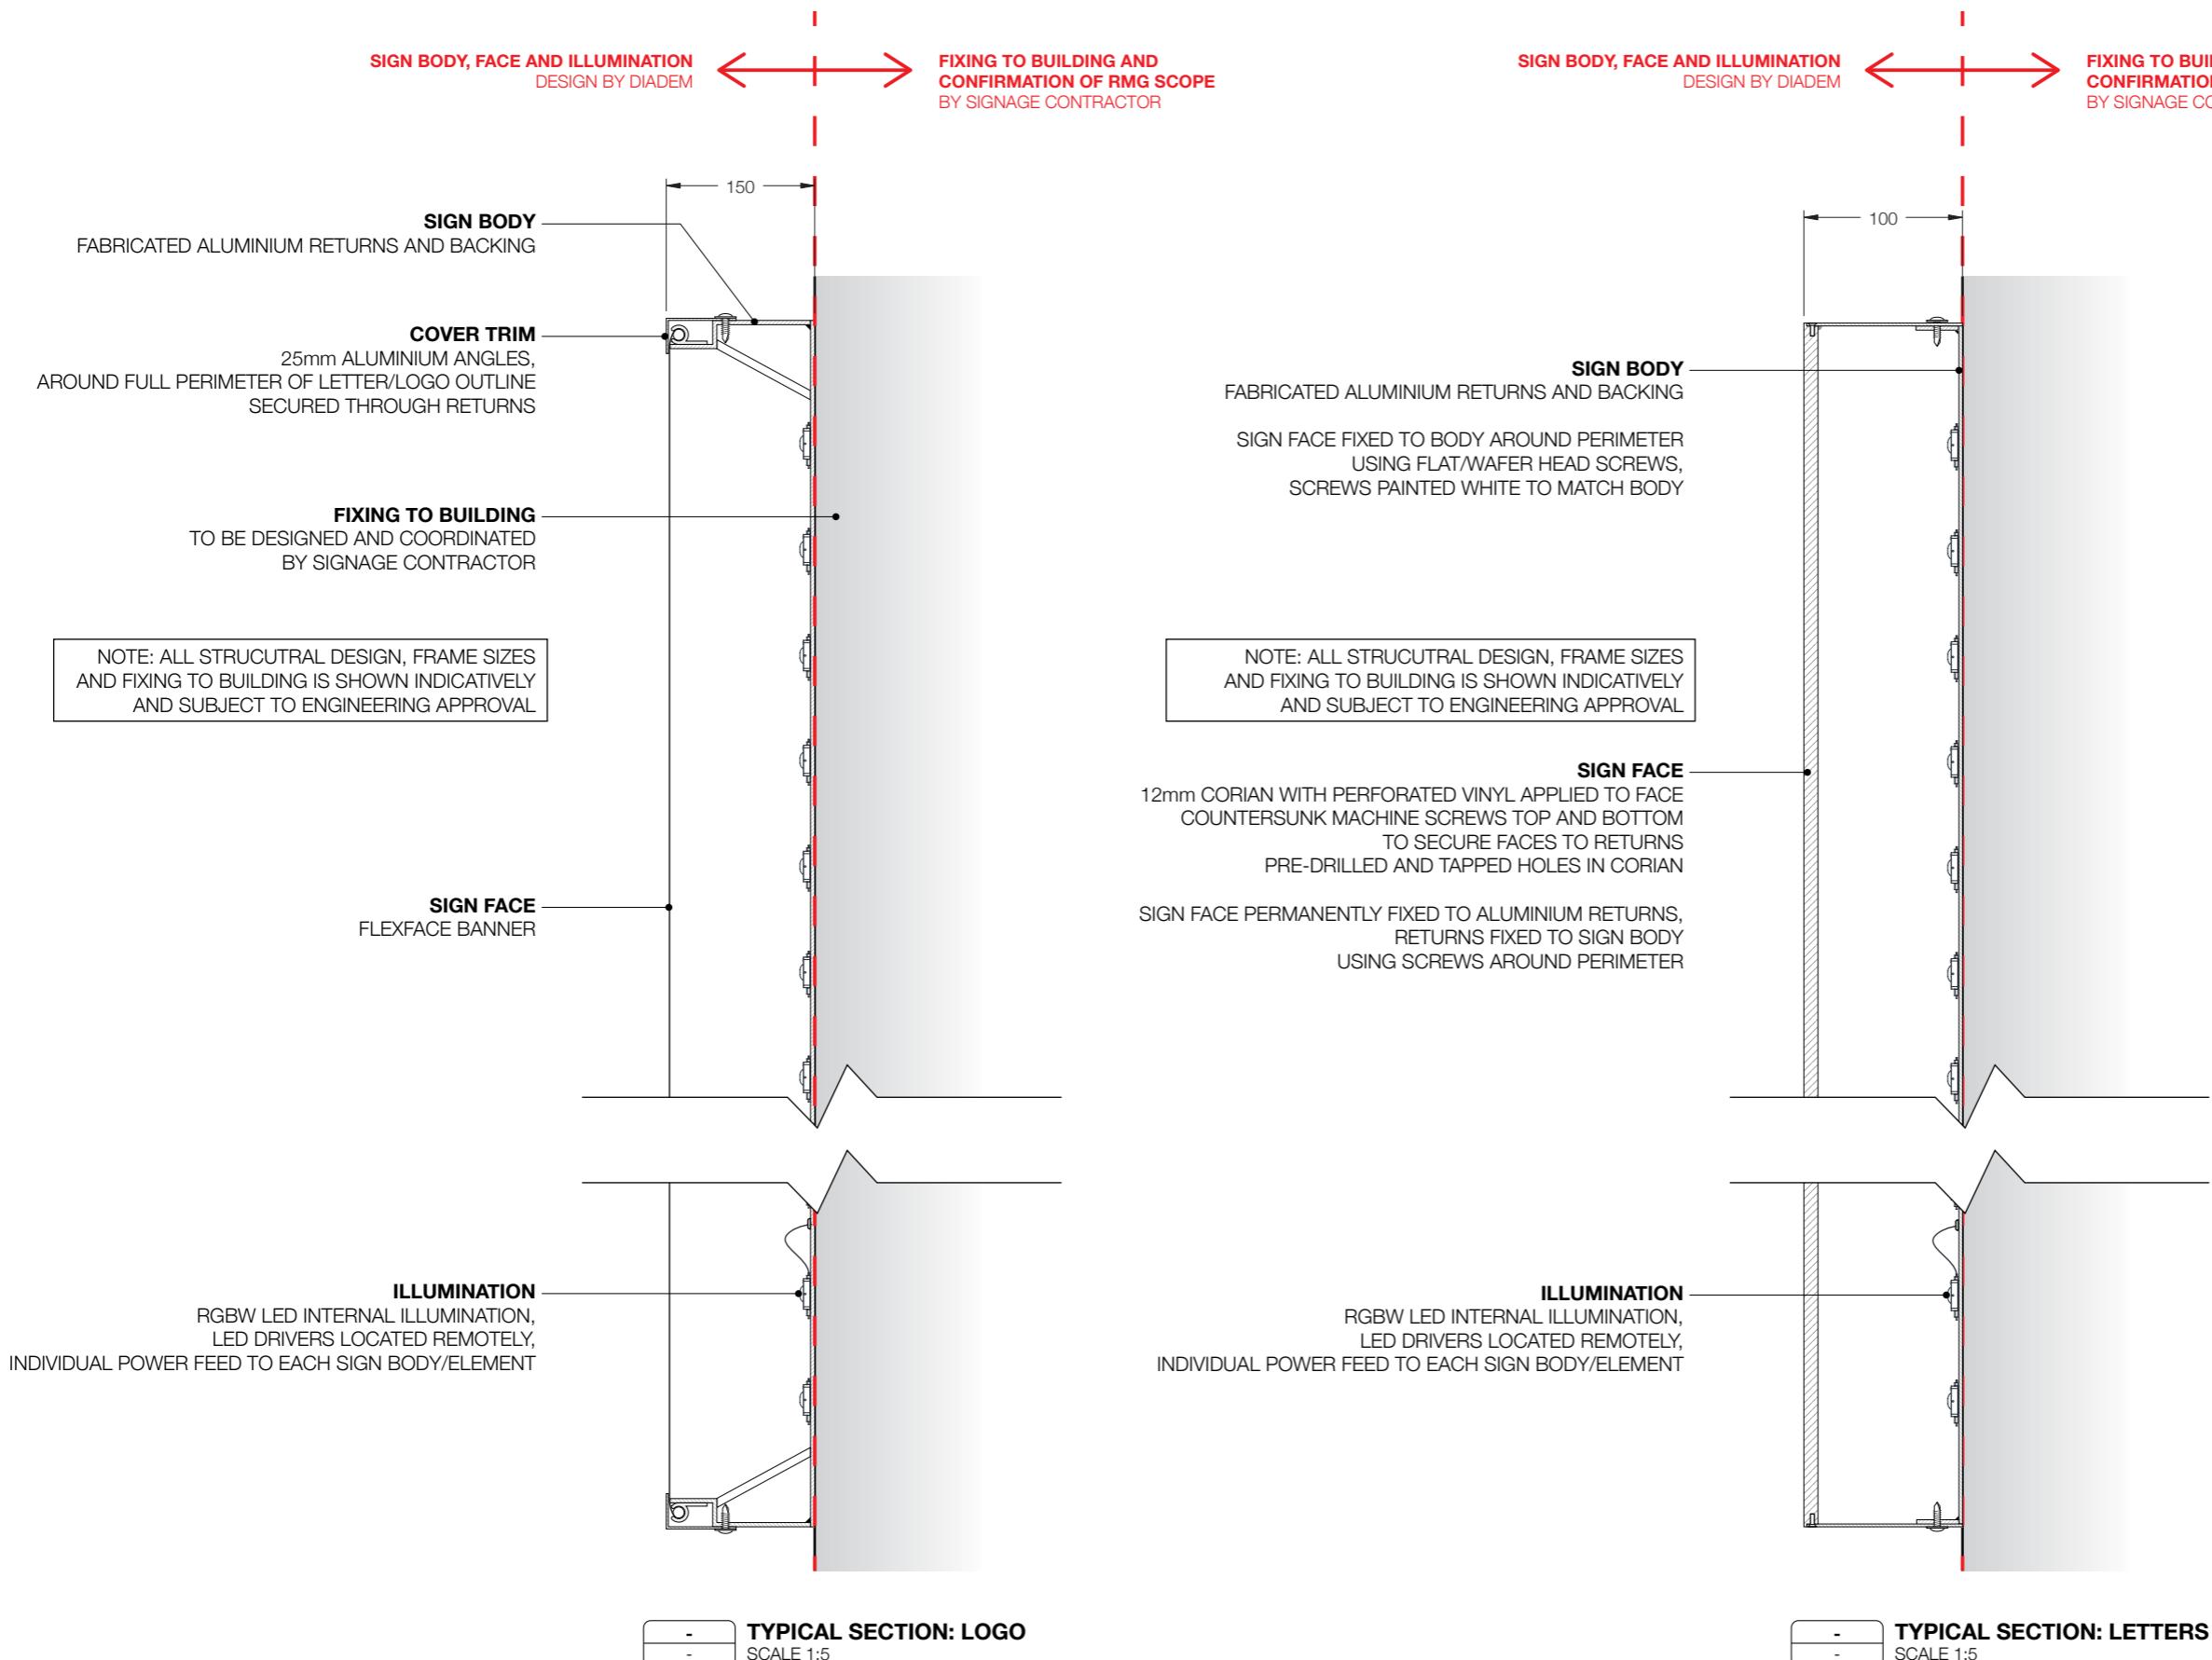

## Nexus10 Tower

10 Pulteney Street  
Adelaide SA 5000

## Location 9

High level sign –  
panoramic format  
Wall mounted  
Single sided  
Illuminated

Drawing title \_\_\_\_\_

### Removal scope



EXISTING CONDITIONS

**RMG:** REMOVE EXISTING SIGN AND MAKE GOOD TO FAÇADE INCLUDING BUT NOT LIMITED TO, WATERPROOFING, PATCHING AND COLOUR MATCHING EXISTING REMOVAL POINTS TO REFLECT CURRENT BUILDING COLOUR AND CONDITIONS. CLEAN AND MAKE GOOD EXTENT OF EXISTING SIGN FOOTPRINT.  
**ACCESS:** CRANE OR ROPE ACCESS FROM ROOF TO BE DETERMINED ON SITE BY CONTRACTOR WITH FACILITIES TEAM. CONTRACTOR TO ALLOW FOR ALL RELEVANT AUTHORITY AND TRAFFIC MANAGEMENT REQUIREMENTS FOR INSTALLATION  
**NOTE:** REFER TO A.U. PROVIDED DOCUMENTATION FOR FURTHER INFORMATION.

Issue      Issue date  
ISSUE 05    27 MARCH 2025

Drawing no      Scale  
-                 @A3

PM      Drawn      Checked  
RL      CO          CR/RL/NOW

Revision \_\_\_\_\_  
- - -

### Not for construction

General note: These drawings are prepared to communicate design intent only. All message content is indicative. All structural frames, footings and connections to be as per engineer's specifications and requirements. Contractor to ensure all materials, measurements, fixing details and methods are suitable for the site application before manufacture.

Client  
ADELAIDE UNIVERSITY

Project  
CITY WEST CAMPUS

Document file name  
26304-DOC\_CITY\_EAST\_SKY\_SIGNS-05

**diadem**

Australia  
1300 613 934

New Zealand  
+64 9 377 3736

Hong Kong  
+61 3 9670 6767  
info@diadem.co  
diadem.co

©Copyright Diadem Pty Ltd  
Reproductions of the whole or part of this document constitutes an infringement of copyright. The information, ideas and concepts contained in this document are the copyright of Diadem Pty Ltd. The recipient(s) of this document is prohibited from disclosing such information to any person without the prior written consent of Diadem. Figured dimensions shall take precedence to scaled.



EXISTING CONDITIONS



PROPOSED LOCATION



SIGN LOCATION  
SCALE 1:2000



#### LOCATION SPECIFIC INFORMATION

##### LOGO

FABRICATED ALUMINIUM, RETURNS PAINTED WHITE FLEXFACE SIGN FACES WITH BLUE DAY/NIGHT VINYL ALUMINIUM TRIM ANGLES TO SECURE SIGN FACE

##### LETTERS

FABRICATED ALUMINIUM, RETURNS PAINTED WHITE CORIAN SIGN FACES WITH BLUE DAY/NIGHT VINYL ALL INTERNAL SIGN FACES PAINTED WHITE LOGO AND LETTERS FIXED DIRECTLY TO BUILDING FAÇADE, INTERNALLY ILLUMINATED THROUGH FACES, SIGN TO ILLUMINATE WHITE AT NIGHT.

LED DRIVERS MUST BE INSTALLED IN AN AGREED-UPON ACCESSIBLE AREA AND, IF APPROPRIATE, THE REUSE OF THE EXISTING 240V SUPPLY FROM THE EXISTING SIGNS IS PREFERRED.

EXISTING SIGN TO BE REMOVED.

## Nexus10 Tower


10 Pulteney Street  
Adelaide SA 5000

## Location 11

High level sign – panoramic format  
Wall mounted  
Single sided  
Illuminated

Drawing title

General arrangement

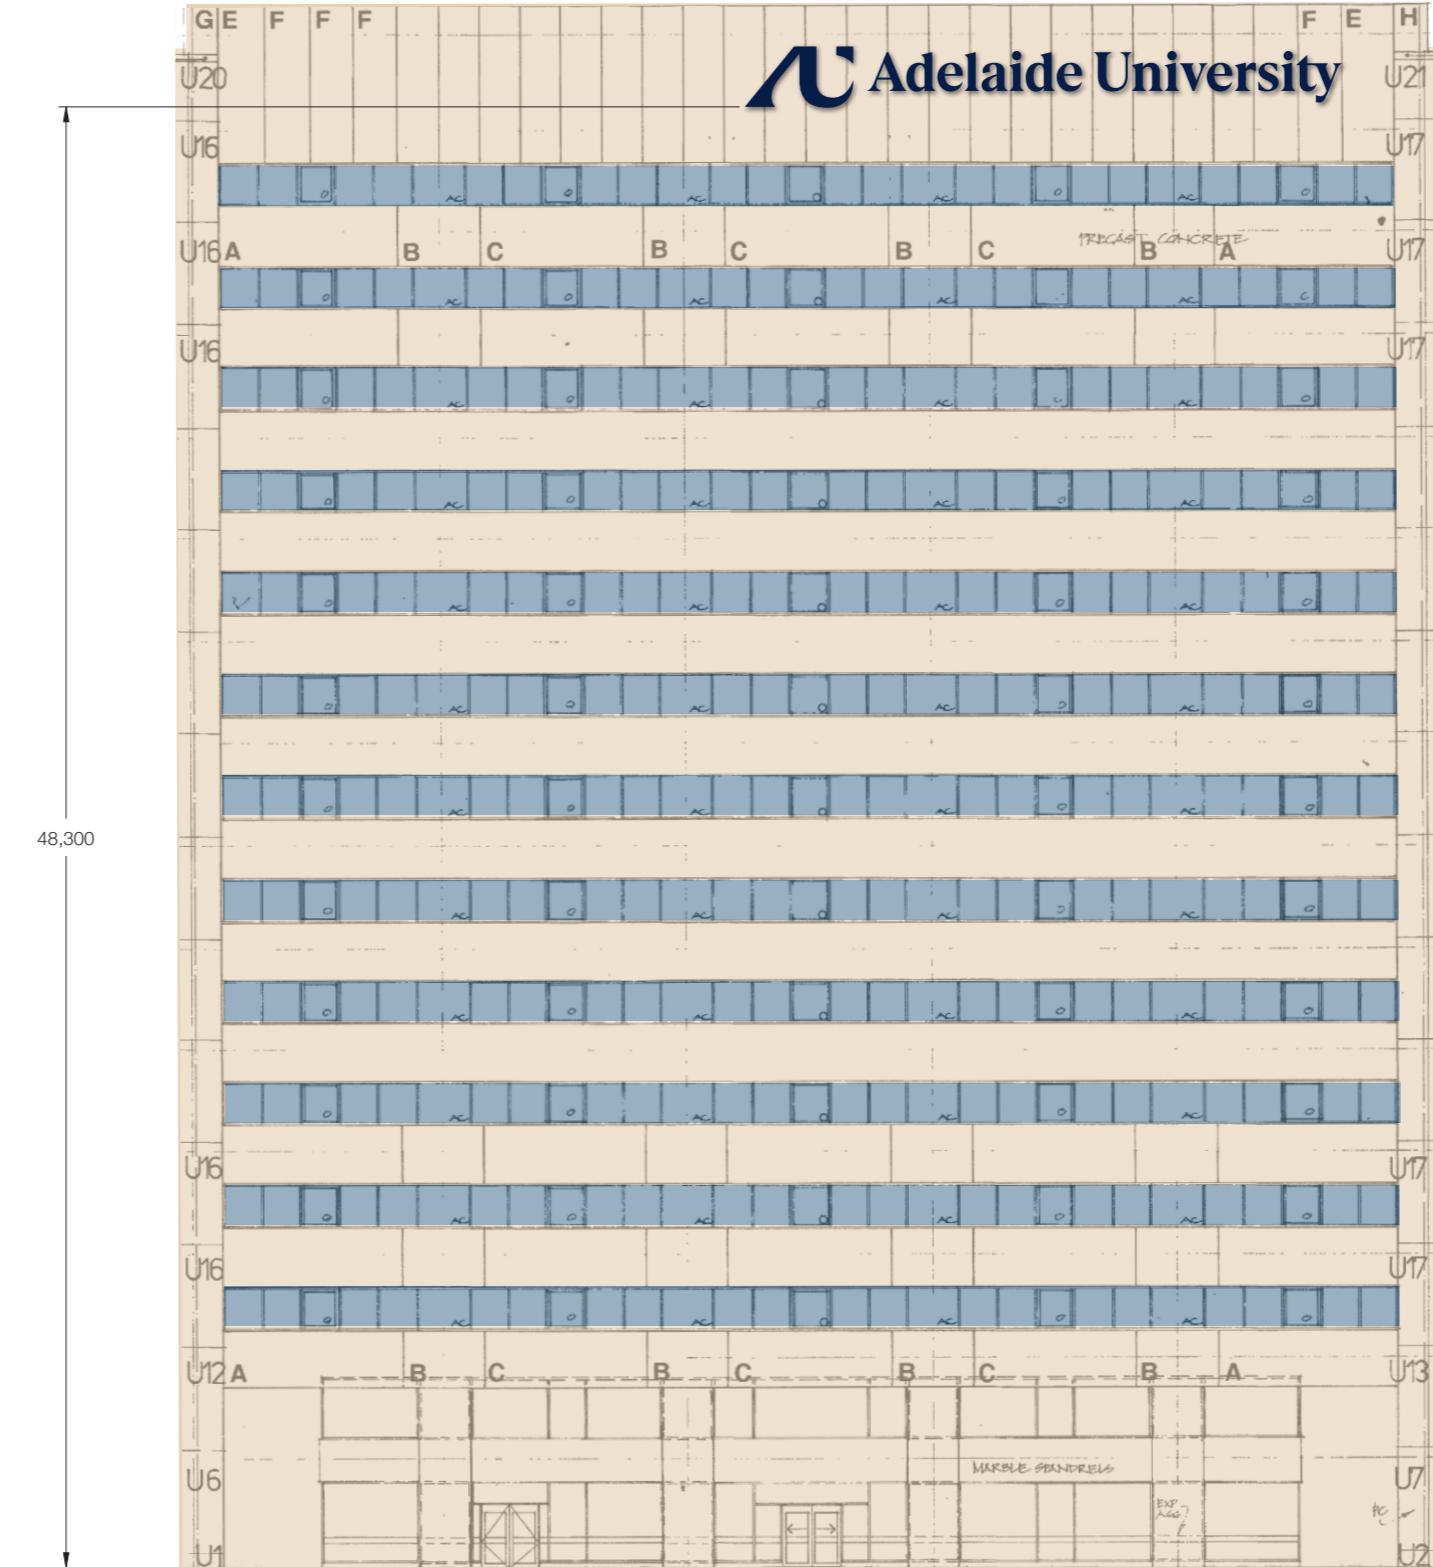

# Nexus10 Tower

10 Pulteney Street  
Adelaide SA 5000

## Location 11

**High level sign – panoramic format**  
Wall mounted  
Single sided  
Illuminated

Drawing title

**Section detail**

Issue Issue date  
ISSUE 05 27 MARCH 2025

Drawing no Scale  
- @A3

PM Drawn Checked  
RL CO CR/RL/NOW

Revision  
- - -

### Not for construction

General note: These drawings are prepared to communicate design intent only. All message content is indicative. All structural frames, footings and connections to be as per engineer's specifications and requirements. Contractor to ensure all materials, measurements, fixing details and methods are suitable for the site application before manufacture.

Client  
ADELAIDE UNIVERSITY

Project  
CITY WEST CAMPUS

Document file name  
26304-DOC\_CITY\_EAST\_SKY\_SIGNS-05

**diadem**


Australia  
1300 613 934

New Zealand  
+64 9 377 3736

Hong Kong  
+61 3 9670 6767

info@diadem.co  
diadem.co

©Copyright Diadem Pty Ltd  
Reproductions of the whole or part of this document constitutes an infringement of copyright. The information, ideas and concepts contained in this document are the intellectual property of the recipient(s) of this document. It is prohibited from disclosing such information to any person without the prior written consent of Diadem. Figured dimensions shall take precedence to scaled.

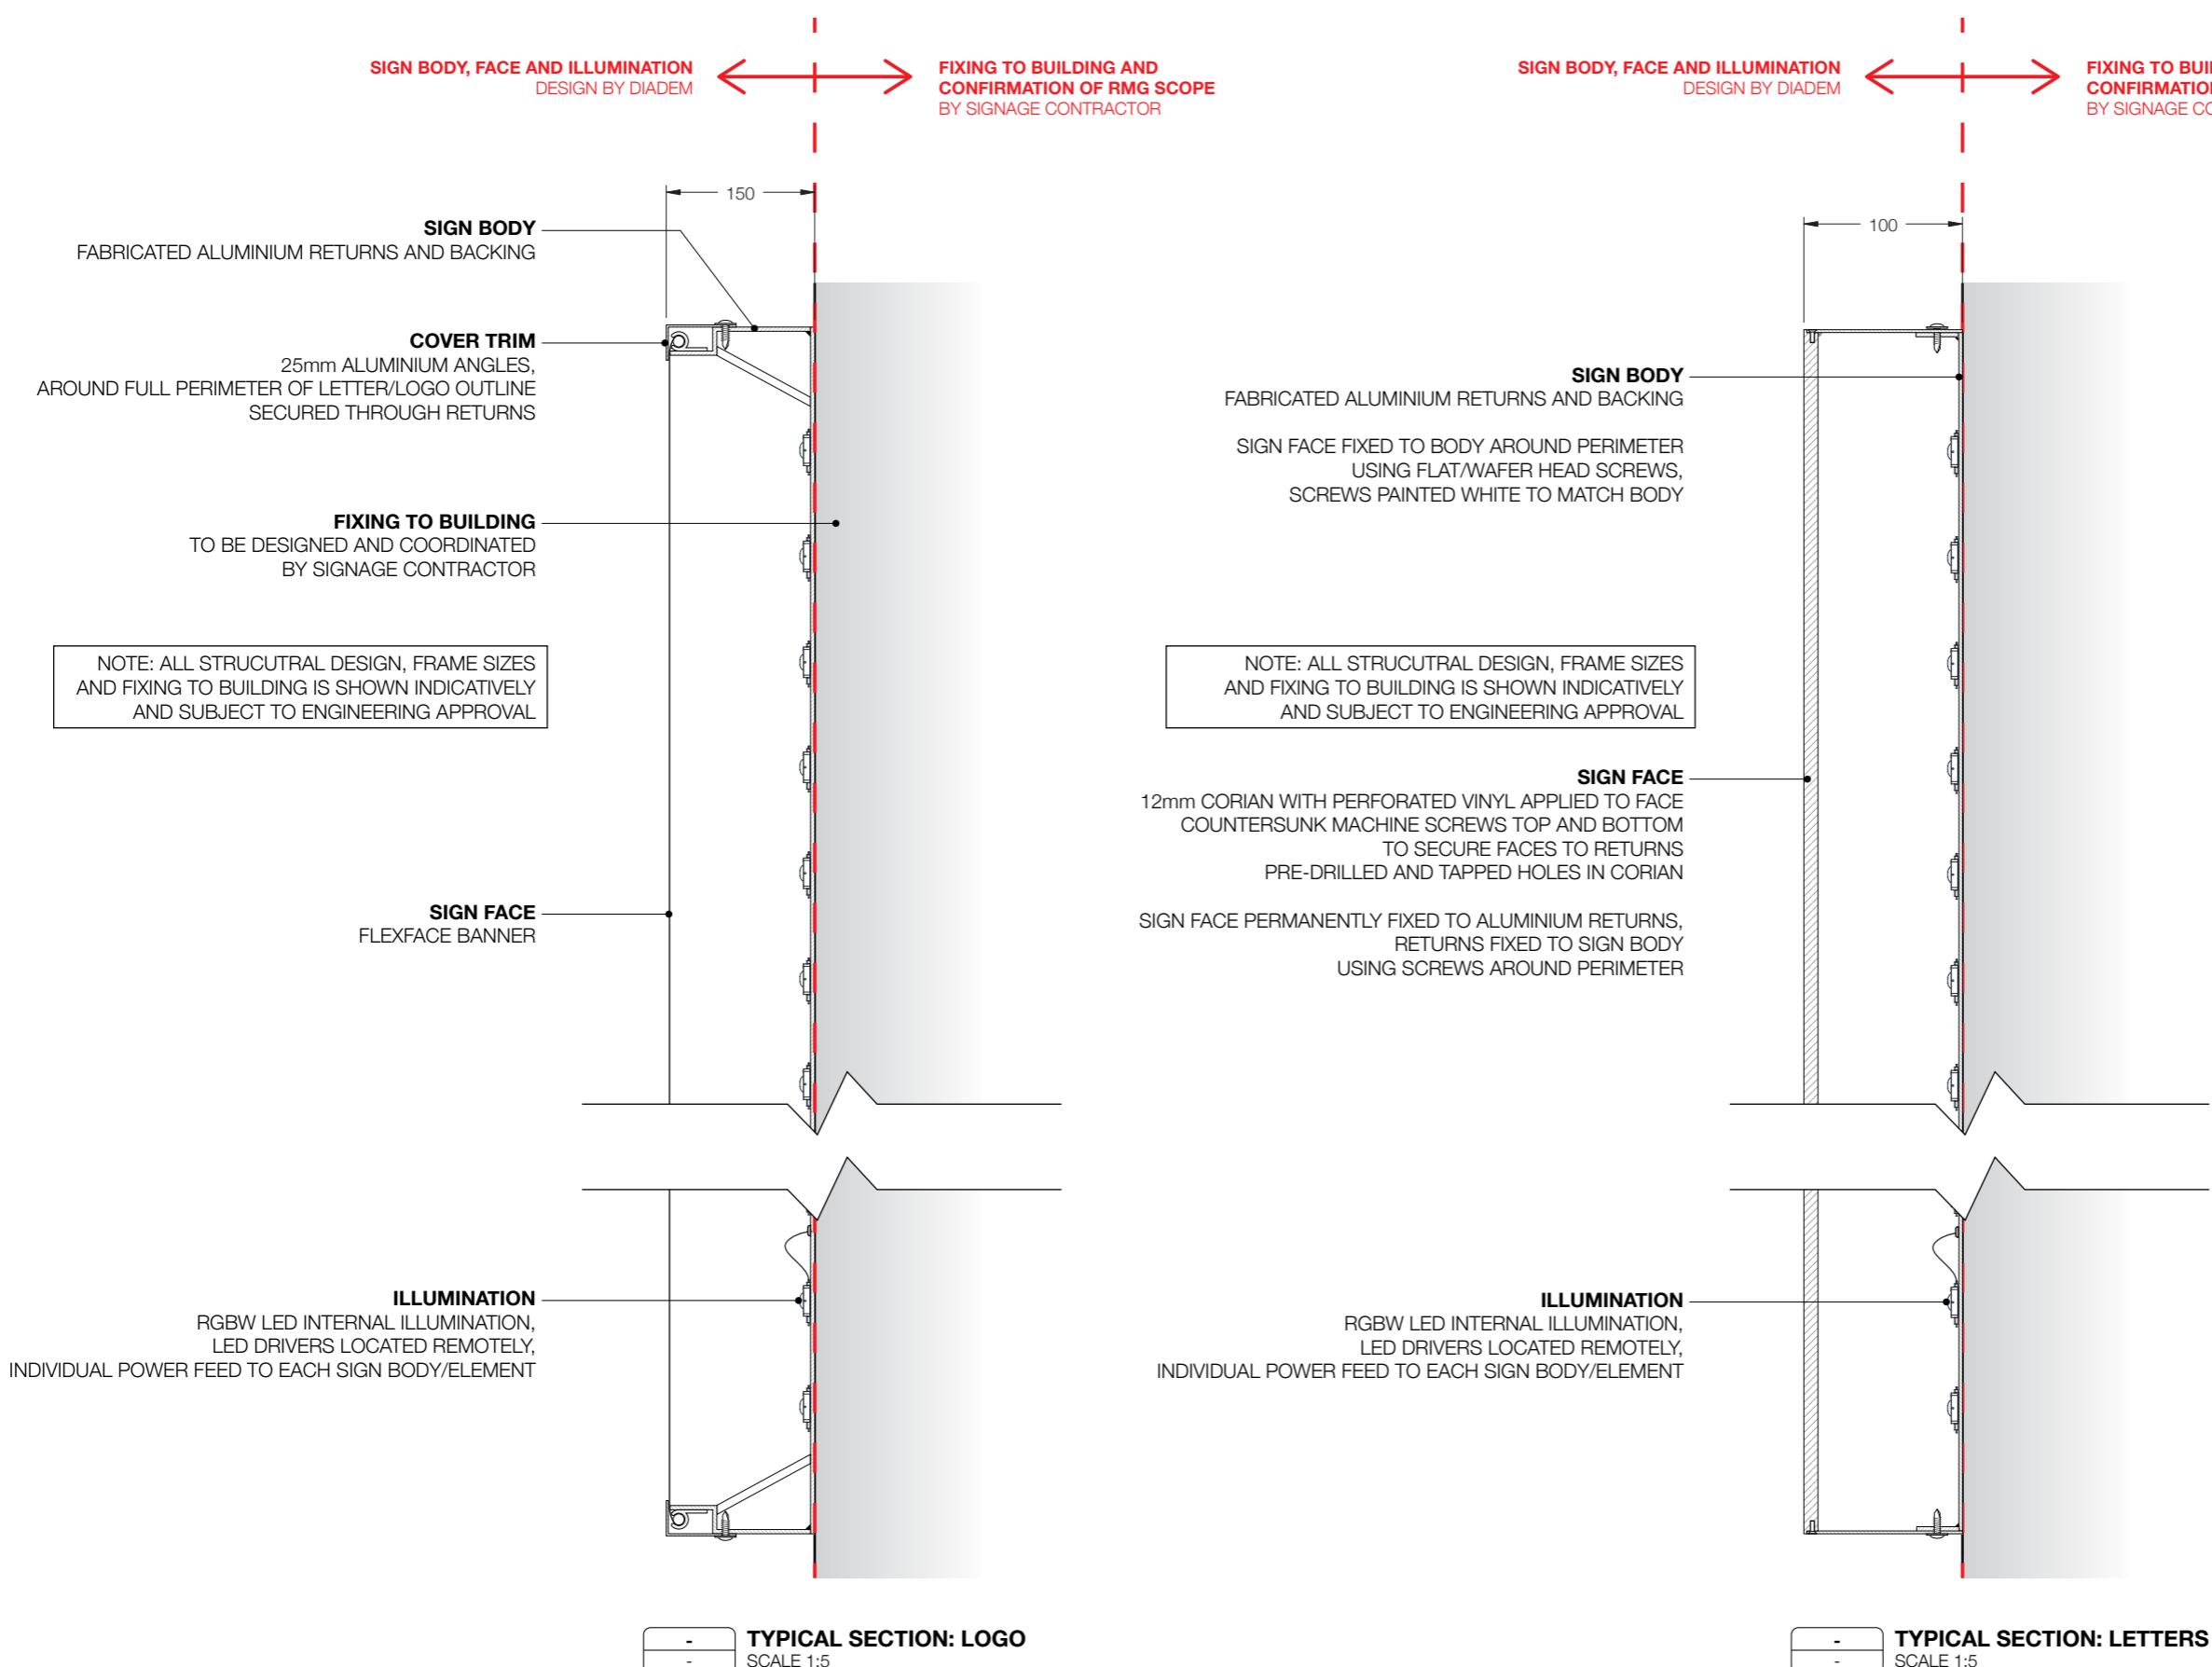

## Nexus10 Tower

10 Pulteney Street  
Adelaide SA 5000

## Location 9

High level sign –  
panoramic format  
Wall mounted  
Single sided  
Illuminated

Drawing title \_\_\_\_\_

### Removal scope



EXISTING CONDITIONS

**RMG:** REMOVE EXISTING SIGN AND MAKE GOOD TO FAÇADE INCLUDING BUT NOT LIMITED TO, WATERPROOFING, PATCHING AND COLOUR MATCHING EXISTING REMOVAL POINTS TO REFLECT CURRENT BUILDING COLOUR AND CONDITIONS. CLEAN AND MAKE GOOD EXTENT OF EXISTING SIGN FOOTPRINT.  
**ACCESS:** CRANE OR ROPE ACCESS FROM ROOF TO BE DETERMINED ON SITE BY CONTRACTOR WITH FACILITIES TEAM. CONTRACTOR TO ALLOW FOR ALL RELEVANT AUTHORITY AND TRAFFIC MANAGEMENT REQUIREMENTS FOR INSTALLATION  
**NOTE:** REFER TO A.U. PROVIDED DOCUMENTATION FOR FURTHER INFORMATION.

Issue      Issue date  
ISSUE 05    27 MARCH 2025

Drawing no      Scale  
-                 @A3

PM      Drawn      Checked  
RL      CO          CR/RL/NOW

Revision  
- - -

### Not for construction

General note: These drawings are prepared to communicate design intent only. All message content is indicative. All structural frames, footings and connections to be as per engineer's specifications and requirements. Contractor to ensure all materials, measurements, fixing details and methods are suitable for the site application before manufacture.

Client  
ADELAIDE UNIVERSITY

Project  
CITY WEST CAMPUS

Document file name  
26304-DOC\_CITY\_EAST\_SKY\_SIGNS-05

**diadem**

Australia  
1300 613 934

New Zealand  
+64 9 377 3736

Hong Kong  
+61 3 9670 6767  
info@diadem.co  
diadem.co

©Copyright Diadem Pty Ltd  
Reproductions of the whole or part of this document constitutes an infringement of copyright. The information, ideas and concepts contained in this document are the copyright of Diadem. The recipient(s) of this document is prohibited from disclosing such information to any person without the prior written consent of Diadem. Figured dimensions shall take precedence to scaled.

