

Change register

Council Documentation

			PM	Drawn	Checked
Issue 01	6 February 2025	First issue	RL	CO	CR/RL/TD
Issue 02	19 February 2025	Updates based on client feedback: Location 12 added, RMG scope updated	RL	CO	CR/RL
Issue 03	14 March 2025	Updates throughout pack	RL	CO	CR/RL/NCW
Issue 04	03 April 2025	General updates	RL	CO	CR/RL/NCW

Endorsed by	Name	Signed	Date	Issue No.

diadem

Australia
1300 613 934

New Zealand
+64 9 377 3736

Hong Kong
+613 9670 6767
info@diadem.co
diadem.co

General note: These drawings are prepared to communicate design intent only.
All message content is indicative. All structural frames, footings and connections to be as per
Engineer's specifications and requirements. Contractor to ensure all materials, measurements,
fixing details and methods are suitable for the site application before manufacture.

©Copyright Diadem Pty Ltd
Proprietary information. All rights reserved. All rights reserved. All rights reserved.
The information, ideas and concepts contained in this document are confidential. The recipient(s)
of this document is prohibited from disclosing such information to any person without the prior
written consent of Diadem. Figured dimensions shall take precedence to scaled.

Logo proportions



INLINE LOGO



STACKED LOGO



PANORAMIC LOGO


LOGO ALIGNMENT CRITICAL
ALL VERSIONS OF THE LOGO

Site plan: new signs – City west campus

CAMPUS BOUNDARY HIGH LEVEL SIGN LOCATION



OVERALL SITE PLAN
NOT TO SCALE

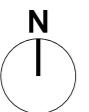


Site plan: new signs – City west campus: Jeffrey Smart Library


CAMPUS BOUNDARY HIGH LEVEL SIGN LOCATION



OVERALL SITE PLAN
NOT TO SCALE

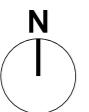

New signs

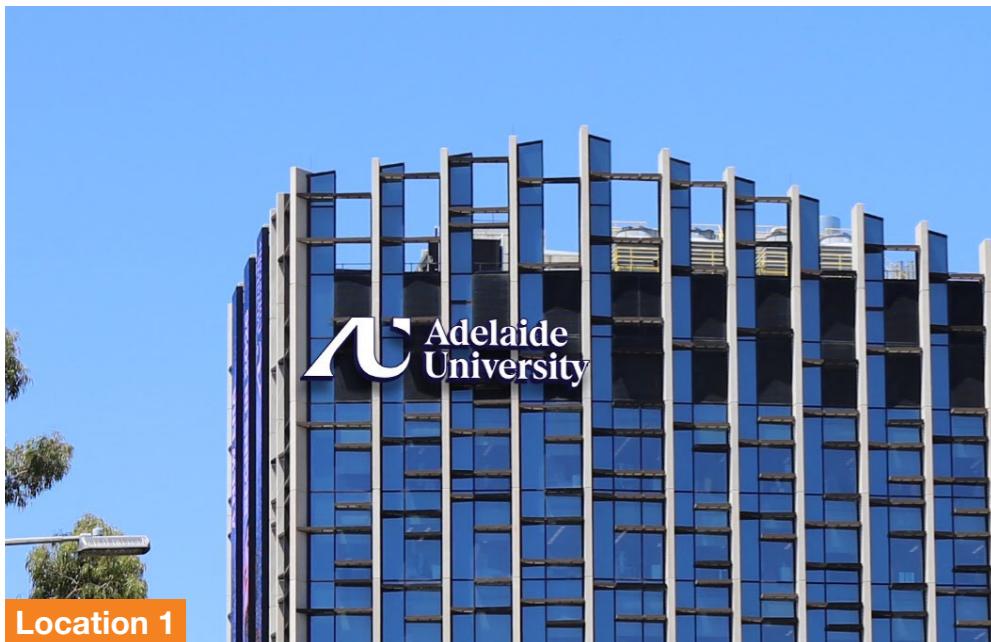

Location 1




Location 2




Location 3



Location 5

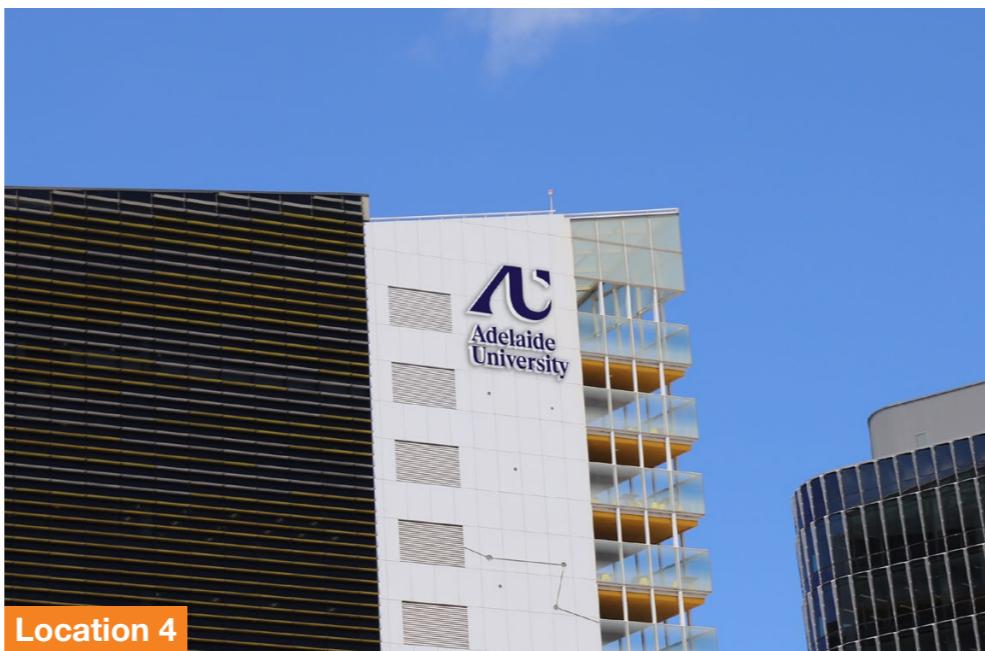



Location 4

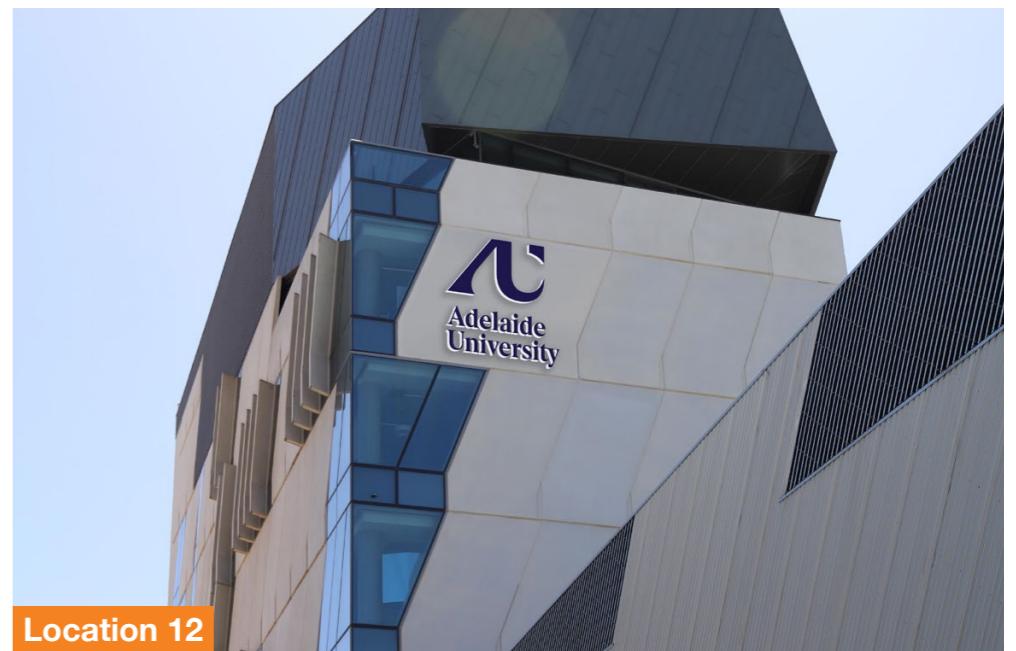

Location 12

ILLUMINATIONS

ALL SIGNS WILL ILLUMINATE WHITE AT NIGHT TIME,
REGARDLESS OF APPEARANCE DURING THE DAY.
IN ADDITION, ALL SIGNS WILL BE FITTED WITH RGBW LEDs,
TO ALLOW THE ABILITY TO ILLUMINATE IN MULTIPLE COLOURS.

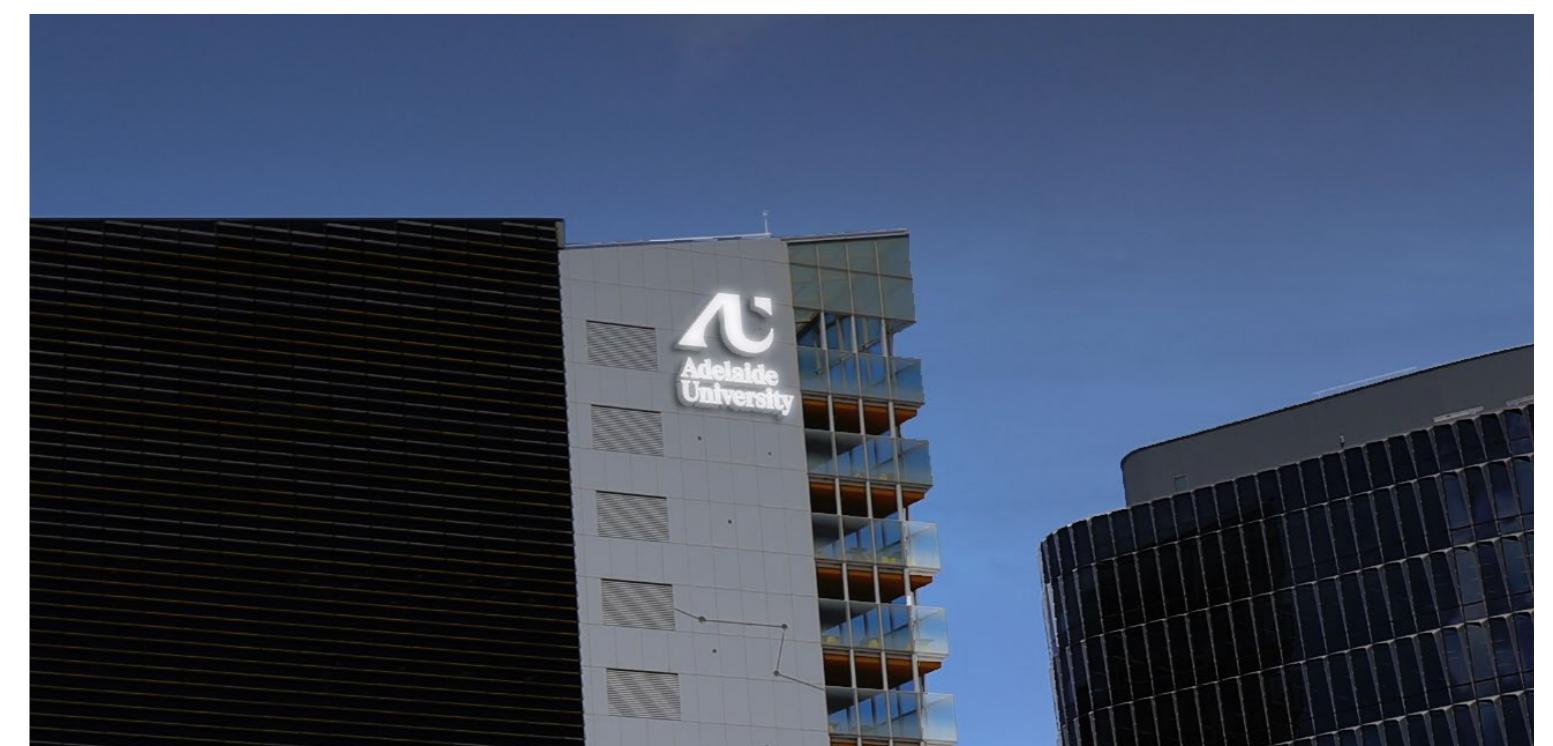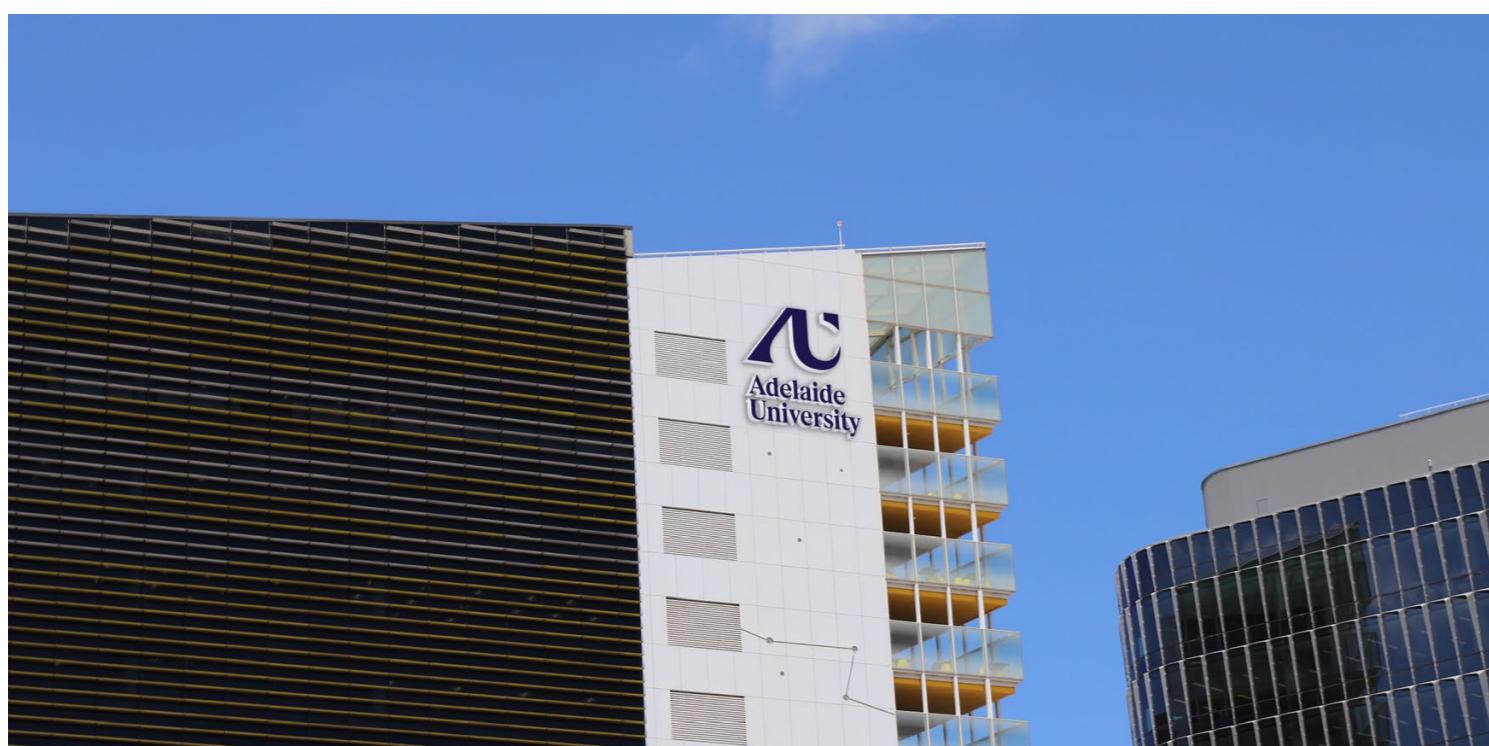


Site plan: removed signs – City west campus

CAMPUS BOUNDARY ----- HIGH LEVEL SIGN LOCATION ■



OVERALL SITE PLAN
NOT TO SCALE

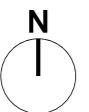

INSTRUCTIONS

REMOVE EXISTING SIGN AND MAKE GOOD TO REMOVE LOCATION.

MAKE GOOD INCLUDES THE FOLLOWING WHERE APPLICABLE:

- EXISTING CLADDING REMOVED
- NEW CLADDING INSTALLED TO MATCH EXISTING
- REPAINT SURROUNDING WALL AREAS
- ANY IMPACTED SUBSTRATES FROM REMOVAL PROCESS

TO BE REINSTATED TO EXISTING CONDITIONS

RMG2**Removal scope**

Existing signage






EXISTING CONDITIONS



PROPOSED LOCATION

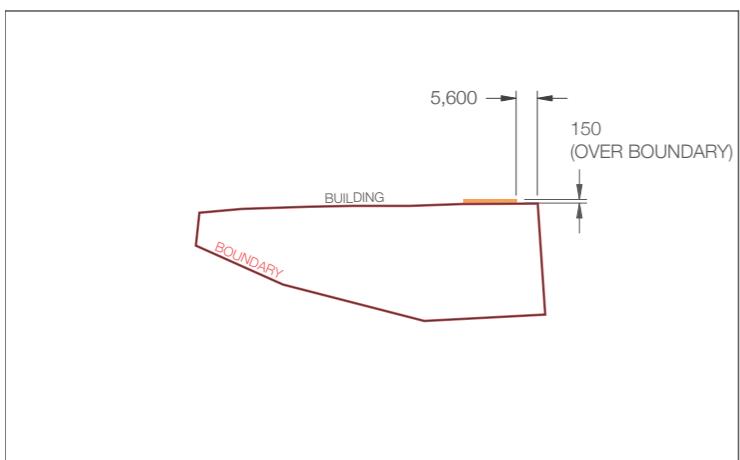

SIGN LOCATION

SCALE 1:2000



LOCATION SPECIFIC INFORMATION

LOGO

FABRICATED ALUMINIUM, RETURNS PAINTED DARK BLUE
WHITE FLEXFACE SIGN FACES
ALUMINIUM TRIM ANGLES TO SECURE SIGN FACE

LETTERS

FABRICATED ALUMINIUM, RETURNS PAINTED DARK BLUE
WHITE CORIAN SIGN FACES

LOGO AND LETTERS FIXED DIRECTLY TO BUILDING FACADE,
INTERNALLY ILLUMINATED THROUGH FACES,
SIGN TO ILLUMINATE WHITE AT NIGHT.

ALL INTERNAL SIGN FACES PAINTED WHITE

LED DRIVERS MUST BE INSTALLED IN AN AGREED-UPON ACCESSIBLE
AREA AND, IF APPROPRIATE, THE REUSE OF THE EXISTING 240V SUPPLY
FROM THE EXISTING SIGNS IS PREFERRED.

EXISTING SIGN TO BE REMOVED.

Bradley Building

Cnr North Terrace & Morphett Street

Adelaide SA 5000

Location 1

High level sign – inline format
Wall mounted
Single sided
Illuminated

Drawing title

General arrangement

Issue Issue date
ISSUE 04 03 APRIL 2025

Drawing no Scale
- @A3

PM Drawn Checked
RL CO CR/RL/NOW

Revision
- - -

Not for construction

General note: These drawings are prepared to communicate design intent only. All message content is indicative. All structural frames, footings and connections to be as per engineer's specifications and requirements. Contractor to ensure all materials, measurements, fixing details and methods are suitable for the site application before manufacture.

Client
ADELAIDE UNIVERSITY

Project
CITY WEST CAMPUS

Document file name
26304-DOC_CITY_WEST_SKY_SIGNS-04


diadem

Australia
1300 613 934


New Zealand
+64 9 377 3736

Hong Kong
+61 3 9670 6767
info@diadem.co
diadem.co

©Copyright Diadem Pty Ltd
Reproductions of the whole or part of this document constitutes an infringement of copyright. The information, ideas and concepts contained in this document are the intellectual property of the recipient(s) of this document. It is prohibited from disclosing such information to any person without the prior written consent of Diadem. Figured dimensions shall take precedence to scaled.

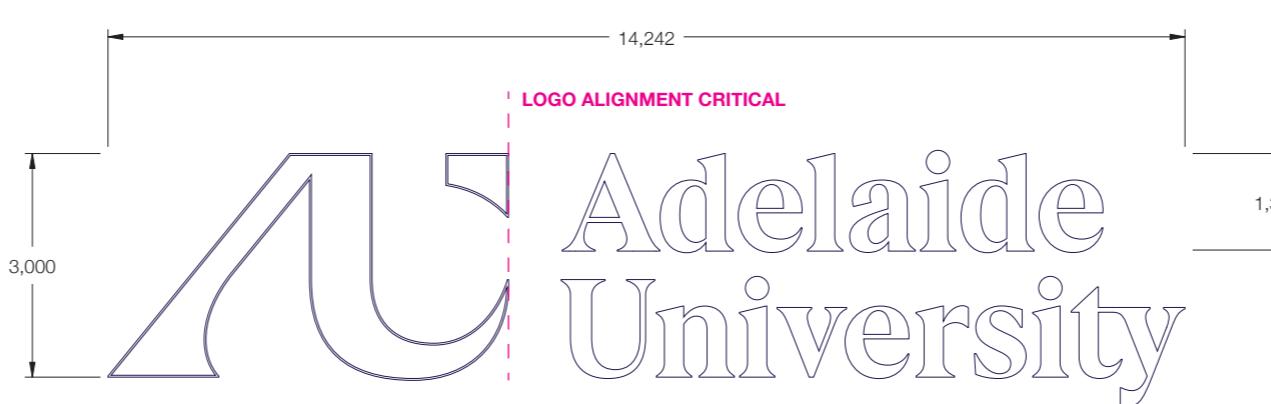

SIGN DETAIL
SCALE 1:100

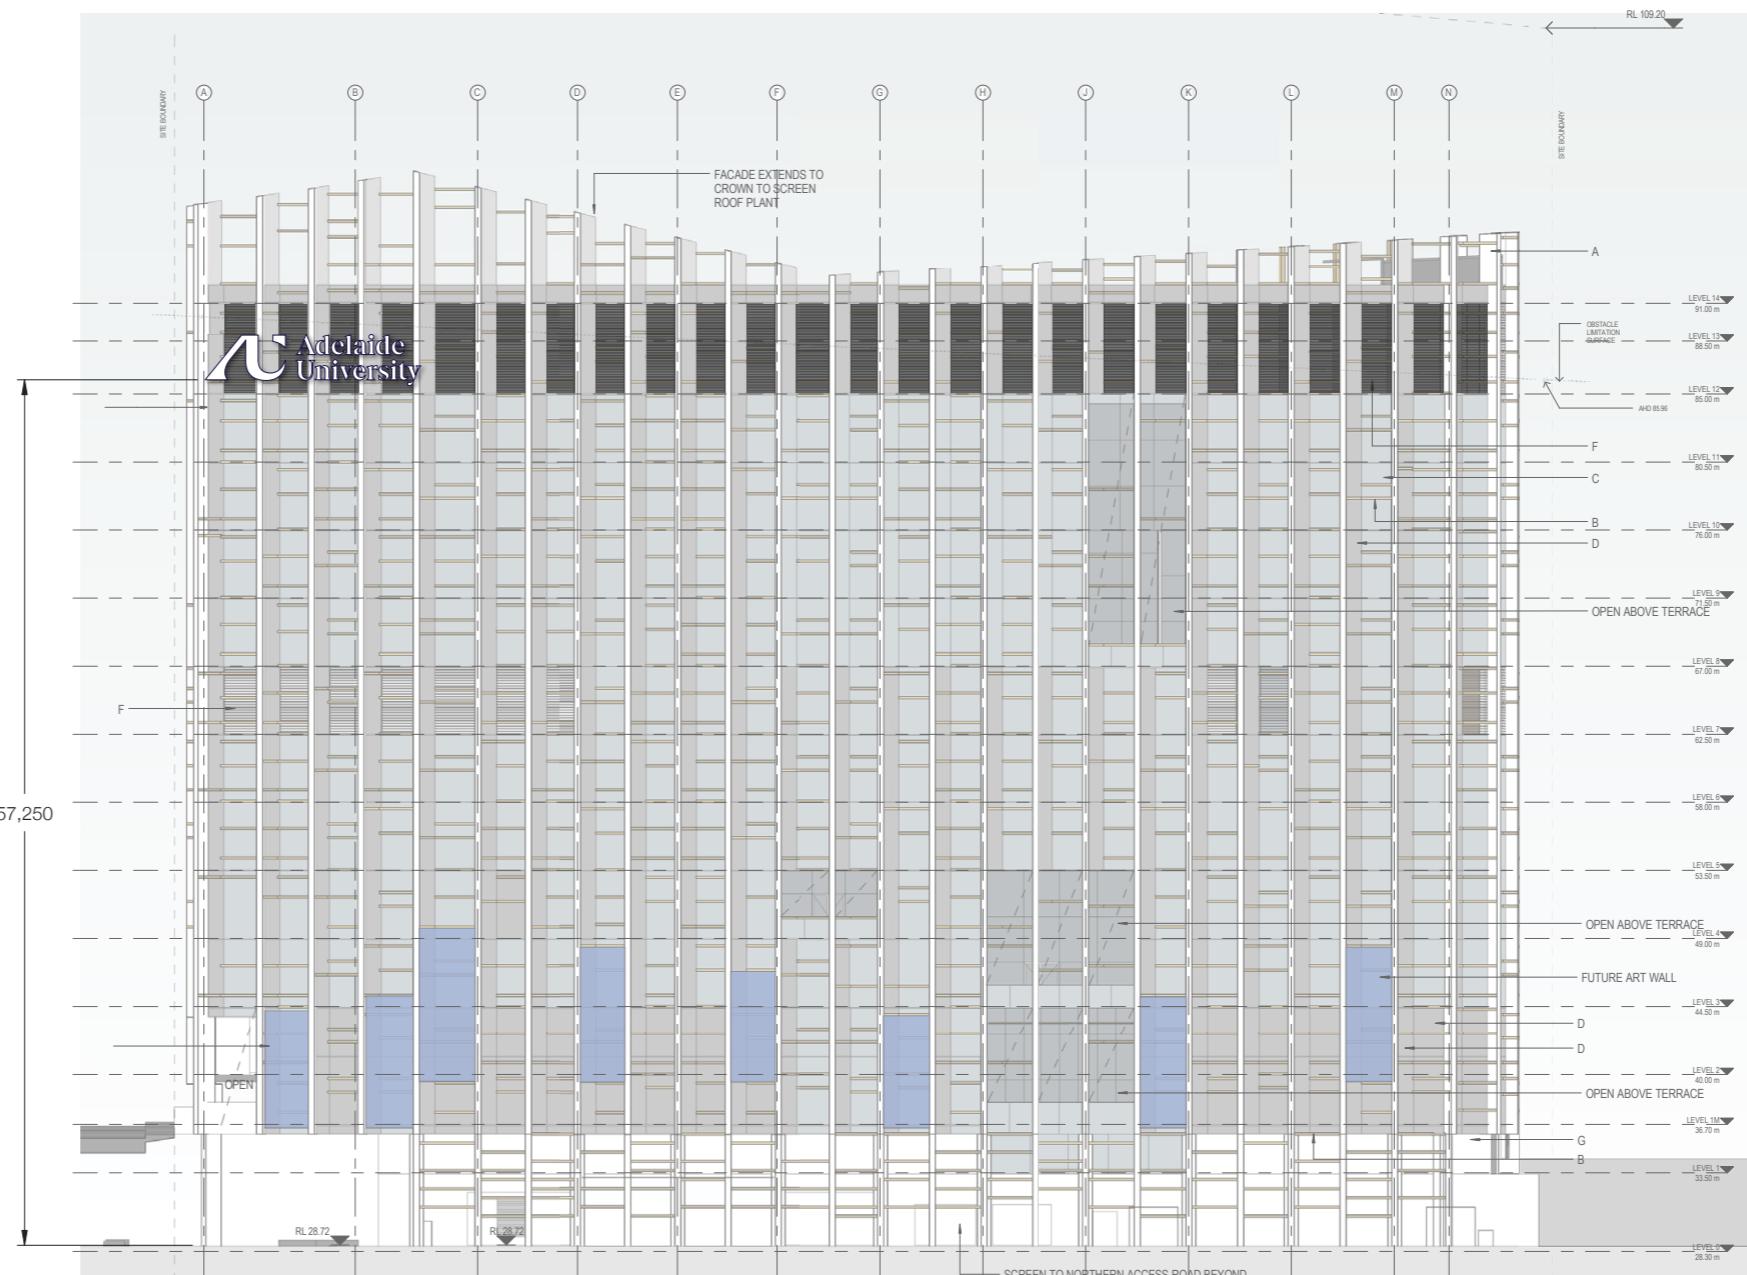

NORTH ELEVATION
SCALE 1:500

Bradley Building

Cnr North Terrace & Morphett Street
Adelaide SA 5000

Location 1

High level sign – inline format
Wall mounted
Single sided
Illuminated

Drawing title

Section detail

Issue Issue date
ISSUE 04 03 APRIL 2025

Drawing no Scale
- @A3

PM Drawn Checked
RL CO CR/RL/NOW

Revision
- - -

Not for construction

General note: These drawings are prepared to communicate design intent only. All message content is indicative. All structural frames, footings and connections to be as per engineer's specifications and requirements. Contractor to ensure all materials, measurements, fixing details and methods are suitable for the site application before manufacture.

Client
ADELAIDE UNIVERSITY

Project
CITY WEST CAMPUS

Document file name
26304-DOC_CITY_WEST_SKY_SIGNS-04

diadem


Australia
1300 613 934

New Zealand
+64 9 377 3736

Hong Kong
+61 3 9670 6767

info@diadem.co
diadem.co

©Copyright Diadem Pty Ltd
Reproductions of the whole or part of this document constitutes an infringement of copyright. The information, ideas and concepts contained in this document are the intellectual property of the recipient(s) of this document. It is prohibited from disclosing such information to any person without the prior written consent of Diadem. Figured dimensions shall take precedence to scaled.

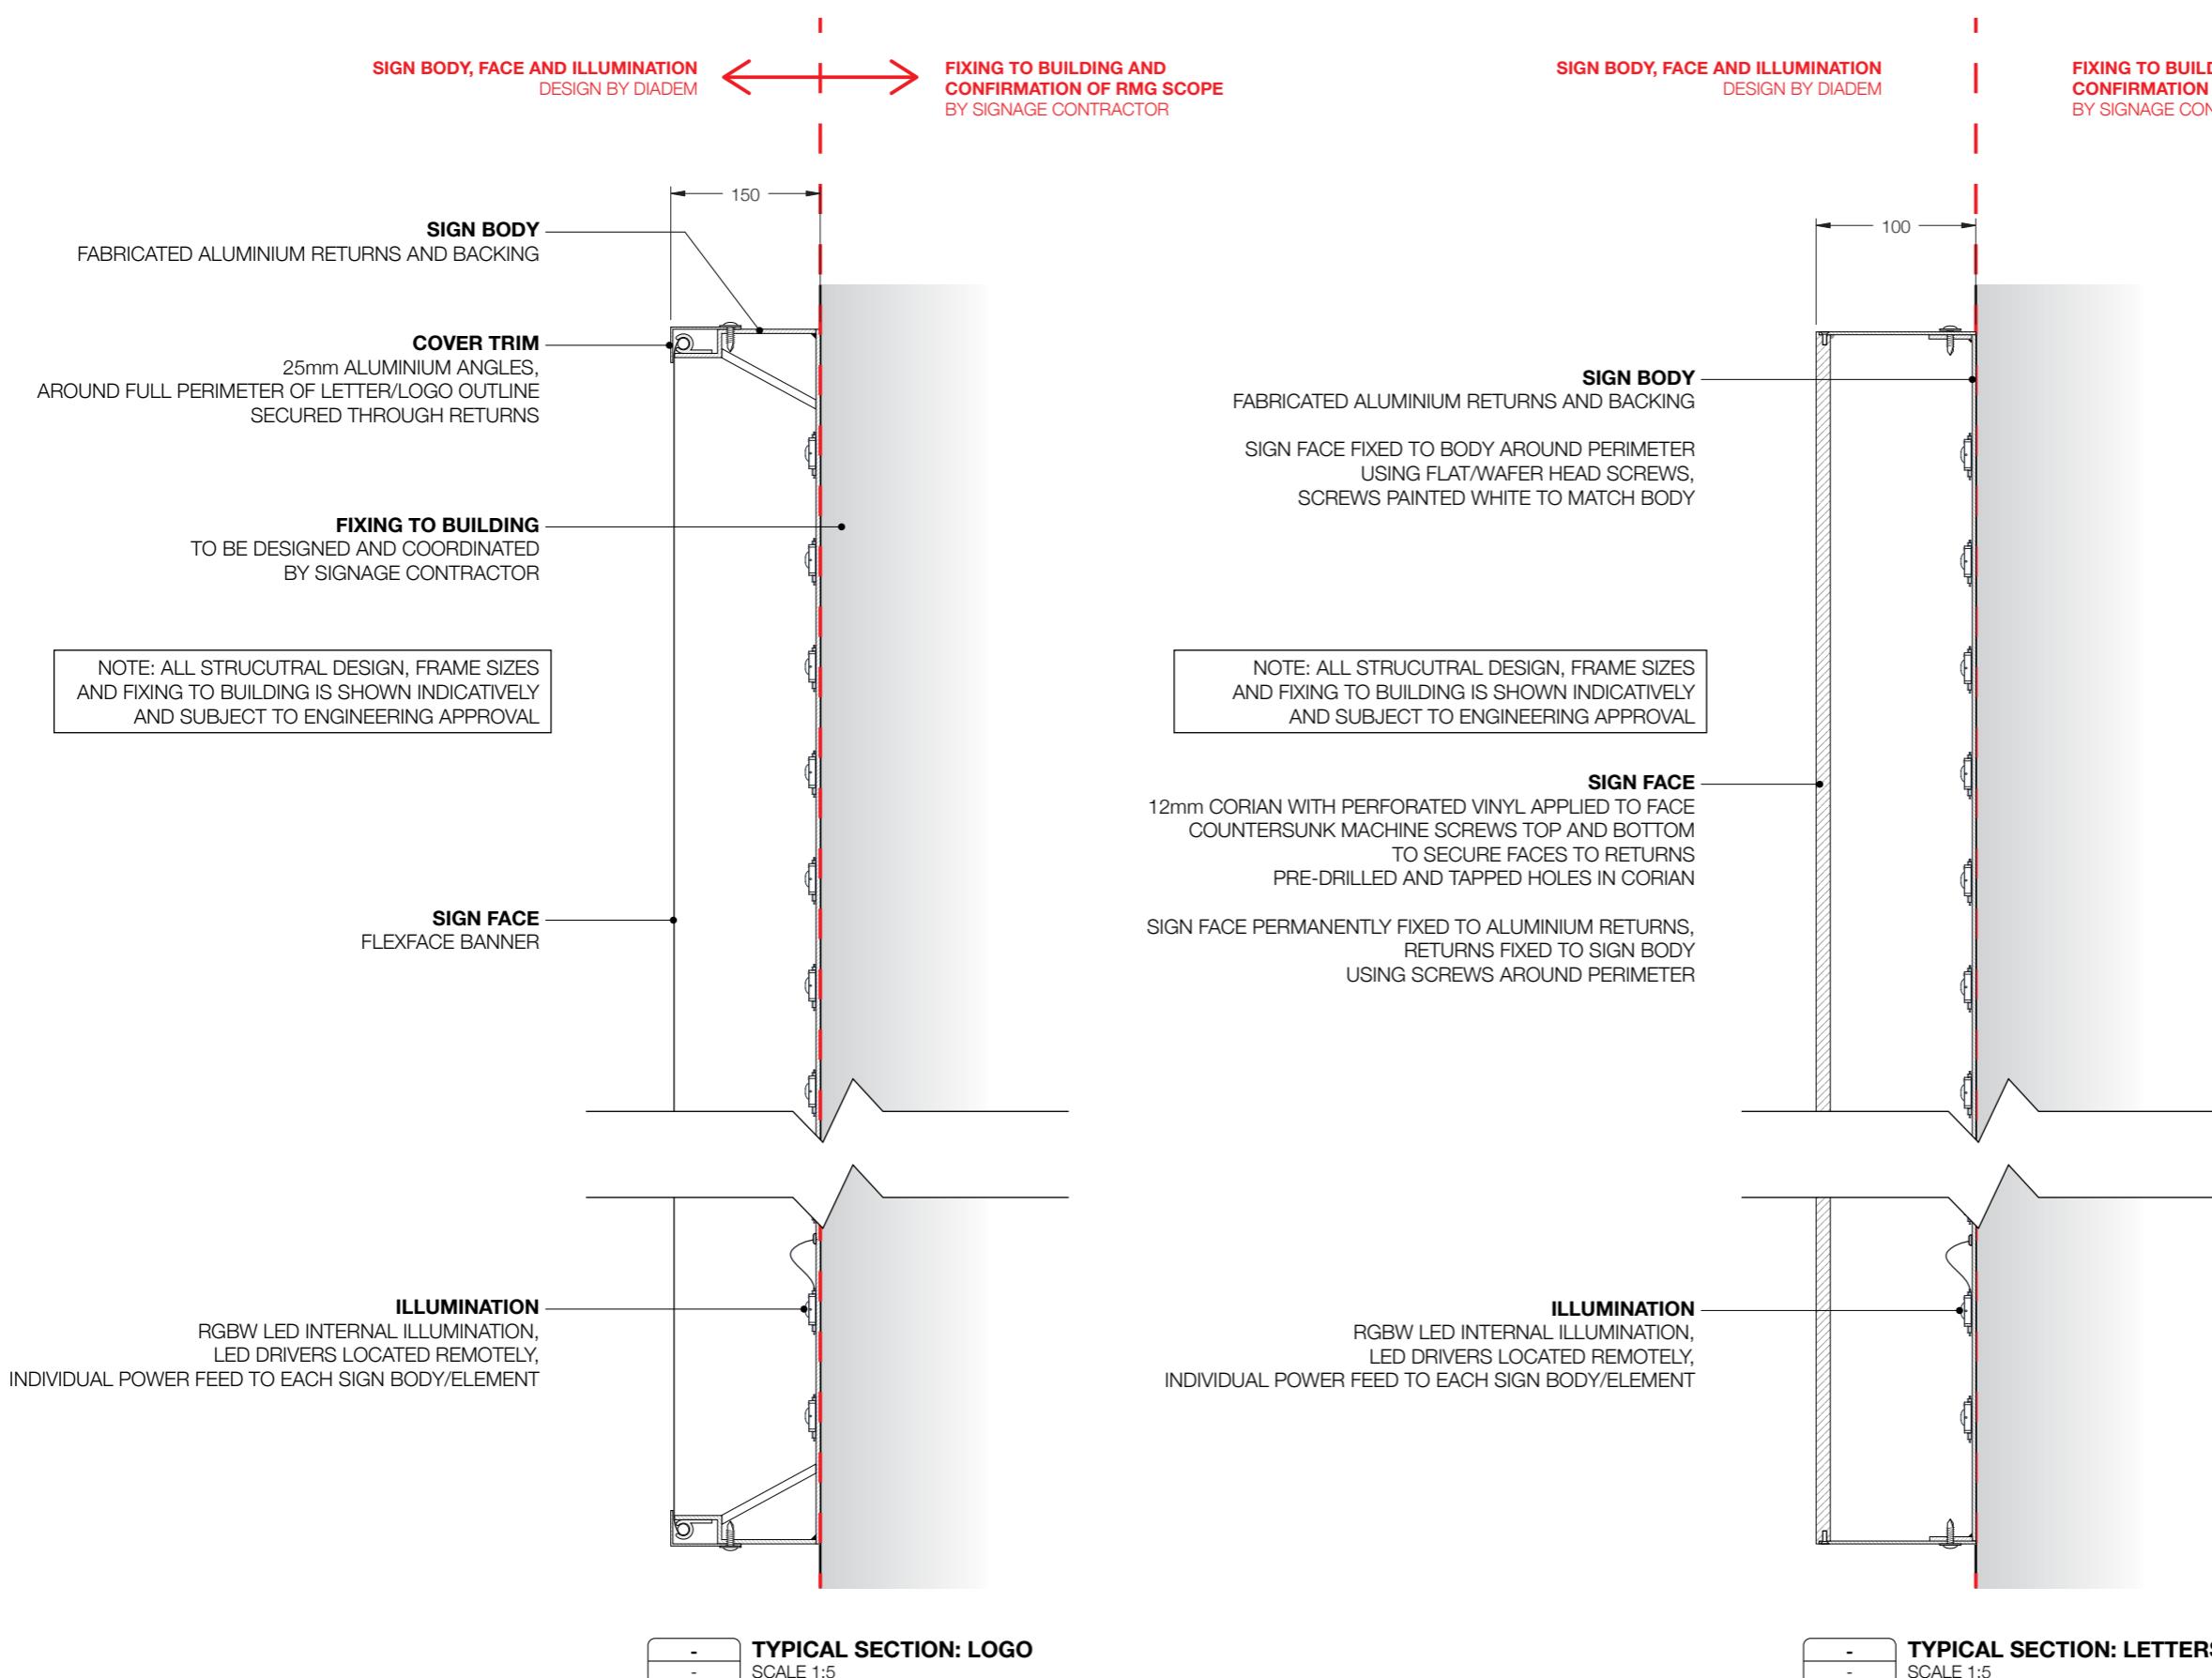

Bradley Building

Cnr North Terrace & Morphett Street
Adelaide SA 5000

Location 1

High level sign –
inline format
Wall mounted
Single sided
Illuminated

Drawing title _____

Removal scope



EXISTING CONDITIONS

RMG: REMOVE EXISTING SIGN AND MAKE GOOD TO FAÇADE PENETRATIONS INCLUDING WATERPROOFING.
ACCESS: CRANE OR ROPE ACCESS FROM ROOF TO BE DETERMINED ON SITE BY CONTRACTOR WITH FACILITIES TEAM. SHADE AWNINGS WILL NEED TO BE REMOVED FOR ACCESS.
ALL IMPACTED SUNSHADES ON THE NORTHERN FAÇADE TO BE REMOVED, LABELLED AND MOVED TO STORAGE – AS ADVISED BY THE UNIVERSITY.
NOTE: RAIL CORRIDOR BELOW – CONTRACTOR TO ALLOW FOR ALL RELEVANT AUTHORITY APPROVALS FOR ACCESS.
NOISE AND VIBRATION MONITORING AND MITIGATION WORK WILL BE REQUIRED DUE TO NATURE OF RESEARCH FACILITY LOCATED IN UPPER LEVELS OF BRADLEY BUILDING – 3RD PARTY CONSULTANTS WILL BE REQUIRED.
TIMING WILL BE LIMITED DUE TO BREEDING CYCLES OF ANIMALS IN FACILITY.
A.U. TO PROVIDE CONTRACTORS WITH THIS DETAIL.
REFER TO A.U. PROVIDED DOCUMENTATION FOR FURTHER INFORMATION.
CONSIDER AND DESIGN APPROPRIATE CLEARANCE TO ENABLE ABSEILING BEHIND THE NEW SIGNS FOR CLEANING THE FAÇADE AND WINDOWS.

Issue Issue date
ISSUE 04 03 APRIL 2025

Drawing no Scale
- @A3

PM Drawn Checked
RL CO CR/RL/NOW

Revision
- - -

Not for construction

General note: These drawings are prepared to communicate design intent only. All message content is indicative. All structural frames, footings and connections to be as per engineer's specifications and requirements. Contractor to ensure all materials, measurements, fixing details and methods are suitable for the site application before manufacture.

Client
ADELAIDE UNIVERSITY

Project
CITY WEST CAMPUS

Document file name
26304-DOC_CITY_WEST_SKY_SIGNS-04

diadem

Australia
1300 613 934

New Zealand
+64 9 377 3736

Hong Kong
+61 3 9670 6767
info@diadem.co
diadem.co

©Copyright Diadem Pty Ltd
Reproductions of the whole or part of this document constitutes an infringement of copyright. The information, ideas and concepts contained in this document are the intellectual property of Diadem. The recipient(s) of this document is prohibited from disclosing such information to any person without the prior written consent of Diadem. Figured dimensions shall take precedence to scaled.

Location 2

Bradley Building


Cnr North Terrace & Morphett Street
Adelaide SA 5000

High level sign – inline format
Wall mounted
Single sided
Illuminated


Drawing title
General arrangement



EXISTING CONDITIONS

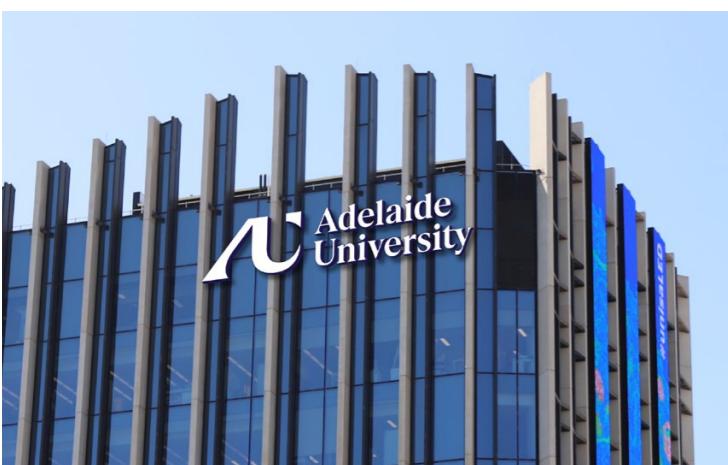

PROPOSED LOCATION

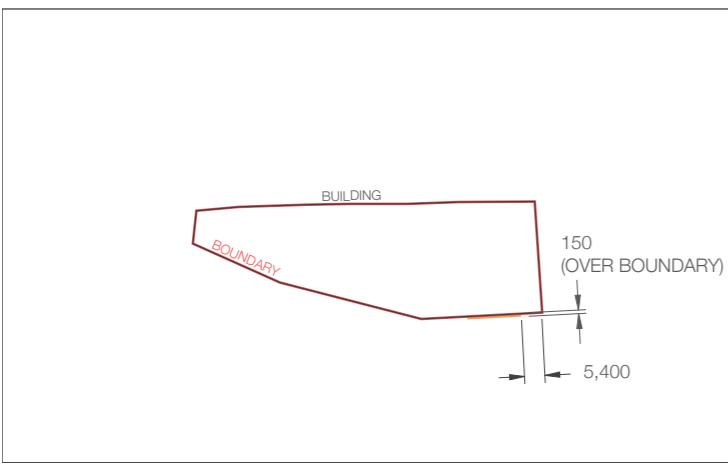

SIGN LOCATION

SCALE 1:2000



LOCATION SPECIFIC INFORMATION

LOGO

FABRICATED ALUMINIUM, RETURNS PAINTED DARK BLUE
WHITE FLEXFACE SIGN FACES
ALUMINIUM TRIM ANGLES TO SECURE SIGN FACE

LETTERS

FABRICATED ALUMINIUM, RETURNS PAINTED DARK BLUE
WHITE CORIAN SIGN FACES


LOGO AND LETTERS FIXED DIRECTLY TO BUILDING FACADE,
INTERNALLY ILLUMINATED THROUGH FACES,
SIGN TO ILLUMINATE WHITE AT NIGHT.

ALL INTERNAL SIGN FACES PAINTED WHITE
LED DRIVERS MUST BE INSTALLED IN AN AGREED-UPON ACCESSIBLE
AREA AND, IF APPROPRIATE, THE REUSE OF THE EXISTING 240V SUPPLY
FROM THE EXISTING SIGNS IS PREFERRED.

EXISTING SIGN TO BE REMOVED.



SIGN DETAIL
SCALE 1:100

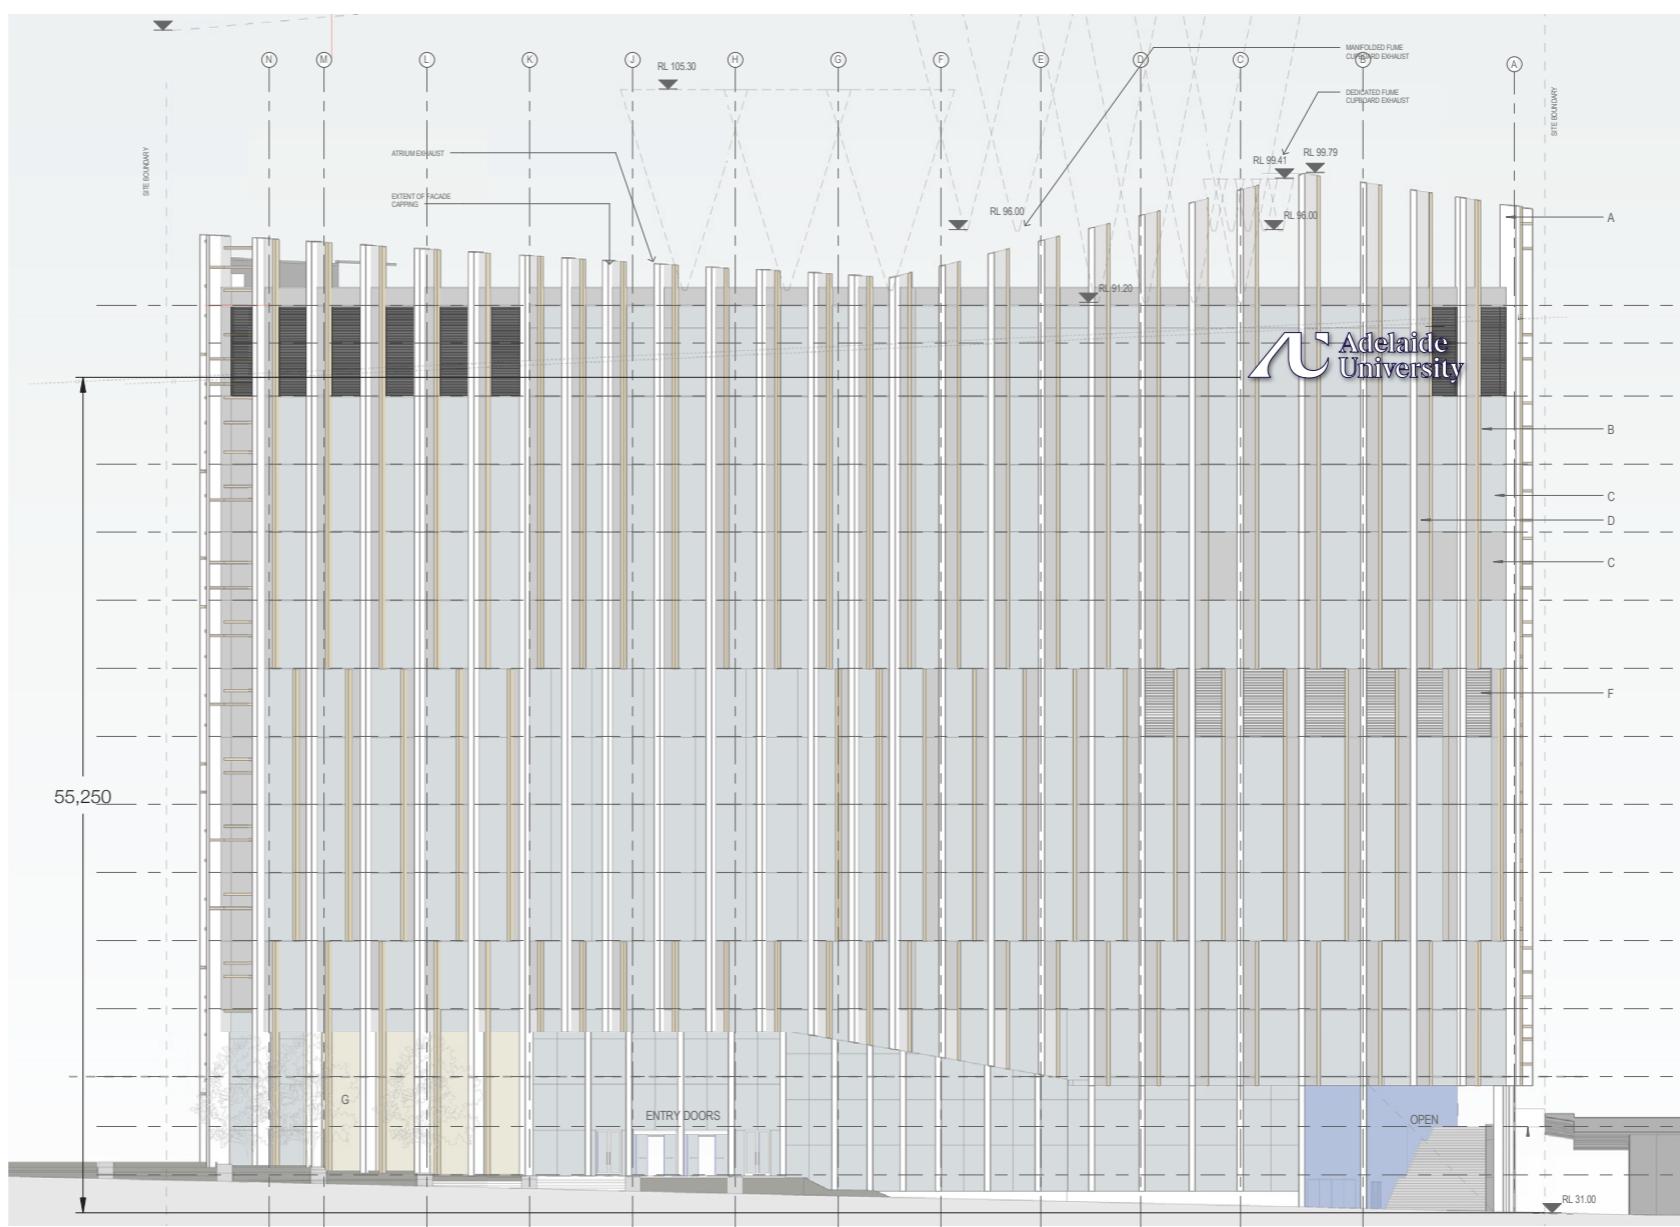

SOUTH ELEVATION
SCALE 1:500

Issue Issue date
ISSUE 04 03 APRIL 2025

Drawing no Scale
- @A3

PM Drawn Checked
RL CO CR/RL/NOW

Revision
- - -

Not for construction

General note: These drawings are prepared to communicate design intent only. All message content is indicative. All structural frames, footings and connections to be as per engineer's specifications and requirements. Contractor to ensure all materials, measurements, fixing details and methods are suitable for the site application before manufacture.

Client
ADELAIDE UNIVERSITY

Project
CITY WEST CAMPUS

Document file name
26304-DOC_CITY_WEST_SKY_SIGNS-04

diadem

Australia
1300 613 934

New Zealand
+64 9 377 3736

Hong Kong
+61 3 9670 6767
info@diadem.co
diadem.co

©Copyright Diadem Pty Ltd
Reproductions of the whole or part of this document constitutes an infringement of copyright. The information, ideas and concepts contained in this document are the intellectual property of the recipient(s). The document is prohibited from disclosing such information to any person without the prior written consent of Diadem. Figured dimensions shall take precedence to scaled.

Bradley Building

Cnr North Terrace & Morphett Street
Adelaide SA 5000

Location 2

High level sign – inline format
Wall mounted
Single sided
Illuminated

Drawing title

Section detail

Issue Issue date
ISSUE 04 03 APRIL 2025

Drawing no Scale
- @A3

PM Drawn Checked
RL CO CR/RL/NOW

Revision
- - -

Not for construction

General note: These drawings are prepared to communicate design intent only. All message content is indicative. All structural frames, footings and connections to be as per engineer's specifications and requirements. Contractor to ensure all materials, measurements, fixing details and methods are suitable for the site application before manufacture.

Client
ADELAIDE UNIVERSITY

Project
CITY WEST CAMPUS

Document file name
26304-DOC_CITY_WEST_SKY_SIGNS-04

diadem


Australia
1300 613 934

New Zealand
+64 9 377 3736

Hong Kong
+61 3 9670 6767

info@diadem.co
diadem.co

©Copyright Diadem Pty Ltd
Reproductions of the whole or part of this document constitutes an infringement of copyright. The information, ideas and concepts contained in this document are the intellectual property of Diadem. The recipient(s) of this document is prohibited from disclosing such information to any person without the prior written consent of Diadem. Figured dimensions shall take precedence to scaled.

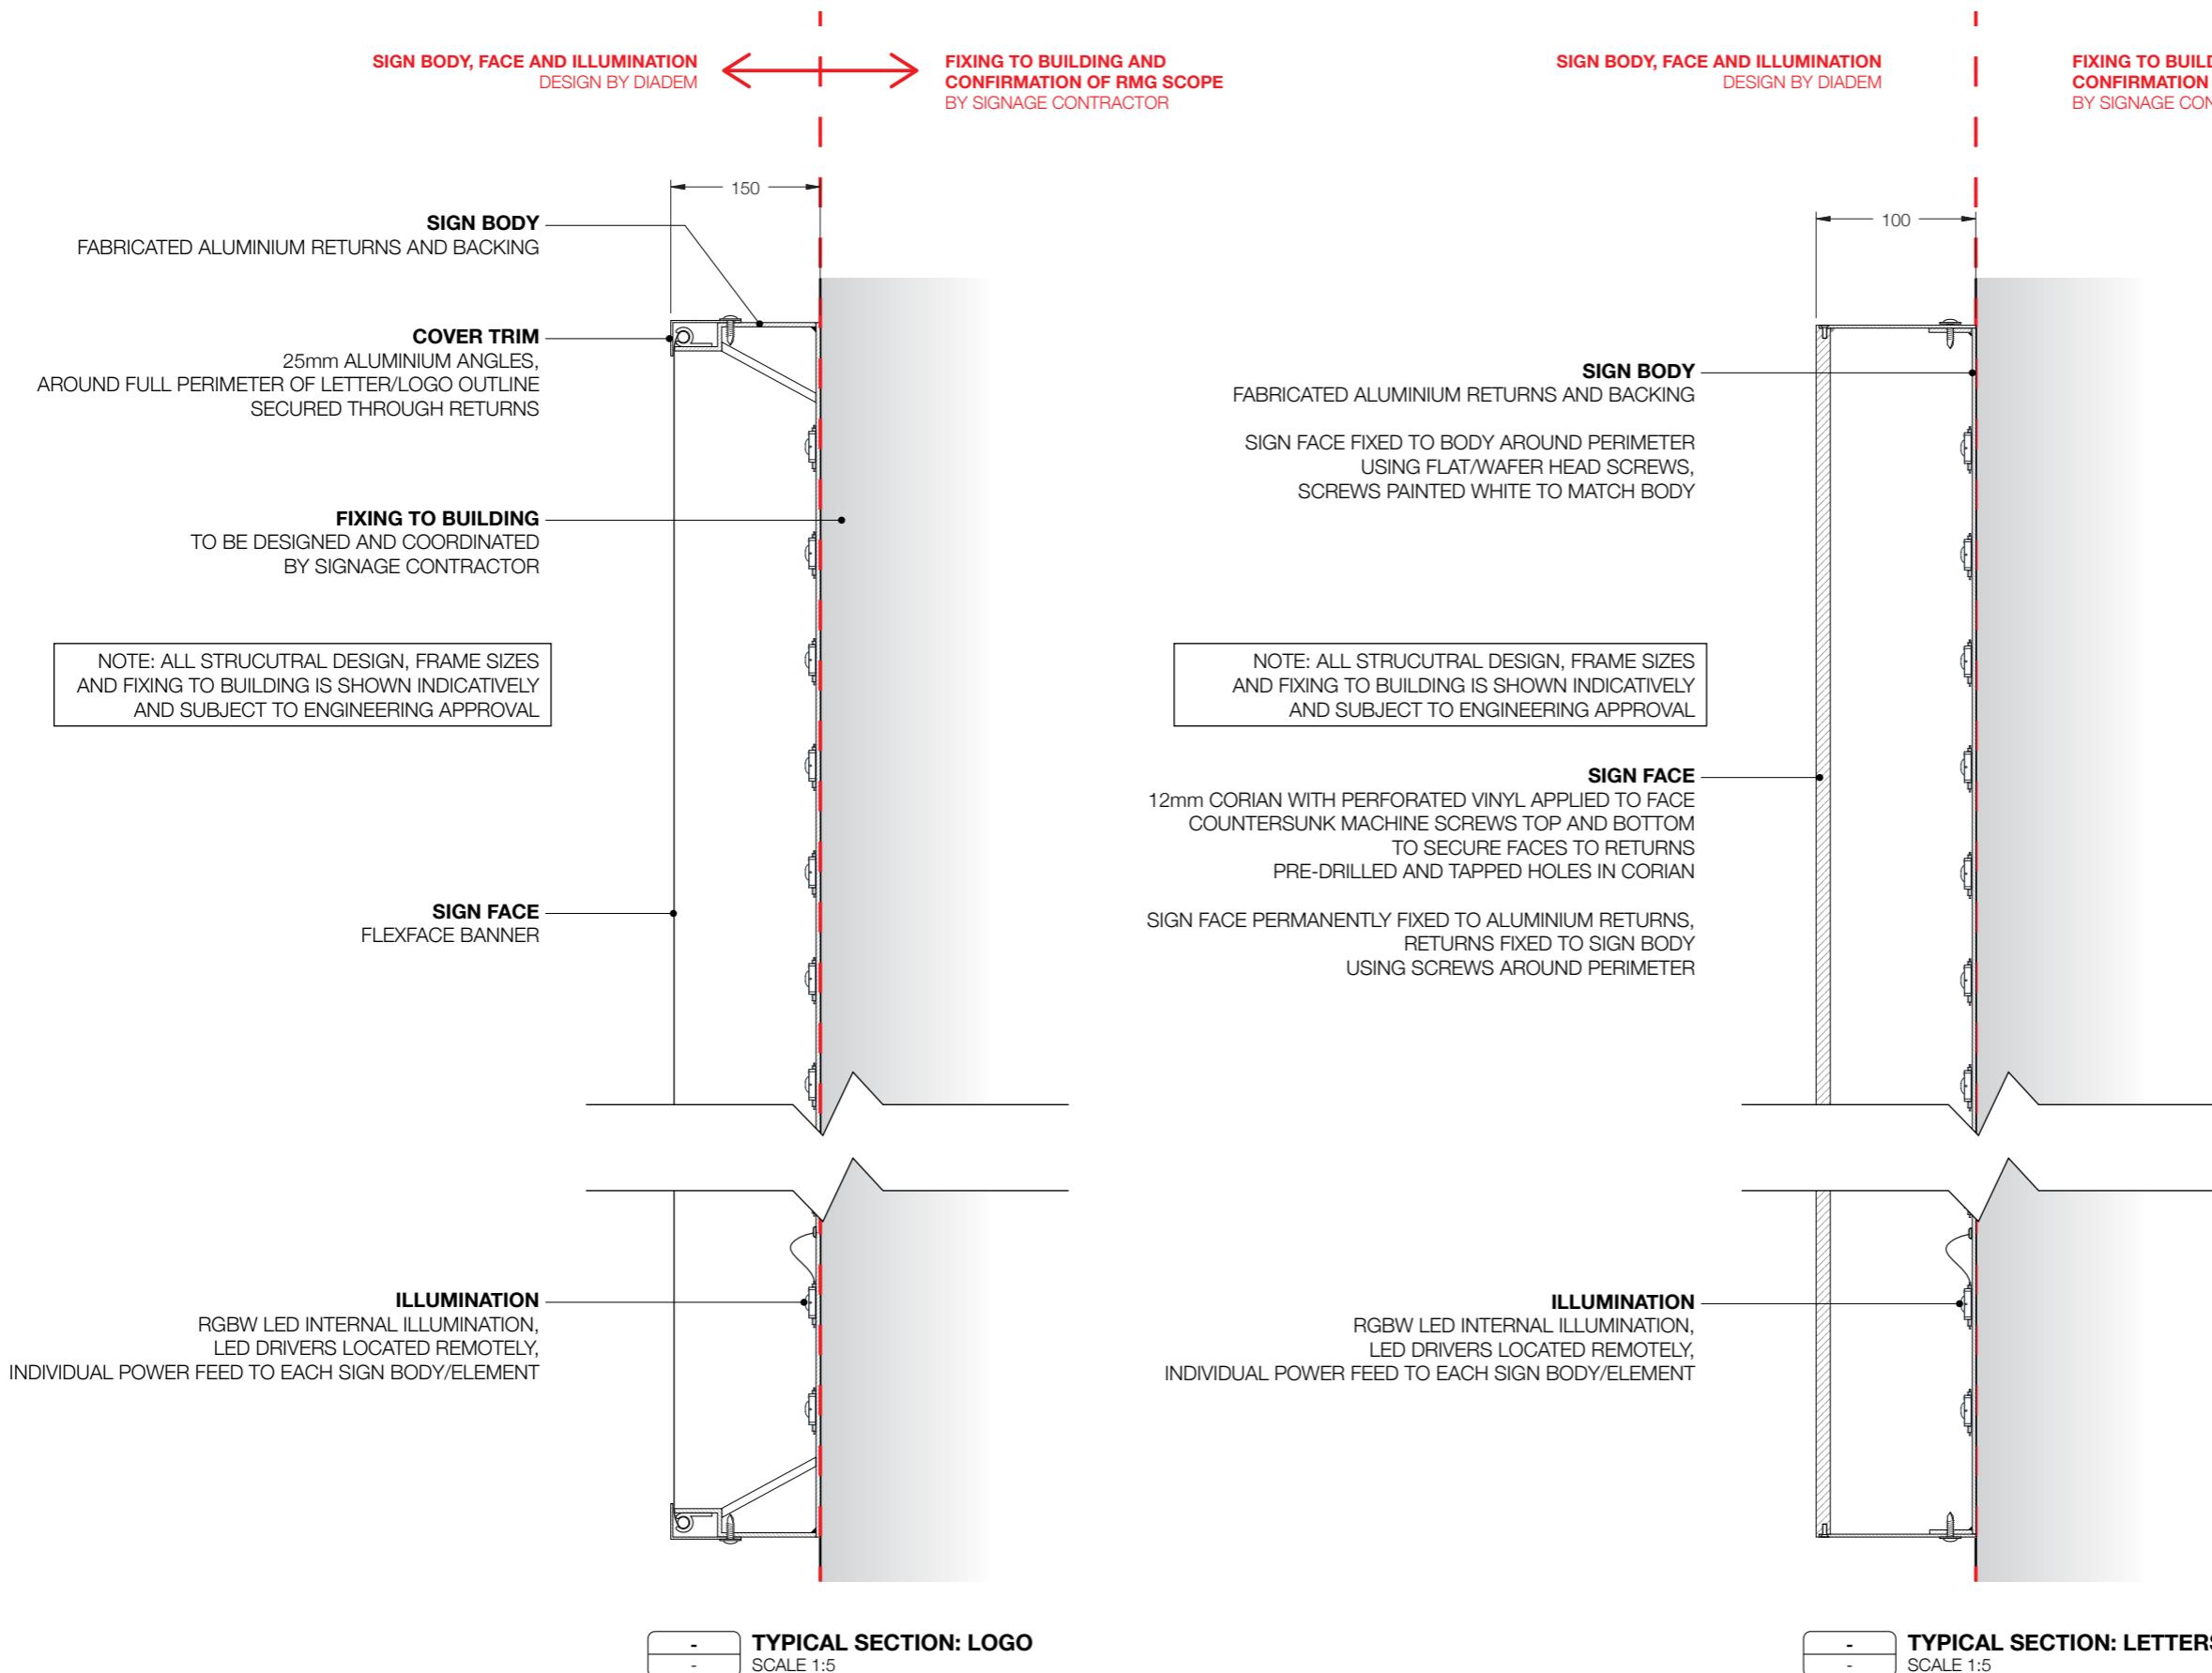

Bradley Building

Cnr North Terrace & Morphett Street
Adelaide SA 5000

Location 2

High level sign –
inline format
Wall mounted
Single sided
Illuminated

Drawing title _____

Removal scope



EXISTING CONDITIONS

RMG: REMOVE EXISTING SIGN AND MAKE GOOD TO FAÇADE PENETRATIONS INCLUDING WATERPROOFING.
ACCESS: CRANE OR ROPE ACCESS FROM ROOF TO BE DETERMINED ON SITE BY CONTRACTOR WITH FACILITIES TEAM. SHADE AWNINGS WILL NEED TO BE REMOVED FOR ACCESS.
NOTE: NOISE AND VIBRATION MONITORING AND MITIGATION WORK WILL BE REQUIRED DUE TO NATURE OF RESEARCH FACILITY LOCATED IN UPPER LEVELS OF BRADLEY BUILDING – 3RD PARTY CONSULTANTS WILL BE REQUIRED. TIMING WILL BE LIMITED DUE TO BREEDING CYCLES OF ANIMALS IN FACILITY. A.U. TO PROVIDE CONTRACTORS WITH THIS DETAIL. REFER TO A.U. PROVIDED DOCUMENTATION FOR FURTHER INFORMATION. CONSIDER AND DESIGN APPROPRIATE CLEARANCE TO ENABLE ABSEILING BEHIND THE NEW SIGNS FOR CLEANING THE FAÇADE AND WINDOWS.

Issue	Issue date	
ISSUE 04	03 APRIL 2025	
Drawing no	Scale	
-	@A3	
PM	Drawn	Checked
RL	CO	CR/RL/NOW

Revision _____

-- -- -

Not for construction

General note: These drawings are prepared to communicate design intent only. All message content is indicative. All structural frames, footings and connections to be as per engineer's specifications and requirements. Contractor to ensure all materials, measurements, fixing details and methods are suitable for the site application before manufacture.

Client _____
ADELAIDE UNIVERSITY

Project _____
CITY WEST CAMPUS

Document file name _____
26304-DOC_CITY_WEST_SKY_SIGNS-04

diadem

Australia
1300 613 934

New Zealand
+64 9 377 3736

Hong Kong
+61 3 9670 6767
info@diadem.co
diadem.co


©Copyright Diadem Pty Ltd
Reproductions of the whole or part of this document constitutes an infringement of copyright. The information, ideas and concepts contained in this document are the intellectual property of Diadem. The recipient(s) of this document is prohibited from disclosing such information to any person without the prior written consent of Diadem. Figured dimensions shall take precedence to scaled.

Location 3

Adelaide Medical School Building

4 North Terrace
Adelaide SA 5000


High level sign – stacked format
Wall mounted
Single sided
Illuminated

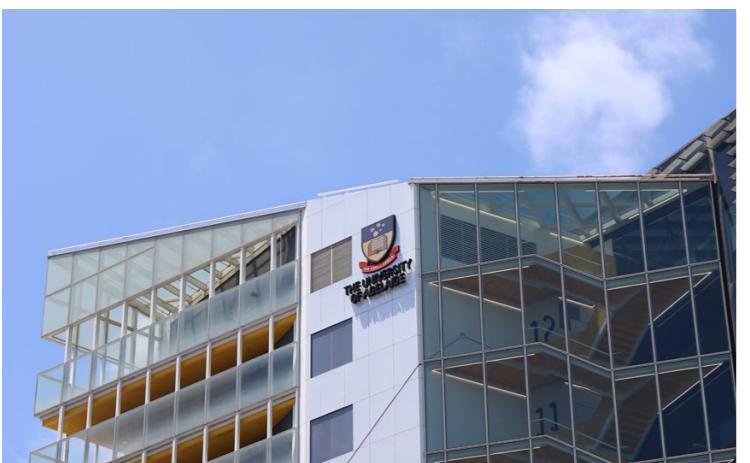

EXISTING CONDITIONS



PROPOSED LOCATION

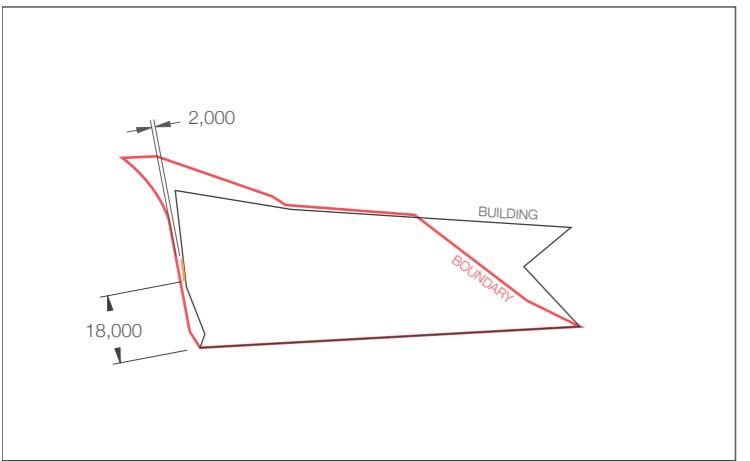

SIGN LOCATION

SCALE 1:2000



LOCATION SPECIFIC INFORMATION

LOGO

FABRICATED ALUMINIUM, RETURNS PAINTED WHITE FLEXFACE SIGN FACES WITH BLUE DAY/NIGHT VINYL ALUMINIUM TRIM ANGLES TO SECURE SIGN FACE

LETTERS

FABRICATED ALUMINIUM, RETURNS PAINTED WHITE CORIAN SIGN FACES WITH BLUE DAY/NIGHT VINYL

LOGO AND LETTERS FIXED DIRECTLY TO BUILDING FAÇADE, INTERNALLY ILLUMINATED THROUGH FACES, SIGN TO ILLUMINATE WHITE AT NIGHT.


ALL INTERNAL SIGN FACES PAINTED WHITE

LED DRIVERS MUST BE INSTALLED IN AN AGREED-UPON ACCESSIBLE AREA AND, IF APPROPRIATE, THE REUSE OF THE EXISTING 240V SUPPLY FROM THE EXISTING SIGNS IS PREFERRED.

EXISTING SIGN TO BE REMOVED.



SIGN DETAIL
SCALE 1:100

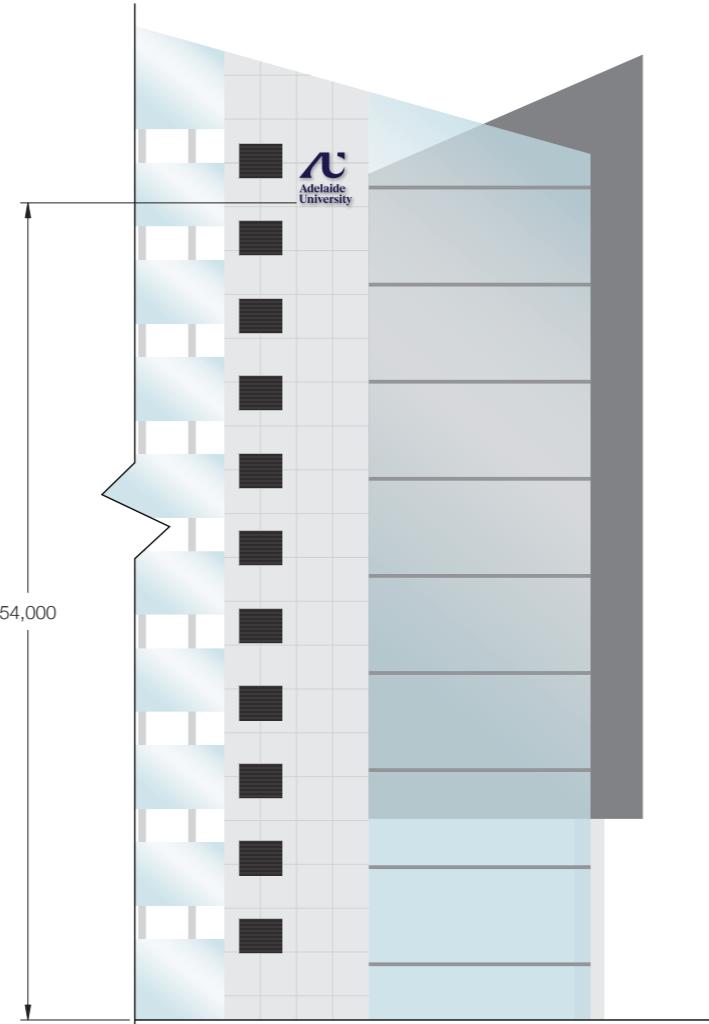

WEST ELEVATION
SCALE 1:500

Issue Issue date
ISSUE 04 03 APRIL 2025

Drawing no Scale
- @A3

PM Drawn Checked
RL CO CR/RL/NOW

Revision
- - -

Not for construction

General note: These drawings are prepared to communicate design intent only. All message content is indicative. All structural frames, footings and connections to be as per engineer's specifications and requirements. Contractor to ensure all materials, measurements, fixing details and methods are suitable for the site application before manufacture.

Client
ADELAIDE UNIVERSITY

Project
CITY WEST CAMPUS

Document file name
26304-DOC_CITY_WEST_SKY_SIGNS-04

diadem

Australia

1300 613 934

New Zealand

+64 9 377 3736

Hong Kong

+61 3 9670 6767

info@diadem.co

diadem.co

©Copyright Diadem Pty Ltd

Reproductions of the whole or part of this document constitutes an infringement of copyright. The information, ideas and concepts contained in this document are the intellectual property of the recipient(s) of this document. It is prohibited from disclosing such information to any person without the prior written consent of Diadem. Figured dimensions shall take precedence to scaled.

Adelaide Medical School Building

4 North Terrace
Adelaide SA 5000

Location 3

High level sign – stacked format
Wall mounted
Single sided
Illuminated

Drawing title

Section detail

Issue Issue date
ISSUE 04 03 APRIL 2025

Drawing no Scale
- @A3

PM Drawn Checked
RL CO CR/RL/NOW

Revision
- - -

Not for construction

General note: These drawings are prepared to communicate design intent only. All message content is indicative. All structural frames, footings and connections to be as per engineer's specifications and requirements. Contractor to ensure all materials, measurements, fixing details and methods are suitable for the site application before manufacture.

Client
ADELAIDE UNIVERSITY


Project
CITY WEST CAMPUS

Document file name
26304-DOC_CITY_WEST_SKY_SIGNS-04

diadem

Australia
1300 613 934
New Zealand
+64 9 377 3736
Hong Kong
+61 3 9670 6767
info@diadem.co
diadem.co

©Copyright Diadem Pty Ltd
Reproductions of the whole or part of this document constitutes an infringement of copyright. The information, ideas and concepts contained in this document are the intellectual property of the recipient(s) of this document. It is prohibited from disclosing such information to any person without the prior written consent of Diadem. Figured dimensions shall take precedence to scaled.

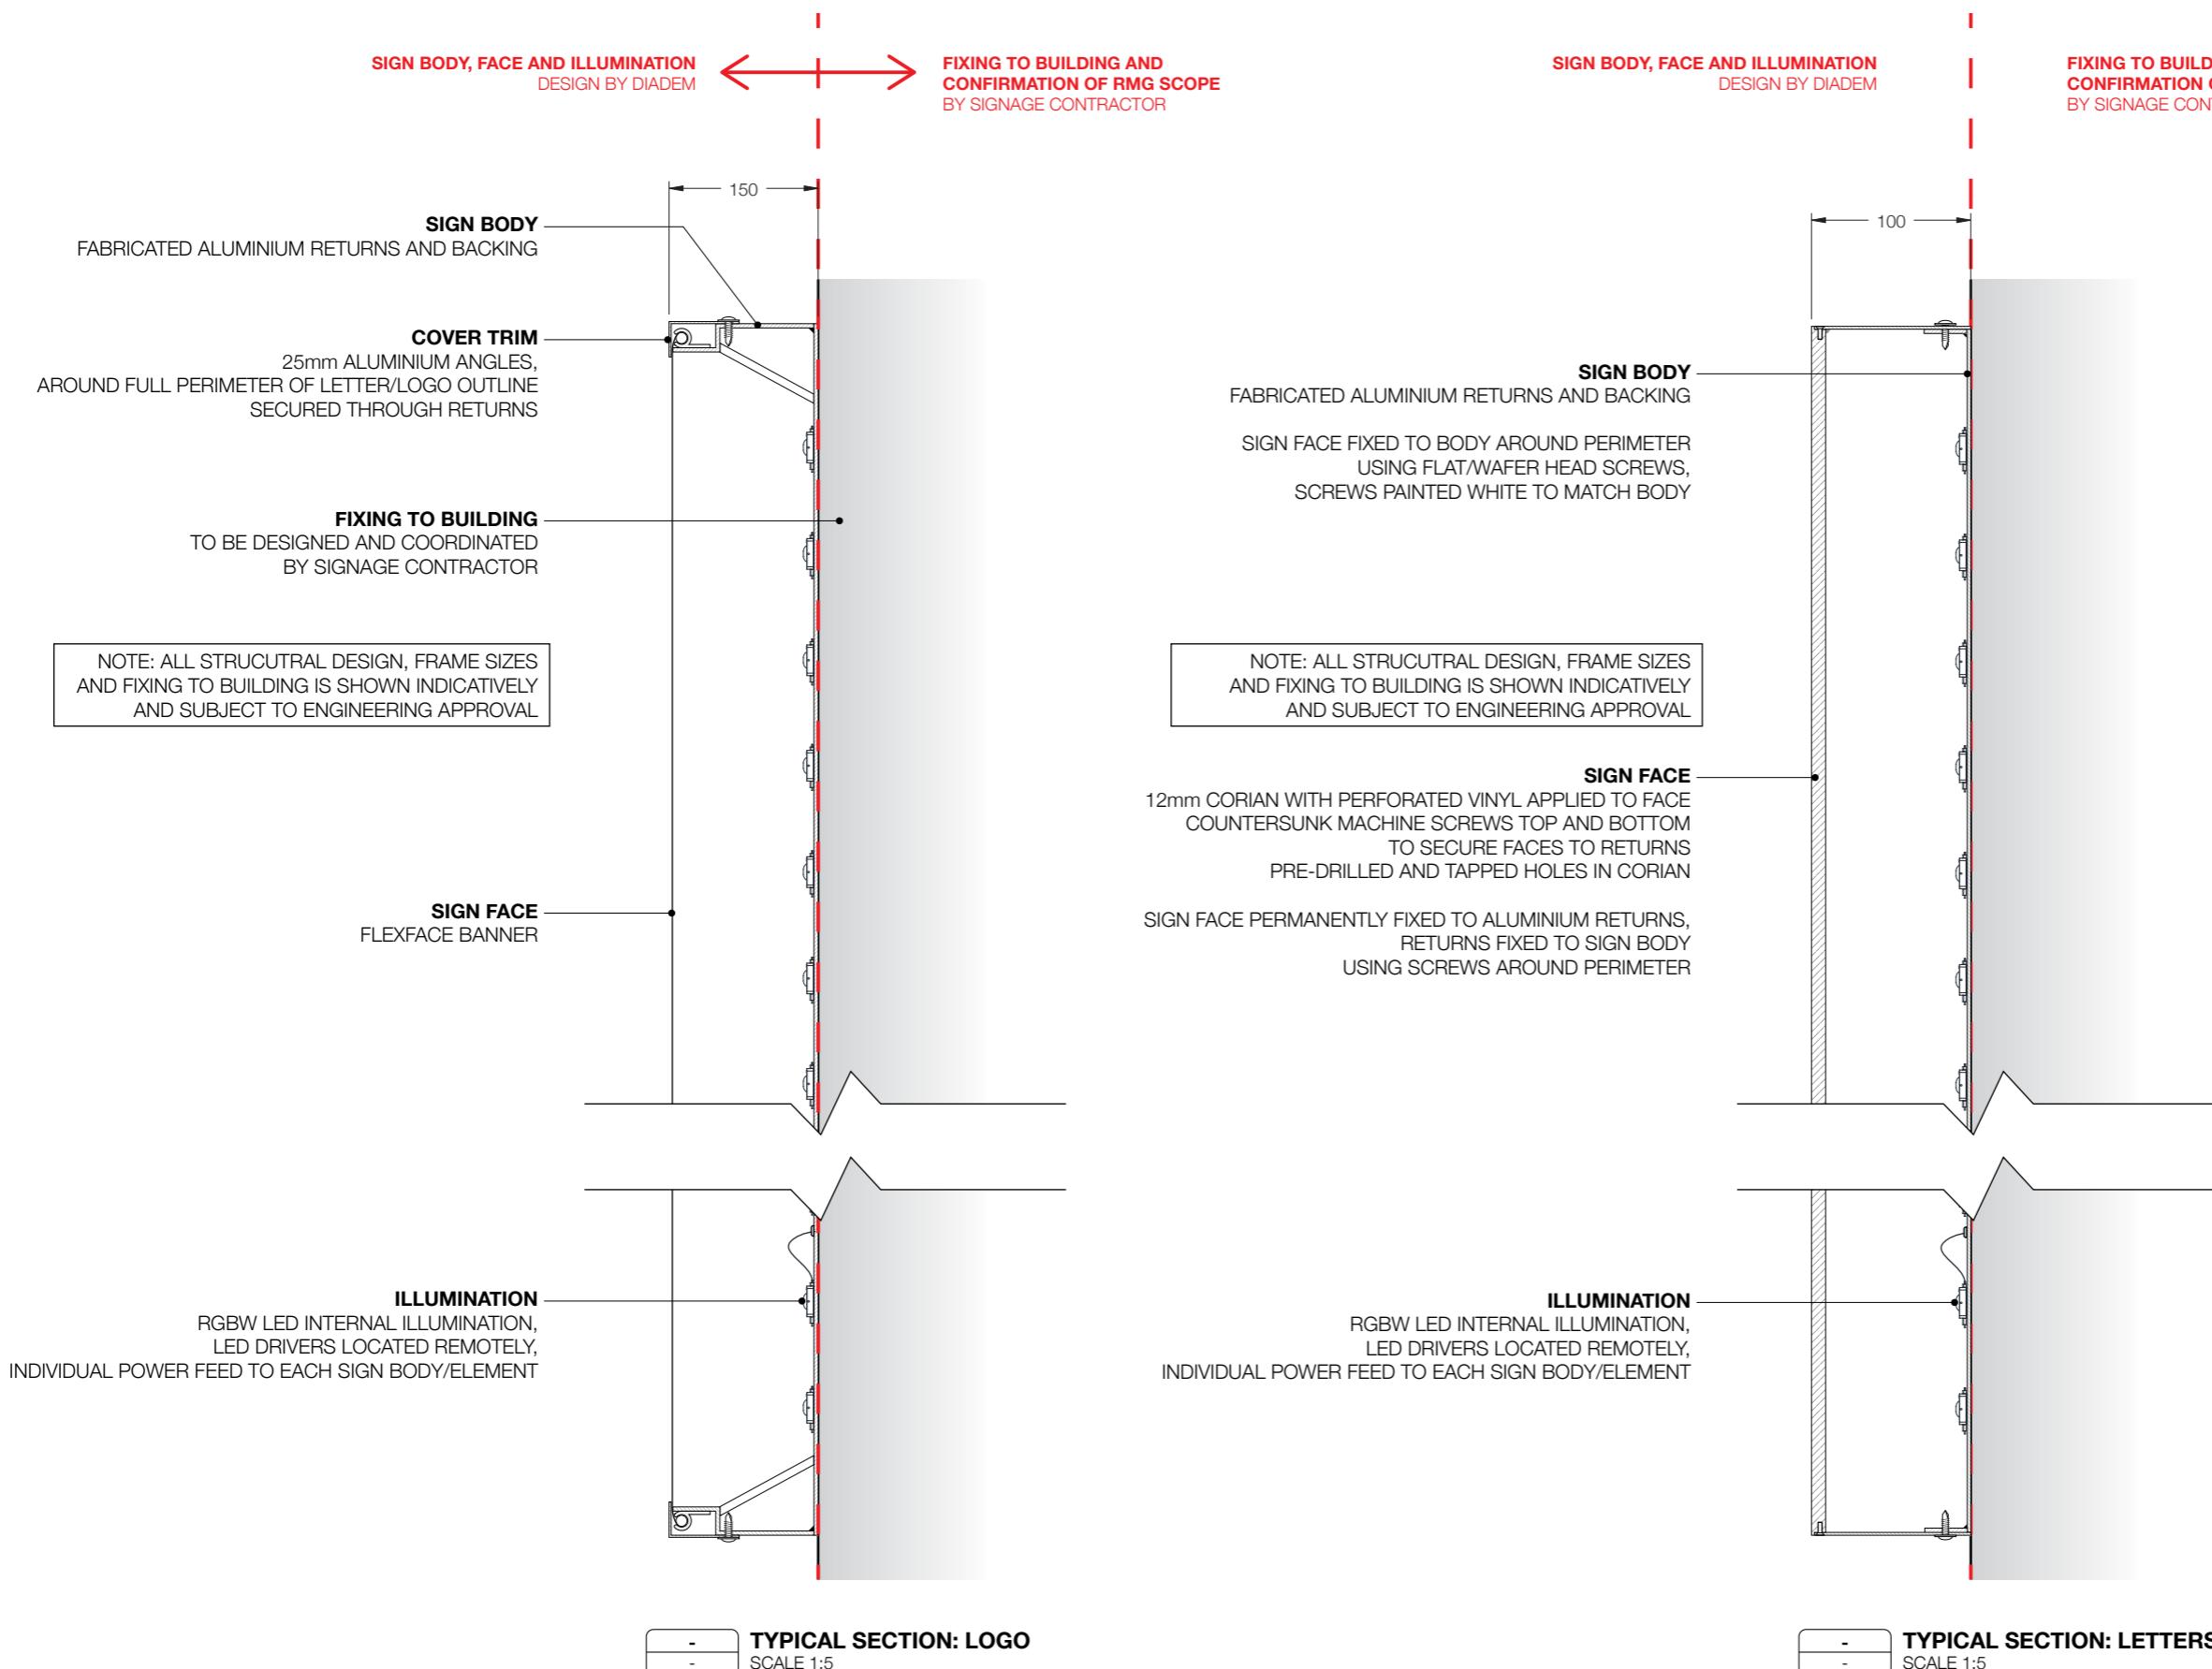

Adelaide Medical School Building

4 North Terrace
Adelaide SA 5000

Location 3

High level sign – stacked format
Wall mounted
Single sided
Illuminated

Drawing title _____

Removal scope



EXISTING CONDITIONS

RMG: REMOVE EXISTING SIGN AND REPLACE FAÇADE PANELS IMPACTED BY REMOVAL
CONTRACTOR TO MATCH EXISTING FAÇADE, A.U. TO PROVIDE DETAIL OF EXISTING PANEL REQUIREMENTS AND FIXINGS METHODS.
ACCESS: CRANE OR ROPE ACCESS FROM ROOF TO BE DETERMINED ON SITE BY CONTRACTOR WITH FACILITIES TEAM.
NOTE: REFER TO A.U. PROVIDED DOCUMENTATION FOR FURTHER INFORMATION.

Issue Issue date
ISSUE 04 03 APRIL 2025

Drawing no Scale
- @A3

PM Drawn Checked
RL CO CR/RL/NOW

Revision
- - -

Not for construction

General note: These drawings are prepared to communicate design intent only. All message content is indicative. All structural frames, footings and connections to be as per engineer's specifications and requirements. Contractor to ensure all materials, measurements, fixing details and methods are suitable for the site application before manufacture.

Client
ADELAIDE UNIVERSITY

Project
CITY WEST CAMPUS

Document file name
26304-DOC_CITY_WEST_SKY_SIGNS-04

diadem

Australia

1300 613 934

New Zealand

+64 9 377 3736

Hong Kong

+61 3 9670 6767


info@diadem.co

diadem.co


©Copyright Diadem Pty Ltd
Reproductions of the whole or part of this document constitutes an infringement of copyright. The information, ideas and concepts contained in this document are the copyright of Diadem Pty Ltd. The recipient(s) of this document is prohibited from disclosing such information to any person without the prior written consent of Diadem. Figured dimensions shall take precedence to scaled.



EXISTING CONDITIONS

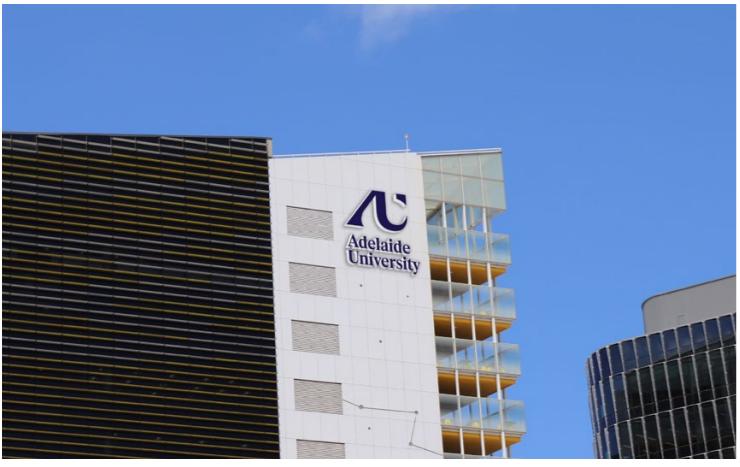

PROPOSED LOCATION

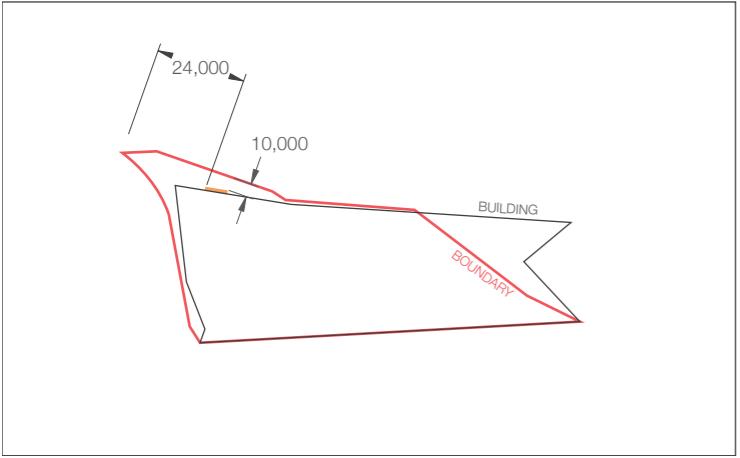

LOCATION SPECIFIC INFORMATION

LOGO

FABRICATED ALUMINIUM, RETURNS PAINTED WHITE FLEXFACE SIGN FACES WITH BLUE DAY/NIGHT VINYL ALUMINIUM TRIM ANGLES TO SECURE SIGN FACE

LETTERS


FABRICATED ALUMINIUM, RETURNS PAINTED WHITE CORIAN SIGN FACES WITH BLUE DAY/NIGHT VINYL

LOGO AND LETTERS FIXED DIRECTLY TO BUILDING FAÇADE, INTERNALLY ILLUMINATED THROUGH FACES, SIGN TO ILLUMINATE WHITE AT NIGHT.


ALL INTERNAL SIGN FACES PAINTED WHITE

LED DRIVERS MUST BE INSTALLED IN AN AGREED-UPON ACCESSIBLE AREA AND, IF APPROPRIATE, THE REUSE OF THE EXISTING 240V SUPPLY FROM THE EXISTING SIGNS IS PREFERRED.

EXISTING SIGN TO BE REMOVED.

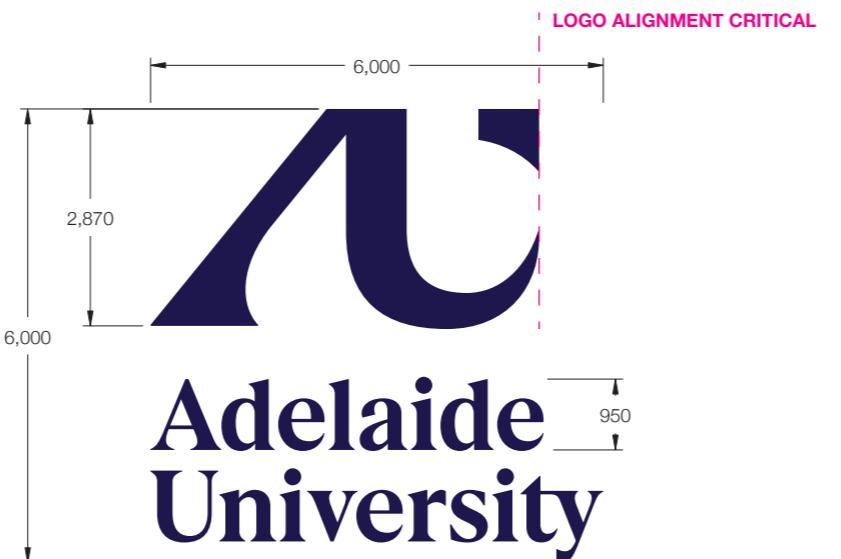

SIGN DETAIL
SCALE 1:100

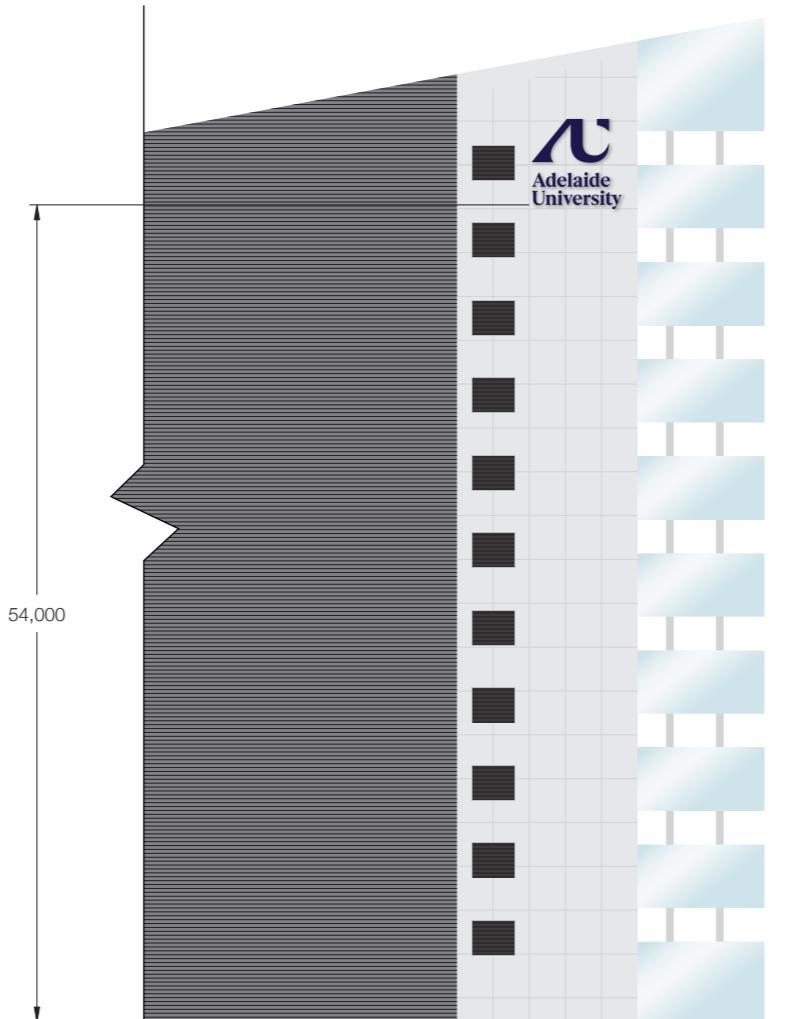

Adelaide Medical School Building

4 North Terrace
Adelaide SA 5000

Location 4

High level sign – stacked format
Wall mounted
Single sided
Illuminated

Drawing title

General arrangement

Issue Issue date
ISSUE 04 03 APRIL 2025

Drawing no Scale
- @A3

PM Drawn Checked
RL CO CR/RL/NOW

Revision

Not for construction

General note: These drawings are prepared to communicate design intent only. All message content is indicative. All structural frames, footings and connections to be as per engineer's specifications and requirements. Contractor to ensure all materials, measurements, fixing details and methods are suitable for the site application before manufacture.

Client
ADELAIDE UNIVERSITY

Project
CITY WEST CAMPUS

Document file name
26304-DOC_CITY_WEST_SKY_SIGNS-04

diadem

Australia

1300 613 934

New Zealand

+64 9 377 3736

Hong Kong

+61 3 9670 6767

info@diadem.co

diadem.co

©Copyright Diadem Pty Ltd
Reproductions of the whole or part of this document constitutes an infringement of copyright. The information, ideas and concepts contained in this document are the intellectual property of the recipient(s) of this document. It is prohibited from disclosing such information to any person without the prior written consent of Diadem. Figured dimensions shall take precedence to scaled.

Adelaide Medical School Building

4 North Terrace
Adelaide SA 5000

Location 4

High level sign – stacked format
Wall mounted
Single sided
Illuminated

Drawing title

Section detail

Issue Issue date
ISSUE 04 03 APRIL 2025

Drawing no Scale
- @A3

PM Drawn Checked
RL CO CR/RL/NOW

Revision
- - -

Not for construction

General note: These drawings are prepared to communicate design intent only. All message content is indicative. All structural frames, footings and connections to be as per engineer's specifications and requirements. Contractor to ensure all materials, measurements, fixing details and methods are suitable for the site application before manufacture.

Client
ADELAIDE UNIVERSITY


Project
CITY WEST CAMPUS

Document file name
26304-DOC_CITY_WEST_SKY_SIGNS-04

diadem

Australia
1300 613 934
New Zealand
+64 9 377 3736
Hong Kong
+61 3 9670 6767
info@diadem.co
diadem.co

©Copyright Diadem Pty Ltd
Reproductions of the whole or part of this document constitutes an infringement of copyright. The information, ideas and concepts contained in this document are the intellectual property of the recipient(s) of this document. It is prohibited from disclosing such information to any person without the prior written consent of Diadem. Figured dimensions shall take precedence to scaled.

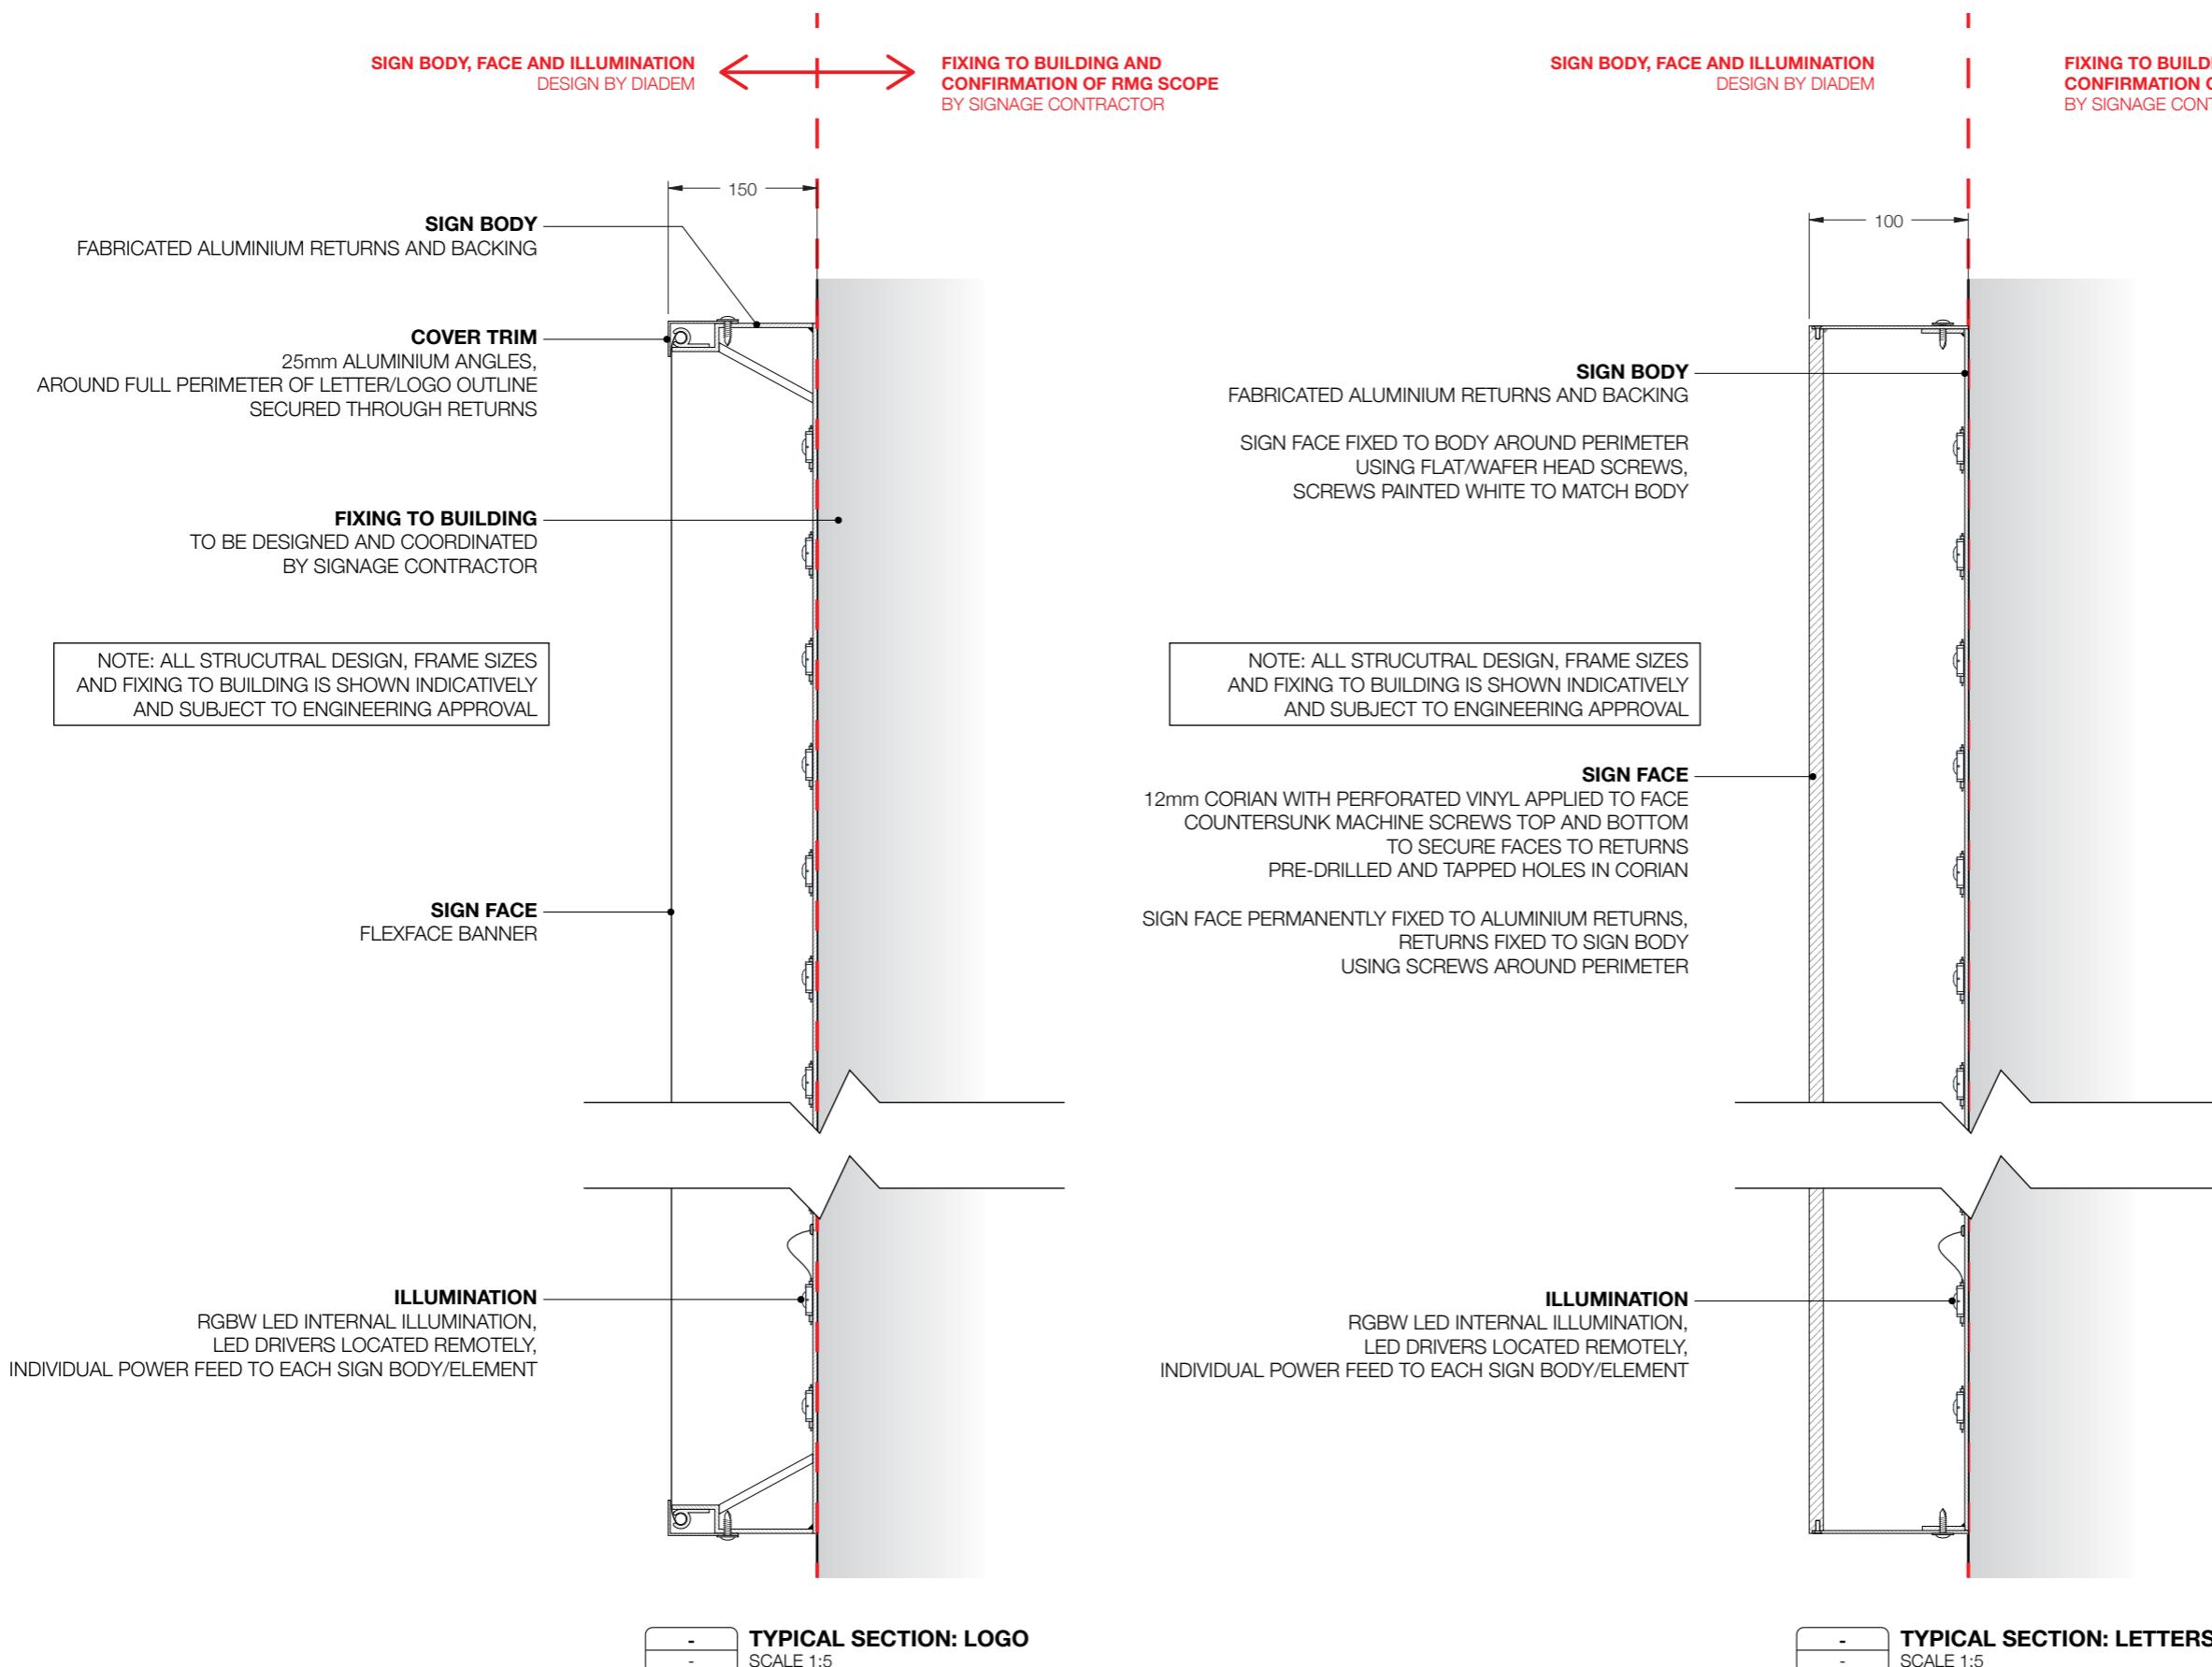

Adelaide Medical School Building

4 North Terrace
Adelaide SA 5000

Location 4

High level sign – stacked format
Wall mounted
Single sided
Illuminated

Drawing title _____

Removal scope



EXISTING CONDITIONS

RMG: REMOVE EXISTING SIGN AND REPLACE FAÇADE PANELS IMPACTED BY REMOVAL
CONTRACTOR TO MATCH EXISTING FAÇADE, A.U. TO PROVIDE DETAIL OF EXISTING PANEL REQUIREMENTS AND FIXINGS METHODS.
ACCESS: CRANE OR ROPE ACCESS FROM ROOF TO BE DETERMINED ON SITE BY CONTRACTOR WITH FACILITIES TEAM.
NOTE: REFER TO A.U. PROVIDED DOCUMENTATION FOR FURTHER INFORMATION.

Issue Issue date
ISSUE 04 03 APRIL 2025

Drawing no Scale
- @A3

PM Drawn Checked
RL CO CR/RL/NOW

Revision
- - -

Not for construction

General note: These drawings are prepared to communicate design intent only. All message content is indicative. All structural frames, footings and connections to be as per engineer's specifications and requirements. Contractor to ensure all materials, measurements, fixing details and methods are suitable for the site application before manufacture.

Client
ADELAIDE UNIVERSITY

Project
CITY WEST CAMPUS

Document file name
26304-DOC_CITY_WEST_SKY_SIGNS-04

diadem

Australia
1300 613 934

New Zealand
+64 9 377 3736

Hong Kong
+61 3 9670 6767
info@diadem.co
diadem.co

©Copyright Diadem Pty Ltd
Reproductions of the whole or part of this document constitutes an infringement of copyright. The information, ideas and concepts contained in this document are the intellectual property of Diadem. The recipient(s) of this document is prohibited from disclosing such information to any person without the prior written consent of Diadem. Figured dimensions shall take precedence to scaled.

Location 5

Jeffrey Smart Library

217/243 Hindley Street
Adelaide SA 5000

High level sign – stacked format
Wall mounted
Single sided
Illuminated

Drawing title

General arrangement

EXISTING CONDITIONS



PROPOSED LOCATION



SIGN LOCATION

SCALE 1:2000



LOCATION SPECIFIC INFORMATION

LOGO

FABRICATED ALUMINIUM, RETURNS PAINTED WHITE FLEXFACE SIGN FACES WITH BLUE DAY/NIGHT VINYL ALUMINIUM TRIM ANGLES TO SECURE SIGN FACE

LETTERS

FABRICATED ALUMINIUM, RETURNS PAINTED WHITE CORIAN SIGN FACES WITH BLUE DAY/NIGHT VINYL



LOGO AND LETTERS FIXED DIRECTLY TO BUILDING FACADE, INTERNALLY ILLUMINATED THROUGH FACES, SIGN TO ILLUMINATE WHITE AT NIGHT.

ALL INTERNAL SIGN FACES PAINTED WHITE

LED DRIVERS MUST BE INSTALLED IN AN AGREED-UPON ACCESSIBLE AREA AND, IF APPROPRIATE, THE REUSE OF THE EXISTING 240V SUPPLY FROM THE EXISTING SIGNS IS PREFERRED.

NOTE: EXISTING SIGN IS RECESSED INTO PRECAST CONCRETE FACADE
MAKE GOOD SCOPE WILL INCLUDE PROVISION OF NEW BACKING PANEL.
(TO BE CONFIRMED VIA SITE SURVEY)

EXISTING SIGN TO BE REMOVED.

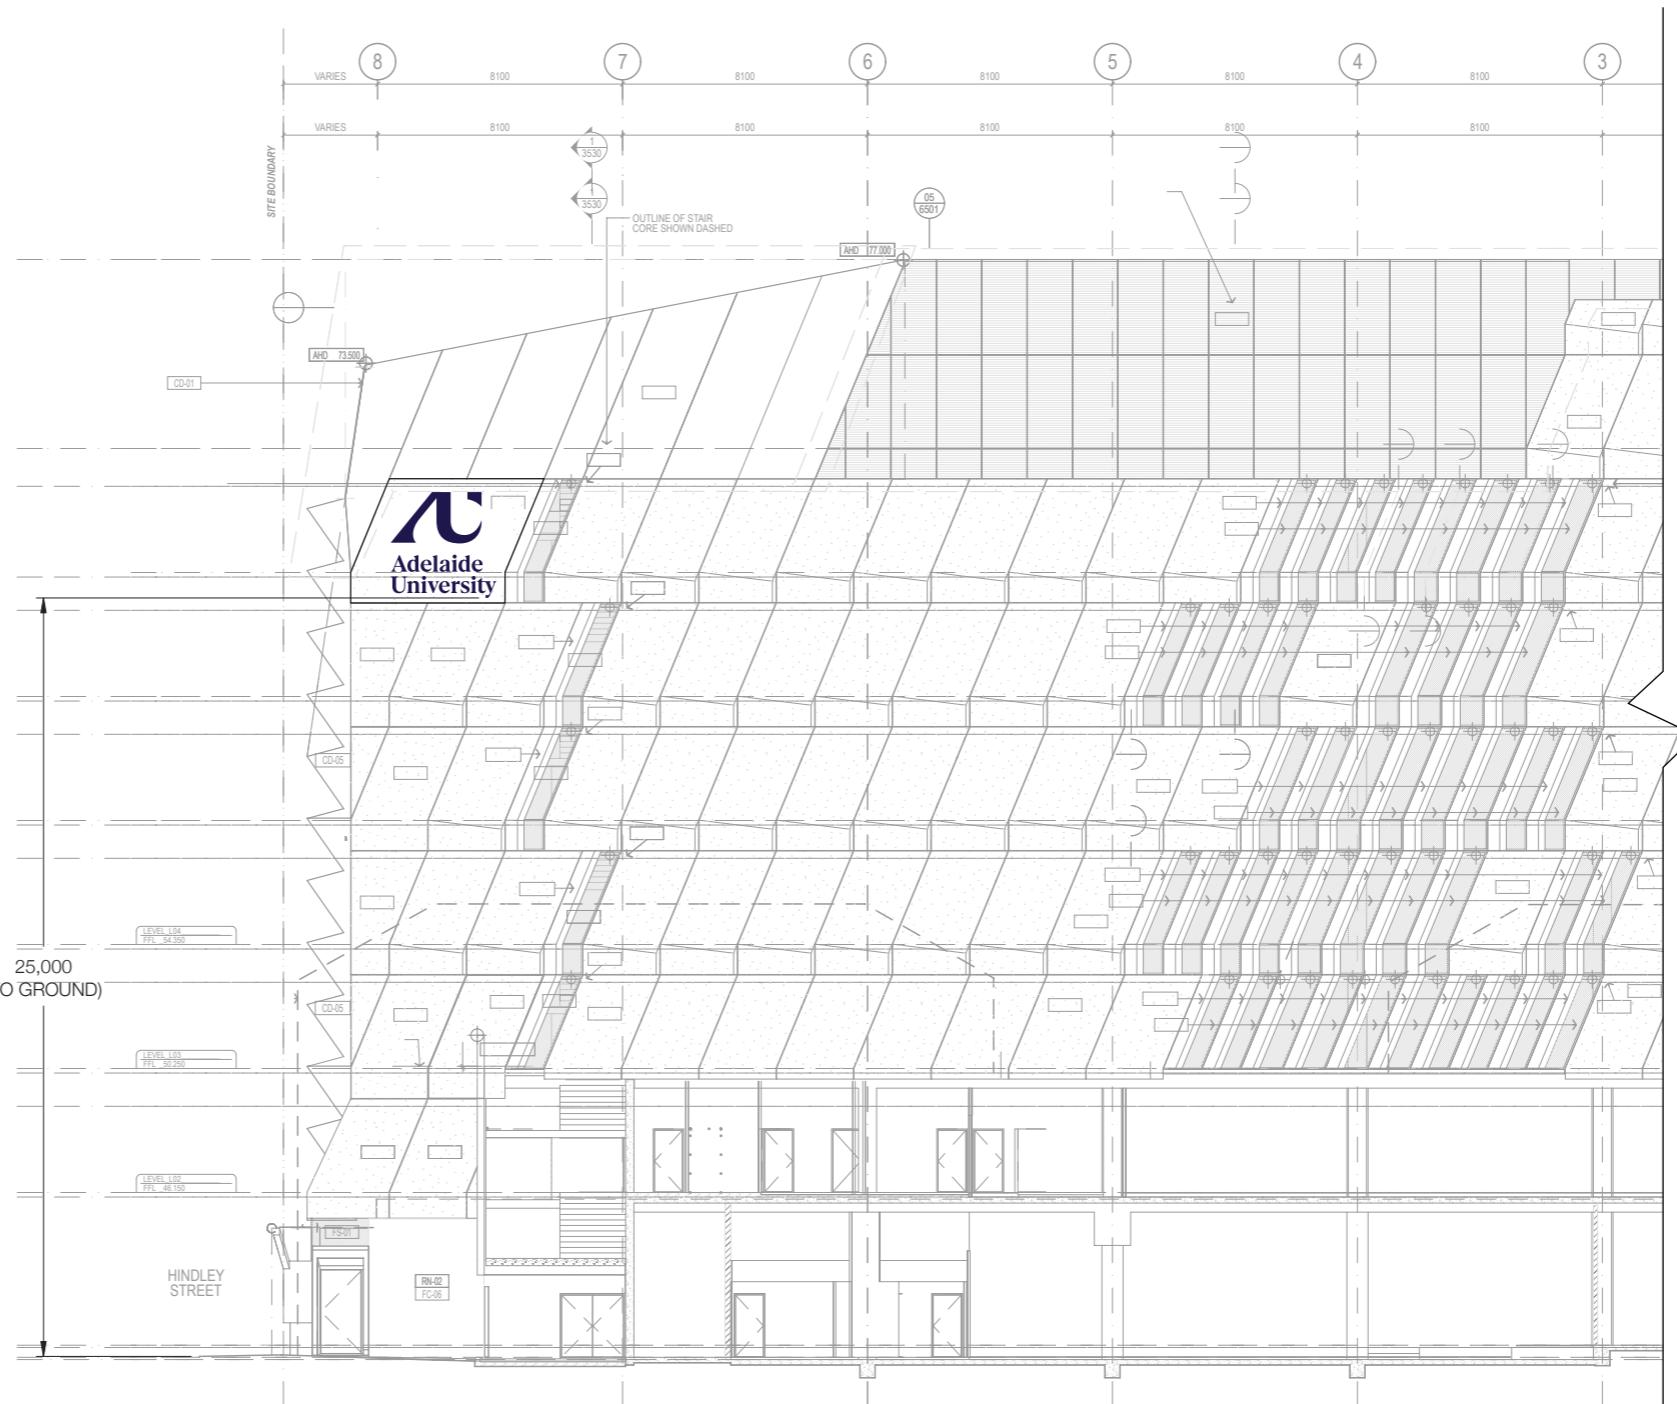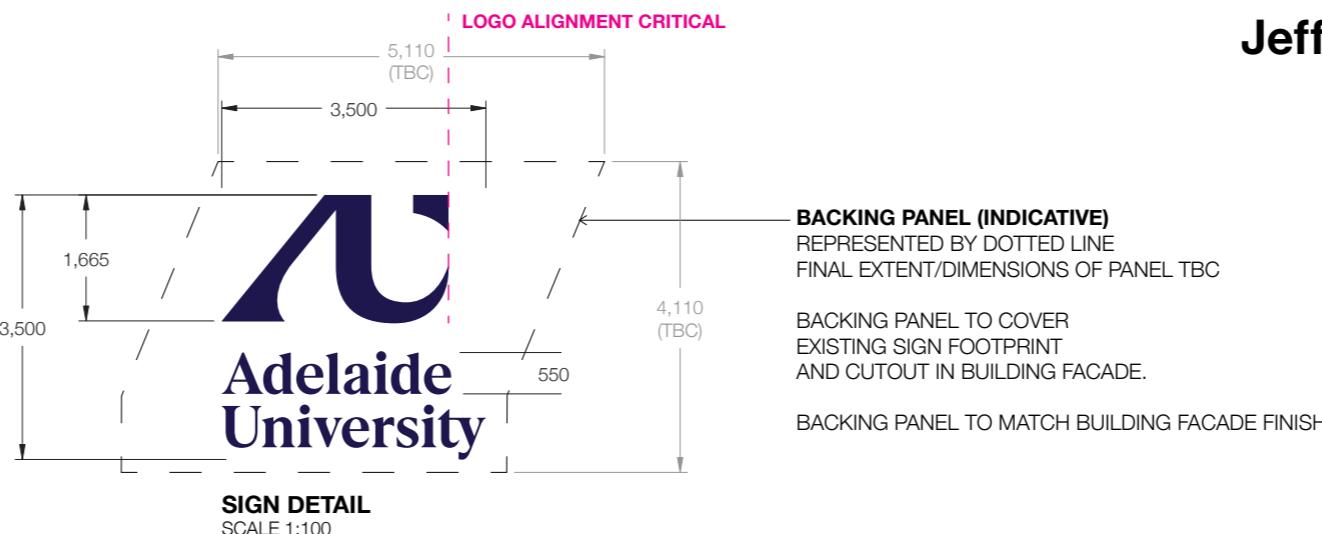

Issue	Issue date	
ISSUE 04	03 APRIL 2025	
Drawing no	Scale	
-	@A3	
PM	Drawn	Checked
RL	CO	CR/RL/NOW

Revision

Not for construction

General note: These drawings are prepared to communicate design intent only. All message content is indicative. All structural frames, footings and connections to be as per engineer's specifications and requirements. Contractor to ensure all materials, measurements, fixing details and methods are suitable for the site application before manufacture.

Client
ADELAIDE UNIVERSITY

Project
CITY WEST CAMPUS

Document file name
26304-DOC_CITY_WEST_SKY_SIGNS-04

diadem

Australia
1300 613 934

New Zealand
+64 9 377 3736

Hong Kong
+61 3 9670 6767
info@diadem.co
diadem.co

©Copyright Diadem Pty Ltd
Reproductions of the whole or part of this document constitutes an infringement of copyright. The information, ideas and concepts contained in this document are the intellectual property of the recipient(s). It is prohibited from disclosing such information to any person without the prior written consent of Diadem. Figured dimensions shall take precedence to scaled.

High level sign – stacked format
Wall mounted
Single sided
Illuminated

Drawing title

Section detail

Issue Issue date
ISSUE 04 03 APRIL 2025

Drawing no Scale
- @A3

PM Drawn Checked
RL CO CR/RL/NOW

Revision
- - -

Not for construction

General note: These drawings are prepared to communicate design intent only. All message content is indicative. All structural frames, footings and connections to be as per engineer's specifications and requirements. Contractor to ensure all materials, measurements, fixing details and methods are suitable for the site application before manufacture.

Client
ADELAIDE UNIVERSITY


Project
CITY WEST CAMPUS

Document file name
26304-DOC_CITY_WEST_SKY_SIGNS-04

diadem

Australia
1300 613 934
New Zealand
+64 9 377 3736
Hong Kong
+61 3 9670 6767
info@diadem.co
diadem.co

©Copyright Diadem Pty Ltd
Reproductions of the whole or part of this document constitutes an infringement of copyright. The information, ideas and concepts contained in this document are the intellectual property of the recipient(s) of this document. It is prohibited from disclosing such information to any person without the prior written consent of Diadem. Figured dimensions shall take precedence to scaled.

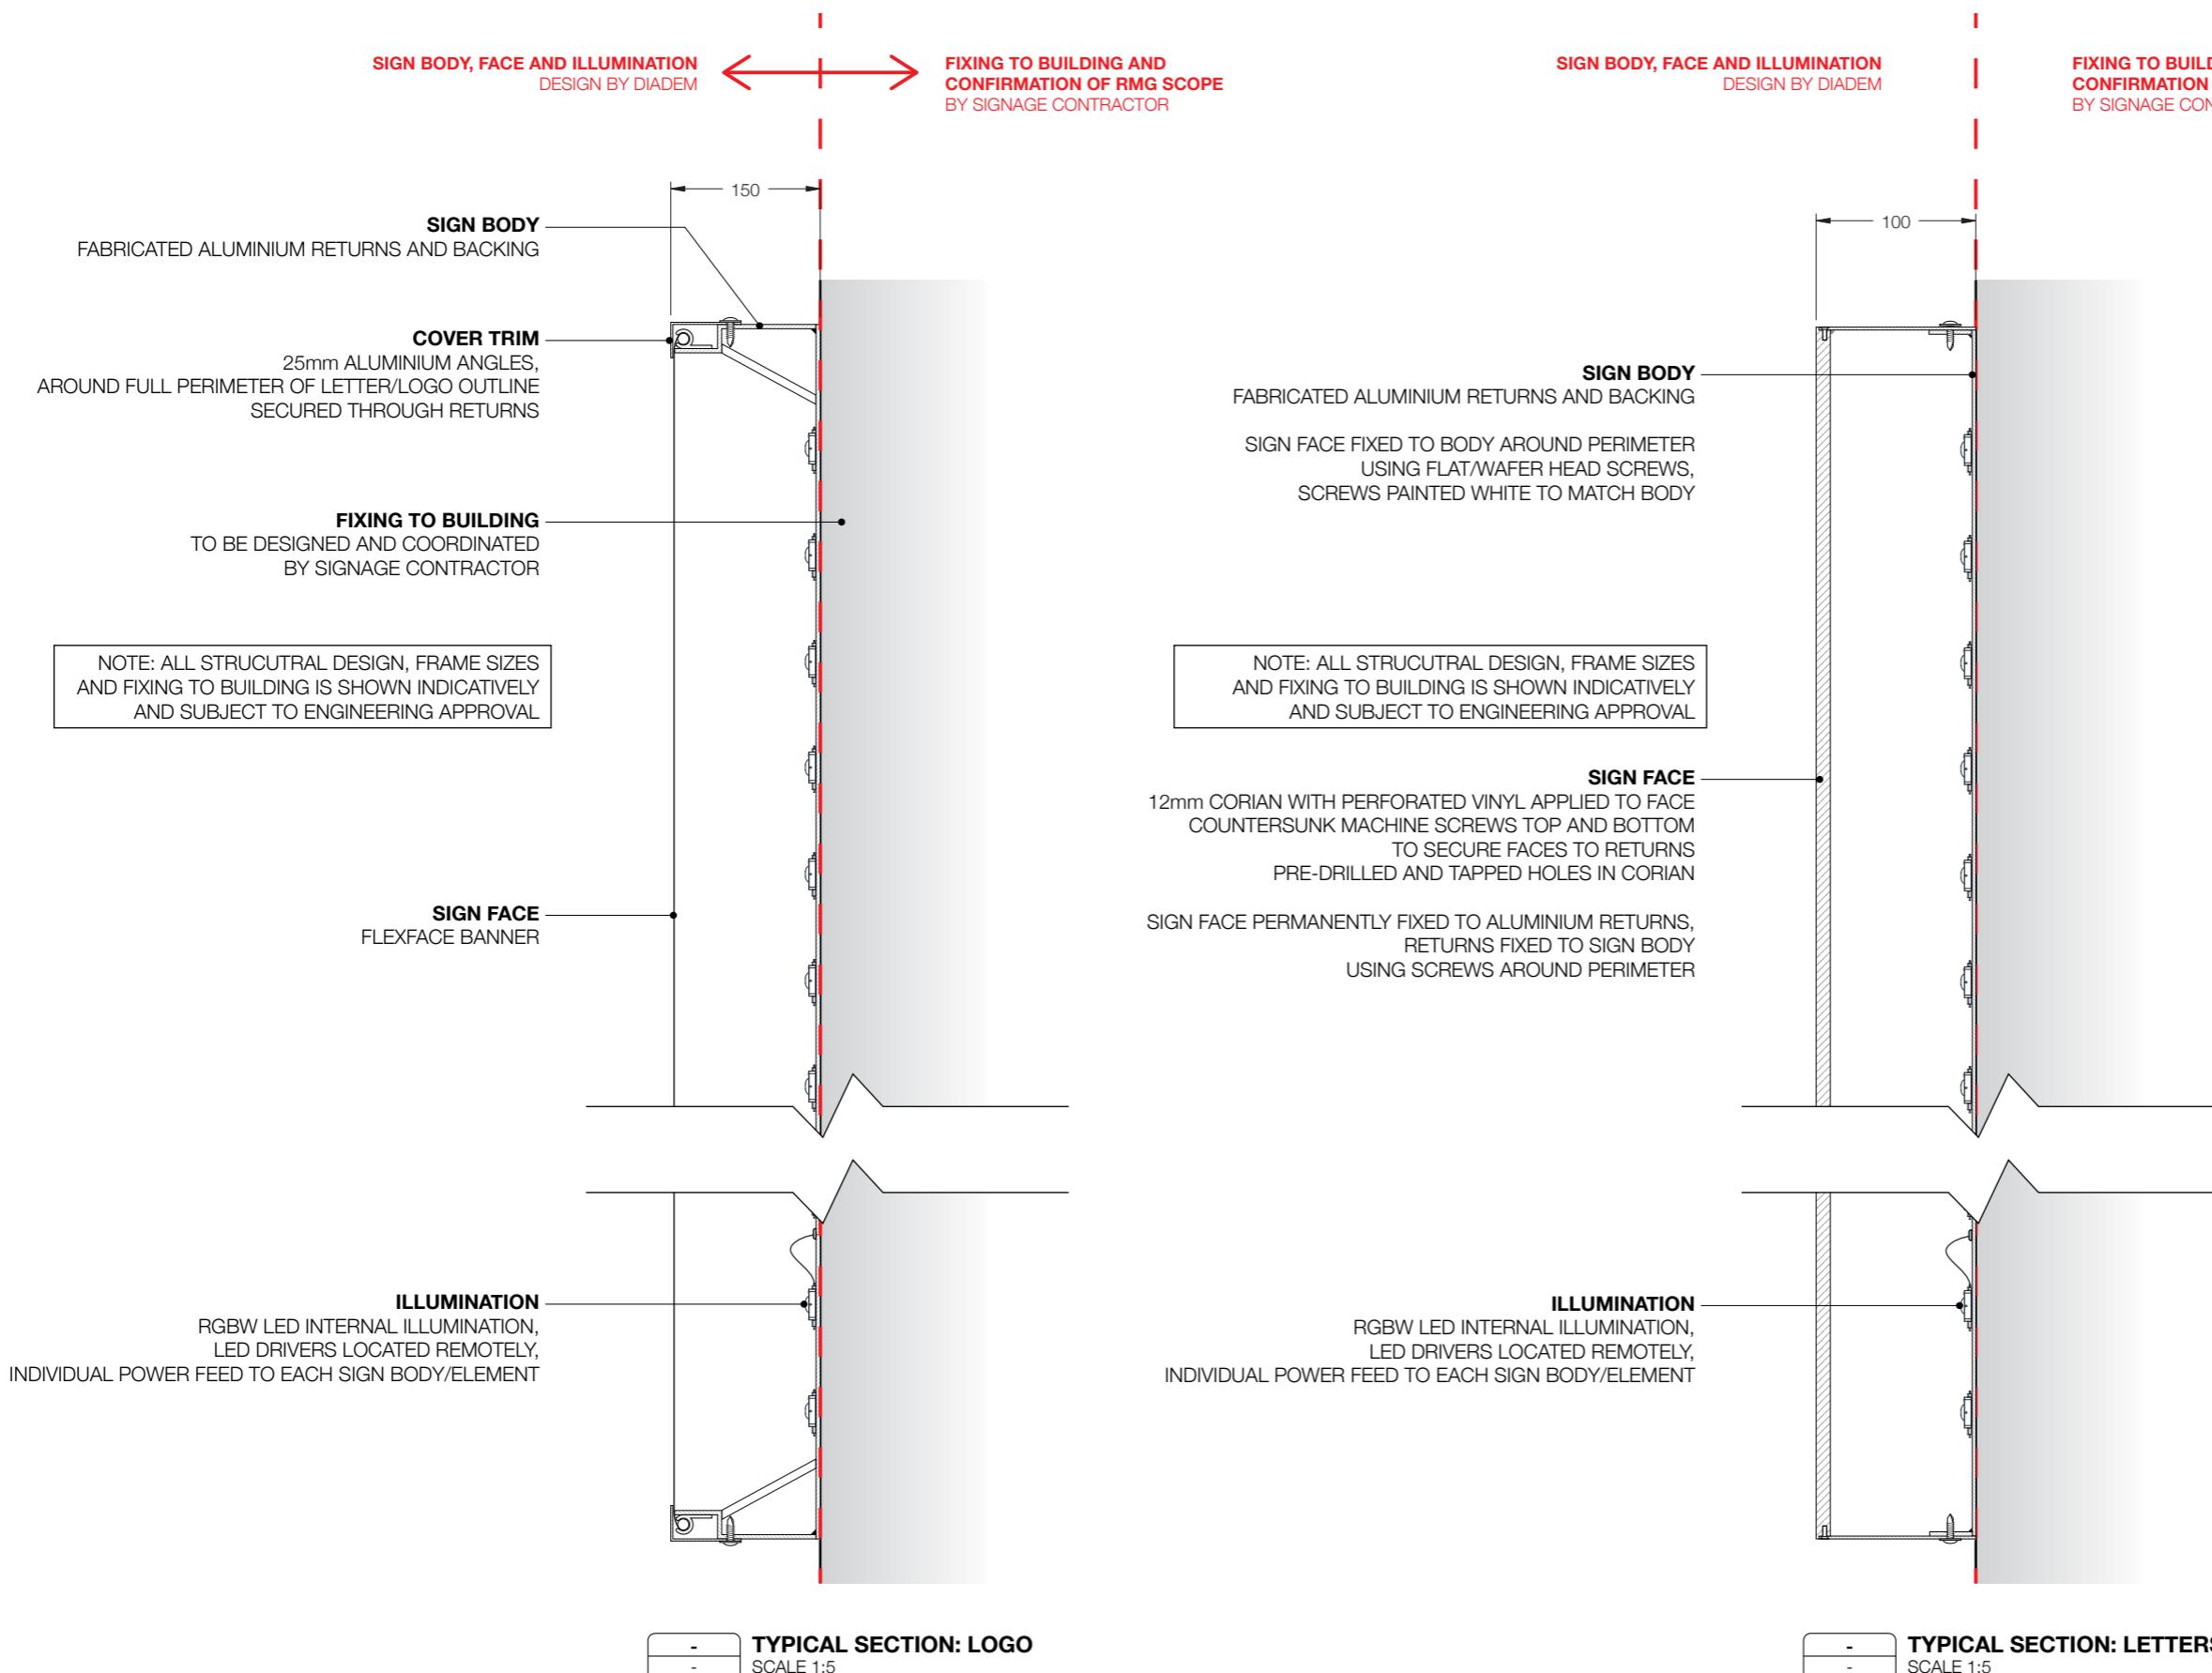

Jeffrey Smart Library

217/243 Hindley Street
Adelaide SA 5000

Location 5

High level sign –
stacked format
Wall mounted
Single sided
Illuminated

Drawing title _____

Removal scope



EXISTING CONDITIONS

RMG: REMOVE EXISTING SIGN AND WATERPROOF AREA.
BACKGROUND PANEL – FOR SIGN COVERING EXTENT OF IMPACTED CONCRETE
PANEL – TO MATCH EXISTING COLOUR OF FAÇADE.
ACCESS: CRANE FROM ROAD.
CONTRACTOR TO ALLOW FOR ALL RELEVANT AUTHORITY AND TRAFFIC
MANAGEMENT REQUIREMENTS FOR INSTALLATION.
NOTE: REFER TO A.U. PROVIDED DOCUMENTATION FOR FURTHER INFORMATION.

Issue Issue date
ISSUE 04 03 APRIL 2025

Drawing no Scale
- @A3

PM Drawn Checked
RL CO CR/RL/NOW

Revision
- - -

Not for construction

General note: These drawings are prepared to communicate design intent only. All message content is indicative. All structural frames, footings and connections to be as per engineer's specifications and requirements. Contractor to ensure all materials, measurements, fixing details and methods are suitable for the site application before manufacture.

Client
ADELAIDE UNIVERSITY

Project
CITY WEST CAMPUS

Document file name
26304-DOC_CITY_WEST_SKY_SIGNS-04

diadem

Australia
1300 613 934

New Zealand
+64 9 377 3736

Hong Kong
+61 3 9670 6767
info@diadem.co
diadem.co

©Copyright Diadem Pty Ltd
Reproductions of the whole or part of this document constitutes an infringement of copyright. The information, ideas and concepts contained in this document are the intellectual property of Diadem. The recipient(s) of this document is prohibited from disclosing such information to any person without the prior written consent of Diadem. Figured dimensions shall take precedence to scaled.

Jeffrey Smart Library

217/243 Hindley Street
Adelaide SA 5000

High level sign – stacked format
Wall mounted
Single sided
Illuminated

Drawing title

General arrangement



EXISTING CONDITIONS



PROPOSED LOCATION



SIGN LOCATION

SCALE 1:2000



LOCATION SPECIFIC INFORMATION

LOGO

FABRICATED ALUMINIUM, RETURNS PAINTED WHITE FLEXFACE SIGN FACES WITH BLUE DAY/NIGHT VINYL ALUMINIUM TRIM ANGLES TO SECURE SIGN FACE

LETTERS



FABRICATED ALUMINIUM, RETURNS PAINTED WHITE CORIAN SIGN FACES WITH BLUE DAY/NIGHT VINYL

LOGO AND LETTERS FIXED DIRECTLY TO BUILDING FAÇADE, INTERNALLY ILLUMINATED THROUGH FACES, SIGN TO ILLUMINATE WHITE AT NIGHT.

ALL INTERNAL SIGN FACES PAINTED WHITE

LED DRIVERS MUST BE INSTALLED IN AN AGREED-UPON ACCESSIBLE AREA AND, IF APPROPRIATE, THE REUSE OF THE EXISTING 240V SUPPLY FROM THE EXISTING SIGNS IS PREFERRED.

NOTE: EXISTING SIGN IS RECESSED INTO PRECAST CONCRETE FAÇADE
MAKE GOOD SCOPE WILL INCLUDE PROVISION OF NEW BACKING PANEL.
(TO BE CONFIRMED VIA SITE SURVEY)
EXISTING SIGN TO BE REMOVED.

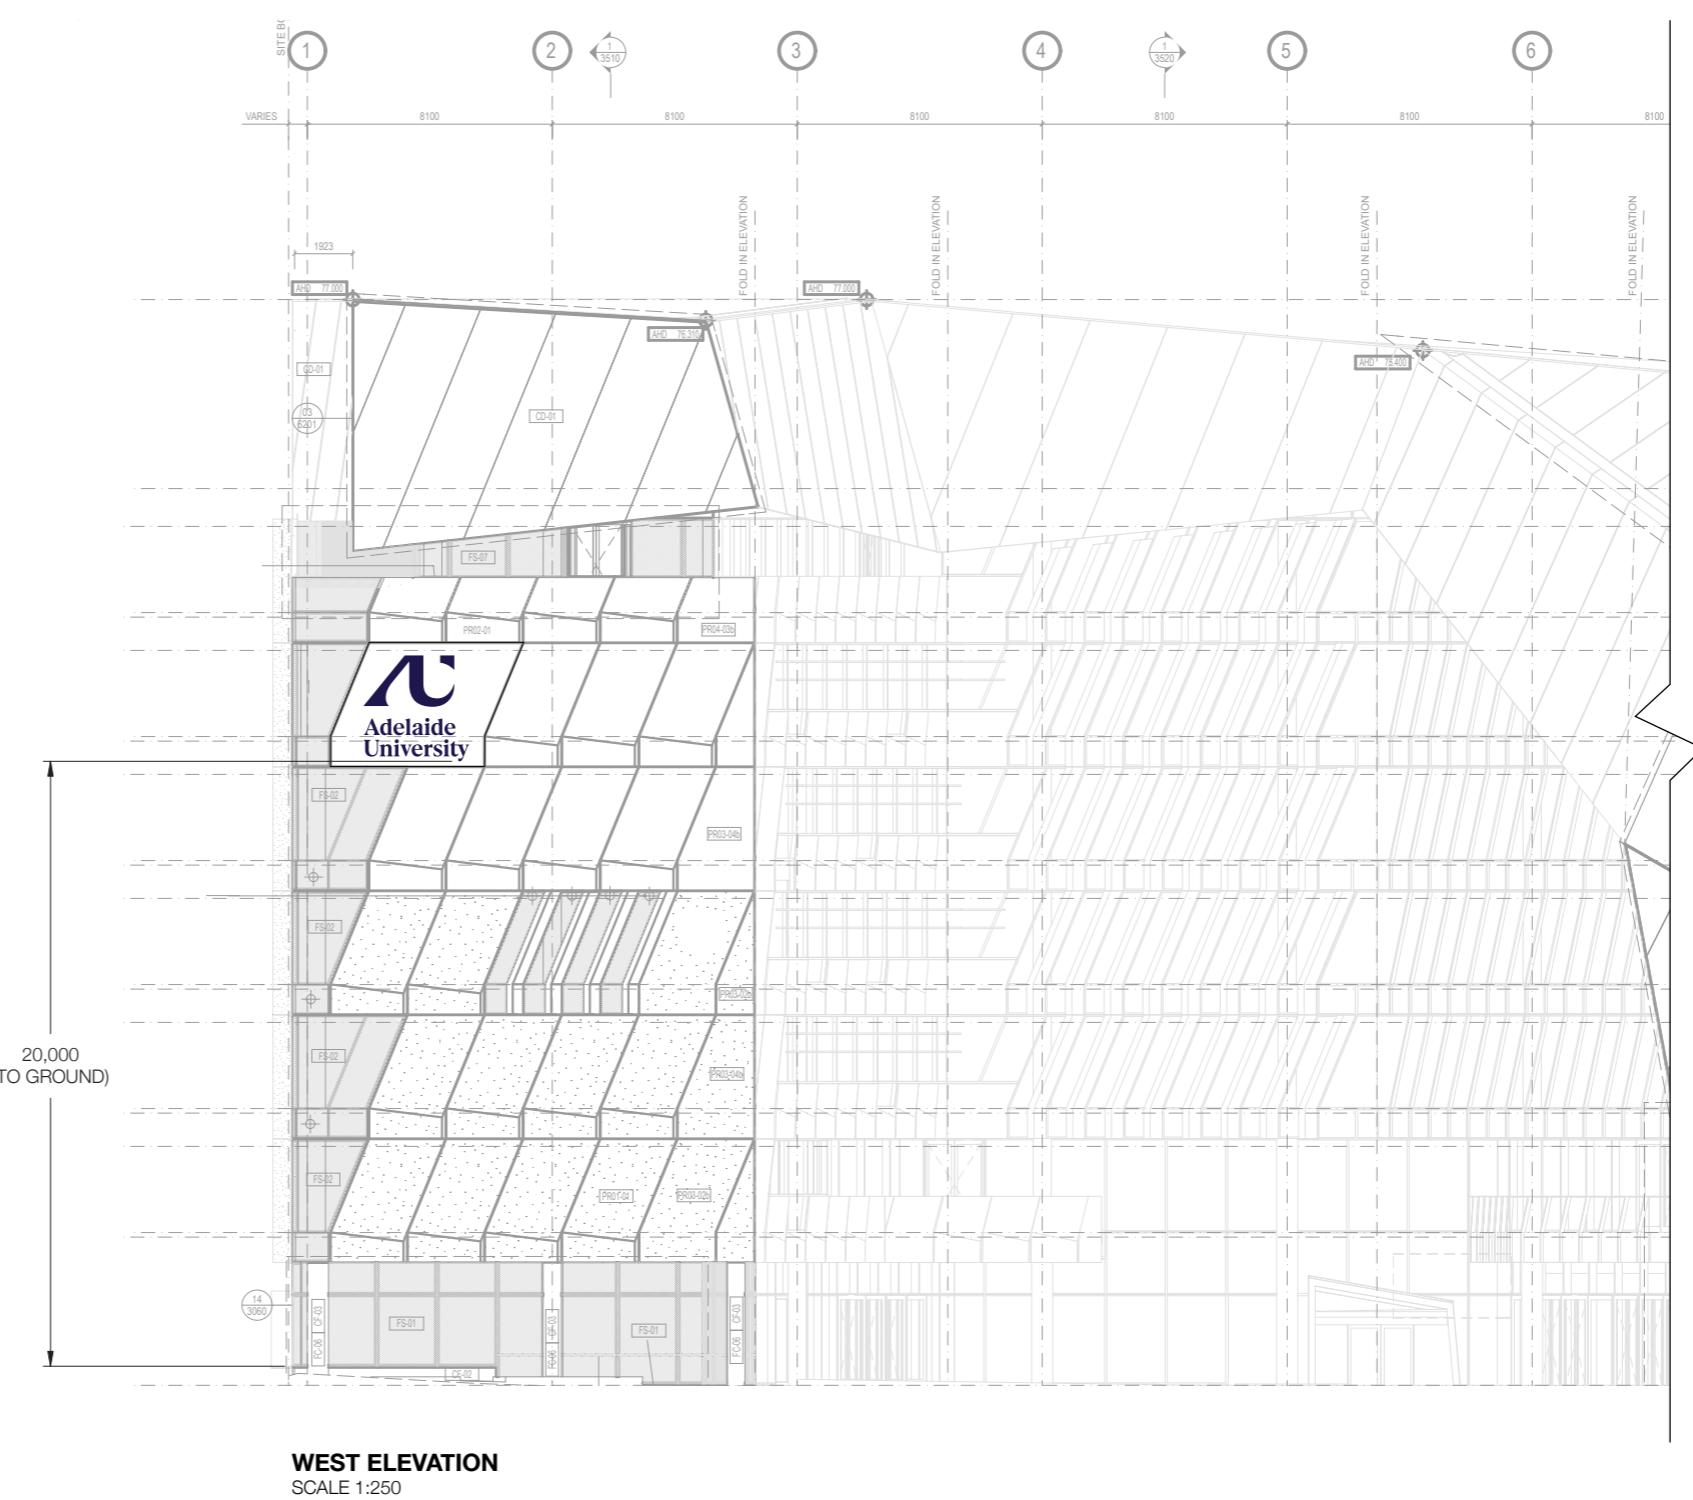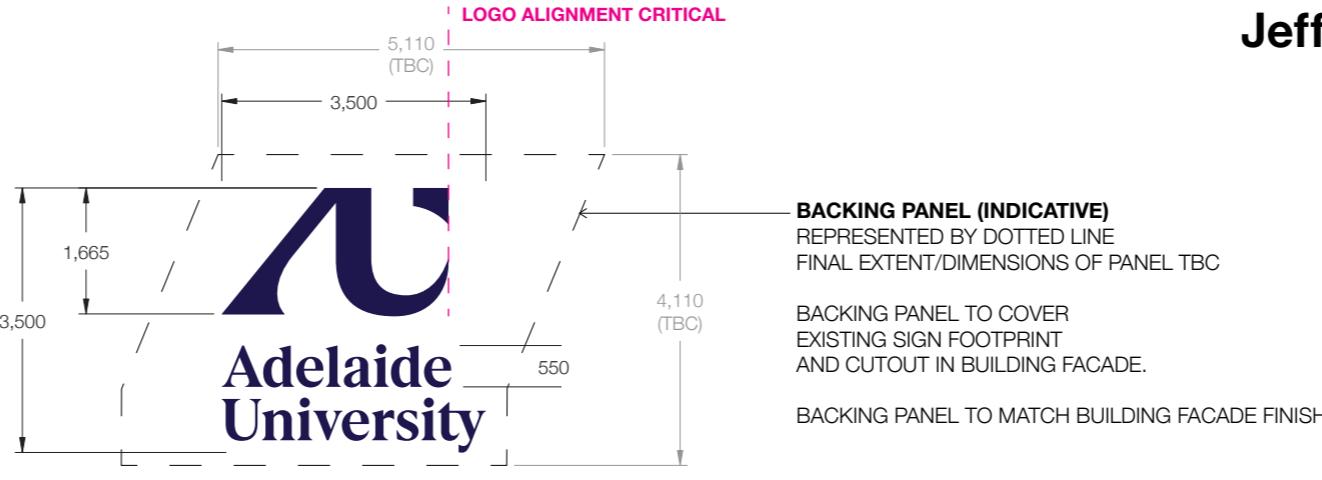

Issue Issue date
ISSUE 04 03 APRIL 2025

Drawing no Scale
- @A3

PM Drawn Checked
RL CO CR/RL/NOW

Revision

Not for construction

General note: These drawings are prepared to communicate design intent only. All message content is indicative. All structural frames, footings and connections to be as per engineer's specifications and requirements. Contractor to ensure all materials, measurements, fixing details and methods are suitable for the site application before manufacture.

Client
ADELAIDE UNIVERSITY

Project
CITY WEST CAMPUS

Document file name
26304-DOC_CITY_WEST_SKY_SIGNS-04

diadem

Australia

1300 613 934

New Zealand

+64 9 377 3736

Hong Kong

+61 3 9670 6767

info@diadem.co

diadem.co

©Copyright Diadem Pty Ltd

Reproductions of the whole or part of this document constitutes an infringement of copyright. The information, ideas and concepts contained in this document are the intellectual property of the recipient(s) of this document. It is prohibited from disclosing such information to any person without the prior written consent of Diadem. Figured dimensions shall take precedence to scaled.

High level sign – stacked format
Wall mounted
Single sided
Illuminated

Drawing title

Section detail

Issue Issue date
ISSUE 04 03 APRIL 2025

Drawing no Scale
- @A3

PM Drawn Checked
RL CO CR/RL/NOW

Revision
- - -

Not for construction

General note: These drawings are prepared to communicate design intent only. All message content is indicative. All structural frames, footings and connections to be as per engineer's specifications and requirements. Contractor to ensure all materials, measurements, fixing details and methods are suitable for the site application before manufacture.

Client
ADELAIDE UNIVERSITY

Project
CITY WEST CAMPUS

Document file name
26304-DOC_CITY_WEST_SKY_SIGNS-04

diadem


Australia
1300 613 934

New Zealand
+64 9 377 3736

Hong Kong
+61 3 9670 6767

info@diadem.co
diadem.co

©Copyright Diadem Pty Ltd
Reproductions of the whole or part of this document constitutes an infringement of copyright. The information, ideas and concepts contained in this document are the intellectual property of Diadem. The recipient(s) of this document is prohibited from disclosing such information to any person without the prior written consent of Diadem. Figured dimensions shall take precedence to scaled.

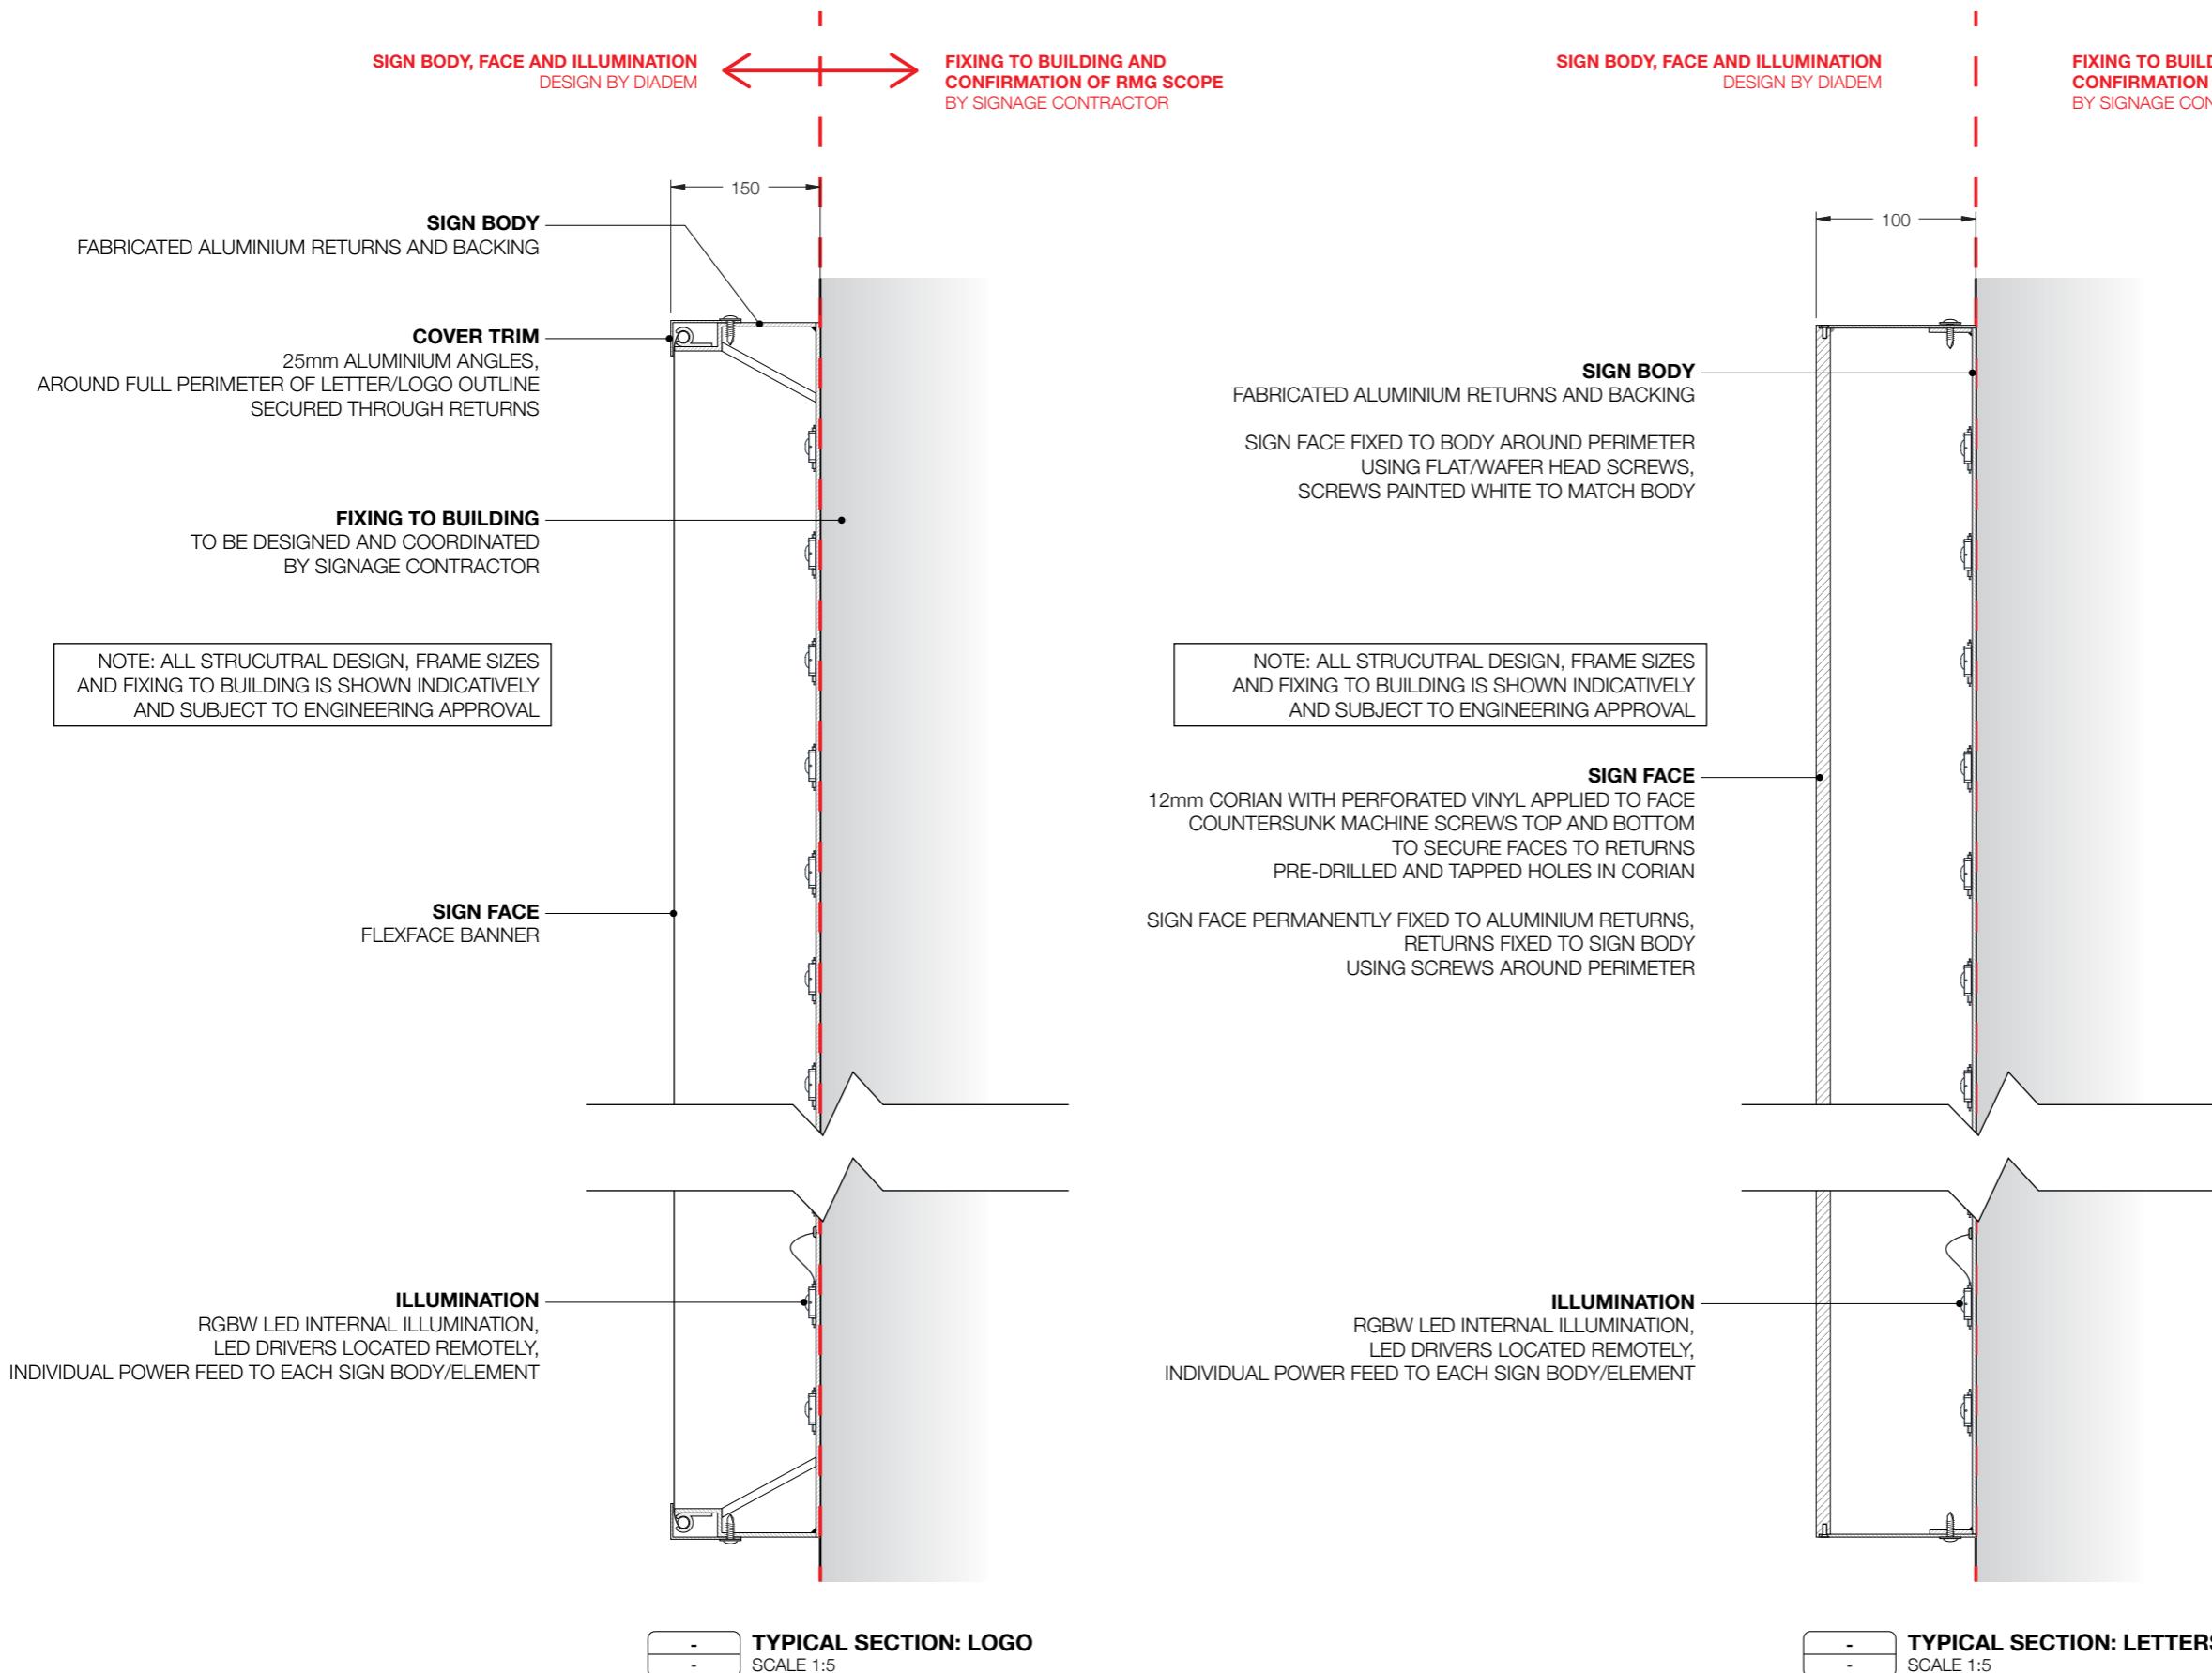

Jeffrey Smart Library

217/243 Hindley Street
Adelaide SA 5000

Location 12

High level sign –
stacked format
Wall mounted
Single sided
Illuminated

Drawing title _____

Removal scope



EXISTING CONDITIONS

RMG: REMOVE EXISTING SIGN AND WATERPROOF AREA.
BACKGROUND PANEL – FOR SIGN COVERING EXTENT OF IMPACTED CONCRETE
PANEL – TO MATCH EXISTING COLOUR OF FAÇADE.
ACCESS: CRANE FROM ROAD.
CONTRACTOR TO ALLOW FOR ALL RELEVANT AUTHORITY AND TRAFFIC
MANAGEMENT REQUIREMENTS FOR INSTALLATION.
NOTE: REFER TO A.U. PROVIDED DOCUMENTATION FOR FURTHER INFORMATION.

Issue Issue date
ISSUE 04 03 APRIL 2025

Drawing no Scale
- @A3

PM Drawn Checked
RL CO CR/RL/NOW

Revision
- - -

Not for construction

General note: These drawings are prepared to communicate design intent only. All message content is indicative. All structural frames, footings and connections to be as per engineer's specifications and requirements. Contractor to ensure all materials, measurements, fixing details and methods are suitable for the site application before manufacture.

Client
ADELAIDE UNIVERSITY

Project
CITY WEST CAMPUS

Document file name
26304-DOC_CITY_WEST_SKY_SIGNS-04

diadem

Australia

1300 613 934

New Zealand

+64 9 377 3736

Hong Kong

+61 3 9670 6767

info@diadem.co

diadem.co

©Copyright Diadem Pty Ltd
Reproductions of the whole or part of this document constitutes an infringement of copyright. The information, ideas and concepts contained in this document are the copyright of Diadem Pty Ltd. The recipient(s) of this document is prohibited from disclosing such information to any person without the prior written consent of Diadem. Figured dimensions shall take precedence to scaled.

